

PROYECTO

Reforma integral de local de hostelería

EMPLAZAMIENTO

Local en planta baja y altillo Málaga

PLANO

PLANTA BAJA

Estado actual · estructura

LEYENDA

- Muro de carga / medianera
- Pilar o machón de hormigón
- Pared en L nueva (apoyo del vidrio)
- Carpintería acristalada
- Espacio de doble altura
- Forjado sobre el corte
- Reserva de espacio del cliente
- Mesas dobles de 0,70 × 0,70 y sillas
- Itinerario accesible ≥ 1,20 · giro Ø 1,50
- Punto de luz s/ proyecto original
- Aire acondicionado (cassette de techo)

SUPERFICIES Y ALTURAS

|                                |              |
|--------------------------------|--------------|
| Planta baja, dentro de muros   | 76,23 m²     |
| Zona de doble altura           | 38,40 m²     |
| Suelo a suelo, medido en obra  | 2,56 m       |
| Altura libre bajo forjado      | 2,56 – canto |
| Pared en L, altura             | 1,22 m       |
| Mesas dobles / plazas sentadas | 11 / 22      |
| Acristalamiento de fachada     | ≈ 4,70 m     |

PILARES Y MACHONES (secciones en m)

|                                |             |
|--------------------------------|-------------|
| P1 Machón del muro Oeste       | 0,30 × 0,60 |
| P2 Pilastra del muro Sur       | 0,58 × 0,45 |
| P3 Pilar central               | 0,65 × 1,07 |
| P4 Machón de la medianera Este | 0,20 × 0,60 |
| P5 Pilar de fachada            | 0,60 × 1,00 |

NOTAS

Cotas en metros. Hundimiento, pared en L, P3, barra, zócalo y puerta con las medidas del 19 set.; el resto, del levantamiento. ±0,00 en el pavimento, sección a 1,20 m. Equipamiento en la lámina 03. Mesas dobles de 0,70 × 0,70 que el personal junta para formar mesas de cuatro. M4 pegada a P3. Luces: las del proyecto original; los dos cassettes de aire, situados con las fotos del cliente. Itinerario accesible de 1,20 de la puerta a la barra, al baño y a la plaza PMR de M1, con giros de Ø 1,50 en la entrada y ante el baño; el baño no es accesible.



ESCALA


1:50 (A3)

FECHA

19 set. 2026

PLANO

01 / 04

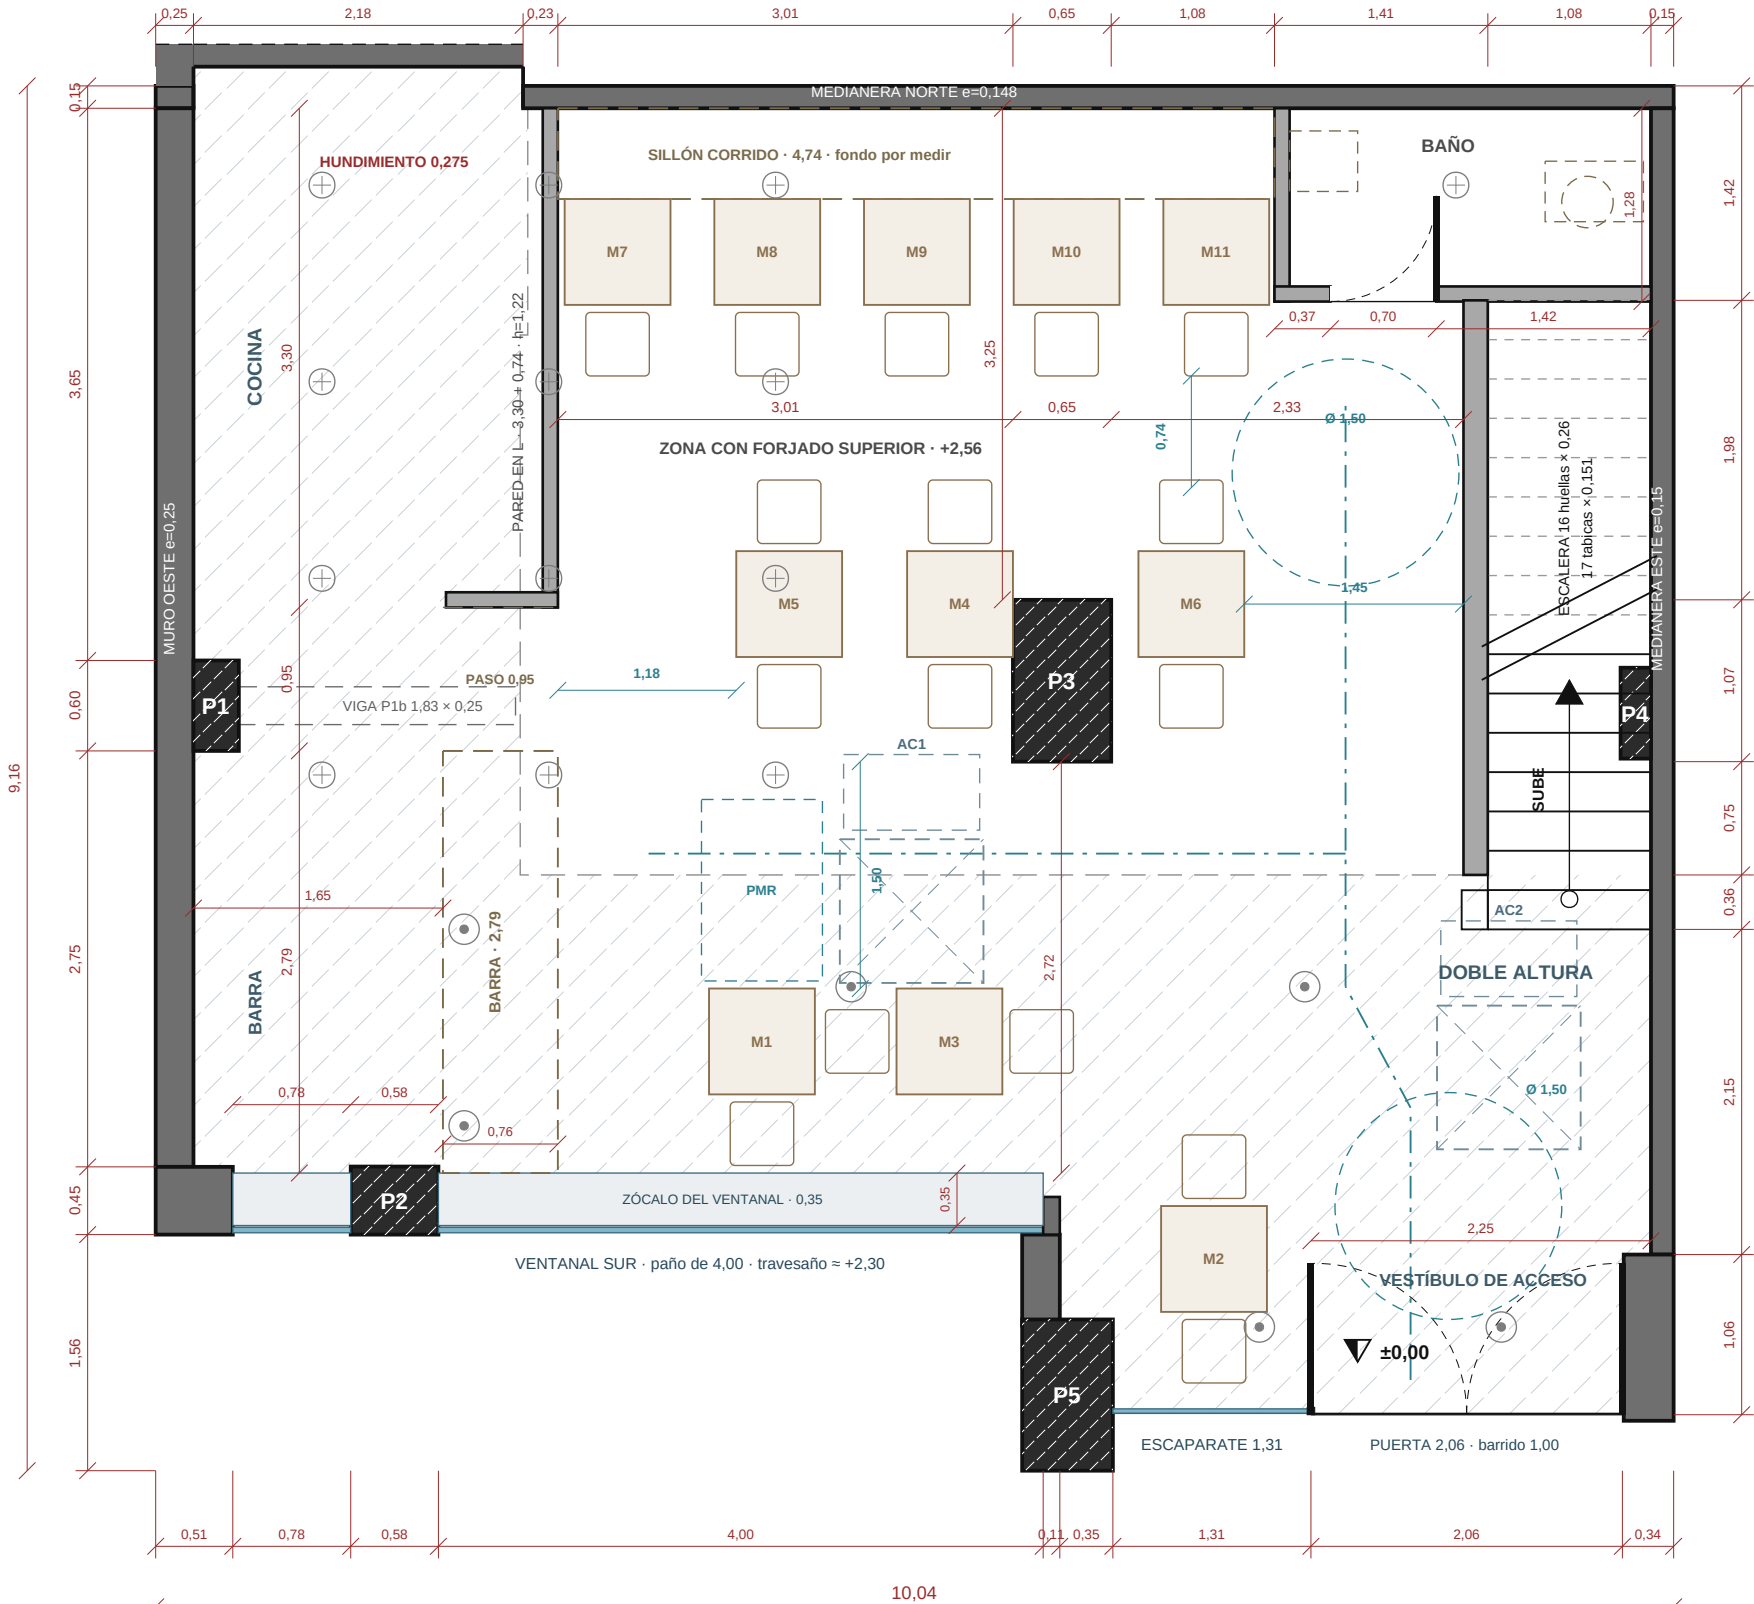

COMPROBAR EN OBRA Puntos en los que los vídeos del local no cuadran con el levantamiento, o que el levantamiento no recoge. Se dibuja el levantamiento por ser la única fuente acotada.

- Hundimiento de la medianera Norte: 0,275 de fondo en los 2,18 de la cocina. Supera el espesor dibujado (0,148): medir ese cerramiento y lo que hay detrás.
- Canto del forjado del altillo. Con 2,56 m de suelo a suelo, la altura libre de planta baja es 2,56 menos ese canto, no los 2,70 supuestos.
- P1b se dibuja como viga (1,83 × 0,25) y no como pilar: si fuera macizo hasta el suelo, la cocina no tendría entrada. Medir su intradós.
- Zócalo del ventanal: 0,347 desde el vidrio, deducido de los 2,72 de P3 a su cara interior; sobresale 0,16 del muro del ventanal (0,25). Medirlo directamente.
- Cadena Este-Oeste del cliente (2,18 + 3,01 + 0,65 + 2,33): cierra contra la escalera con 0,13 de pared entre el hundimiento y la L y 0,16 de cerramiento.
- La pared en L queda 0,10 al Este del borde del forjado del levantamiento: el vidrio de 1,35 sobre ella (2,57 en total) no pasa bajo el altillo. Medir ese borde.
- Vestíbulo: los 1,31 y 2,23 del cliente suman 3,54 y de P5 al muro Este hay 3,559. Se dibuja el 1,31 medido y el resto queda en 2,25, 2 cm más que su medida.
- P3 no se mueve: sus 3,23 a la medianera Norte y 3,65 a la cara Norte de P5 lo llevarían 2 cm al Sur y 4 cm al Norte. Se dibujan 3,25 y 3,69. Medir de nuevo.
- Aire acondicionado: dos cassettes situados con las fotos del cliente, con panel estándar de 0,95 y rejilla de 0,90 × 0,50. Medir posición y tamaño reales.

# GRUPO SUMA

Reformas y proyectos · Málaga

## PROYECTO

Reforma integral de local de hostelería

## EMPLAZAMIENTO

Local en planta baja y altílo  
Málaga

## PLANO

PLANTA ALTA

Altílo +2,56 · estructura

## LEYENDA

- Muro de carga / medianera
- Pilar o machón de hormigón
- Tabiquería
- Barandilla de vidrio
- Mesas y sillas (medidas promedio)
- Paso libre entre mobiliario (m)
- Vacío sobre planta baja

## SUPERFICIES Y ALTURAS

|                           |          |
|---------------------------|----------|
| Forjado de planta alta    | 33,74 m² |
| Altílo diáfano            | 26,17 m² |
| Aseo (lavabo + inodoro)   | 3,92 m²  |
| Almacén                   | 2,59 m²  |
| Nivel del forjado, medido | +2,56 m  |
| Puestos de cowork         | 14       |

## PILARES Y MACHONES (secciones en m)

|                                |             |
|--------------------------------|-------------|
| P1 Machón del muro Oeste       | 0,30 × 0,60 |
| P2 Pilastra del muro Sur       | 0,58 × 0,45 |
| P3 Pilar central               | 0,65 × 1,07 |
| P4 Machón de la medianera Este | 0,20 × 0,60 |
| P5 Pilar de fachada            | 0,60 × 1,00 |

## NOTAS

Cotas en metros, tomadas sobre el levantamiento.


Nivel del forjado +2,56, medido en obra.

El forjado del altílo no cubre todo el local: la franja sur y oeste es un vacío a doble altura.

Mesa de cowork 2,40 × 1,00 para 8 puestos y una redonda de Ø 1,20 con 6 sillas. Medidas promedio.

Pasos libres entre mobiliario acotados en azul:


1,01 hacia el aseo y el almacén; 1,30 en el desembarco; 0,26 a 0,85 en los accesos a las sillas.

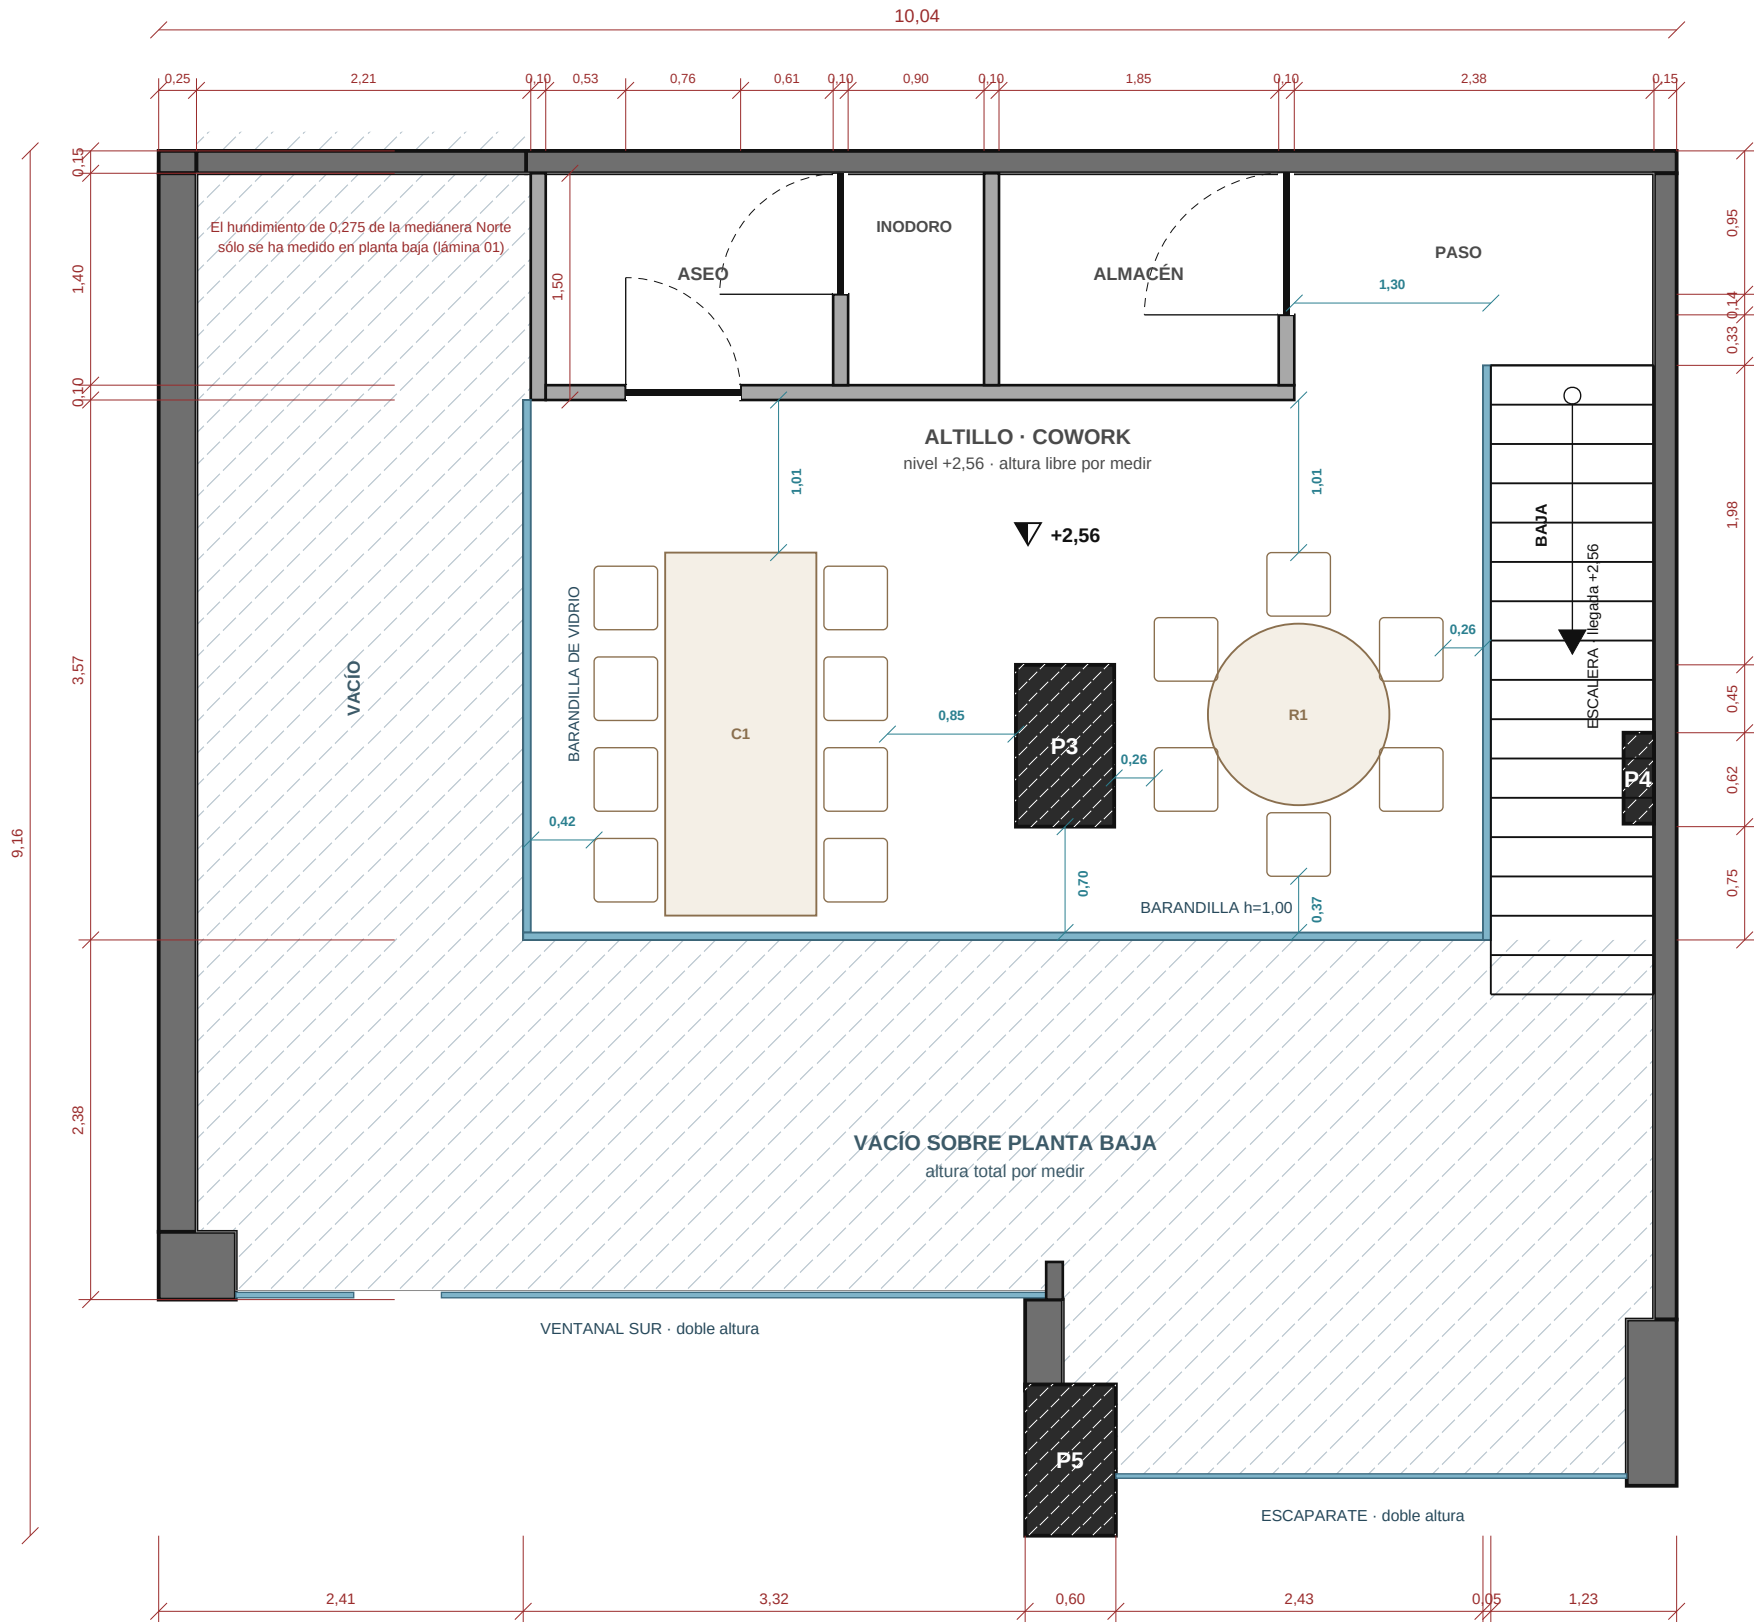

## COMPROBAR EN OBRA

Puntos en los que los vídeos del local no cuadran con el levantamiento, o que el levantamiento no recoge. Se dibuja el levantamiento por ser la única fuente acotada.

- Hundimiento de la medianera Norte: 0,275 de fondo en los 2,18 de la cocina. Supera el espesor dibujado (0,148): medir ese cerramiento y lo que hay detrás.
- Canto del forjado del altílo. Con 2,56 m de suelo a suelo, la altura libre de planta baja es 2,56 menos ese canto, no los 2,70 supuestos.
- P1b se dibuja como viga (1,83 × 0,25) y no como pilar: si fuera macizo hasta el suelo, la cocina no tendría entrada. Medir su intradós.
- Zócalo del ventanal: 0,347 desde el vidrio, deducido de los 2,72 de P3 a su cara interior; sobresale 0,16 del muro del ventanal (0,25). Medirlo directamente.
- Cadena Este-Oeste del cliente (2,18 + 3,01 + 0,65 + 2,33): cierra contra la escalera con 0,13 de pared entre el hundimiento y la L y 0,16 de cerramiento.
- La pared en L queda 0,10 al Este del borde del forjado del levantamiento: el vidrio de 1,35 sobre ella (2,57 en total) no pasa bajo el altílo. Medir ese borde.
- Vestíbulo: los 1,31 y 2,23 del cliente suman 3,54 y de P5 al muro Este hay 3,559. Se dibuja el 1,31 medido y el resto queda en 2,25, 2 cm más que su medida.
- P3 no se mueve: sus 3,23 a la medianera Norte y 3,65 a la cara Norte de P5 lo llevarían 2 cm al Sur y 4 cm al Norte. Se dibujan 3,25 y 3,69. Medir de nuevo.
- Aire acondicionado: dos cassettes situados con las fotos del cliente, con panel estándar de 0,95 y rejilla de 0,90 × 0,50. Medir posición y tamaño reales.

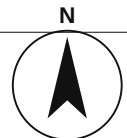

## ESCALA

1:50 (A3)

## FECHA

19 set. 2026

## PLANO

02 / 04

PROYECTO  
Reforma integral de local de hostelería

EMPLAZAMIENTO  
Local en planta baja y altílo  
Málaga

PLANO  
EQUIPAMIENTO

Barra y cocina · productos Makro

LEYENDA

- Bancada o mueble bajo
- Equipo refrigerado
- Encimera o tabla corrida
- Aparato (trazos: bajo encimera)
- Tabla de madera
- Muro de carga / medianera

HOLGURAS Y ALTURAS

|                                   |        |
|-----------------------------------|--------|
| Pasillo de cocina, mínimo         | 0,97 m |
| Paso de servicio en barra         | 1,05 m |
| Entrada a la cocina, bajo la viga | 1,37 m |
| Hueco libre de mesada en barra    | 0,75 m |
| Altura de encimera                | 0,90 m |
| Borde inferior de la campana      | 2,00 m |

NOTAS

Cada máquina es un producto real de makro.es con sus medidas de ficha; la web bloquea el acceso directo, así que las medidas vienen de su buscador. Confirmar en la ficha antes de comprar.


Cocción y campana metidas en el hundimiento de 0,275 de la medianera Norte, como pidió el cliente.

Mesada refrigerada de una sola pieza (2,54, la más larga de Makro) pegada al doblez de la L; 0,33 libres junto a la cocción. K6 bajo el escurridor de K7.

Pasillo de cocina de 0,97 a 1,11. Muro Oeste: 3,04 de aparatos en los 3,33 que hay hasta P1.


Trasbarra nueva del 19 set.: mesada corrida de 0,60 entre P1 y P2, con estante encima; la nevera A5 va bajo el hueco libre y nada bajo el fregadero A4.

Alturas por confirmar: A4 y A5 miden 0,85 y la encimera va a 0,90, con 5 cm de desnivel en A4 y 1-2 de holgura sobre A5. La altura libre que pide A3 para llenar la cuba no consta: medirla antes de colgar A6.

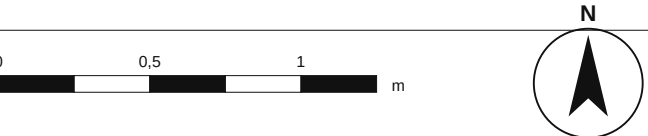


BARRA

trasbarra 2,75 entre P1 y P2 · mostrador 2,79 · paso de personal 0,95

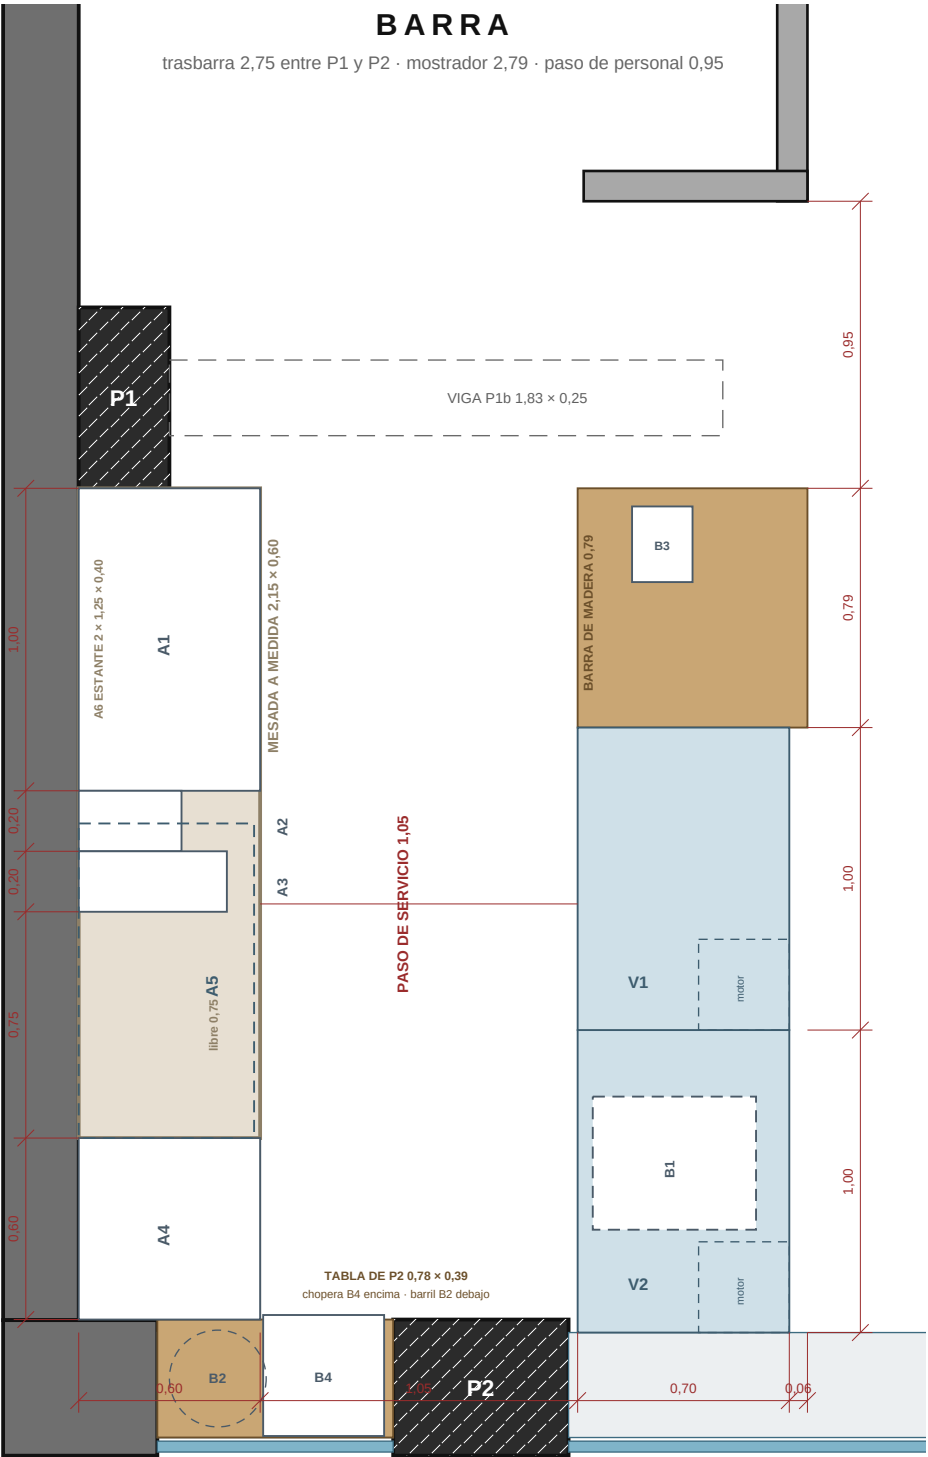

COCINA

2,31 × 3,20 m · hundimiento de 0,275 al Norte · entrada bajo la viga P1b

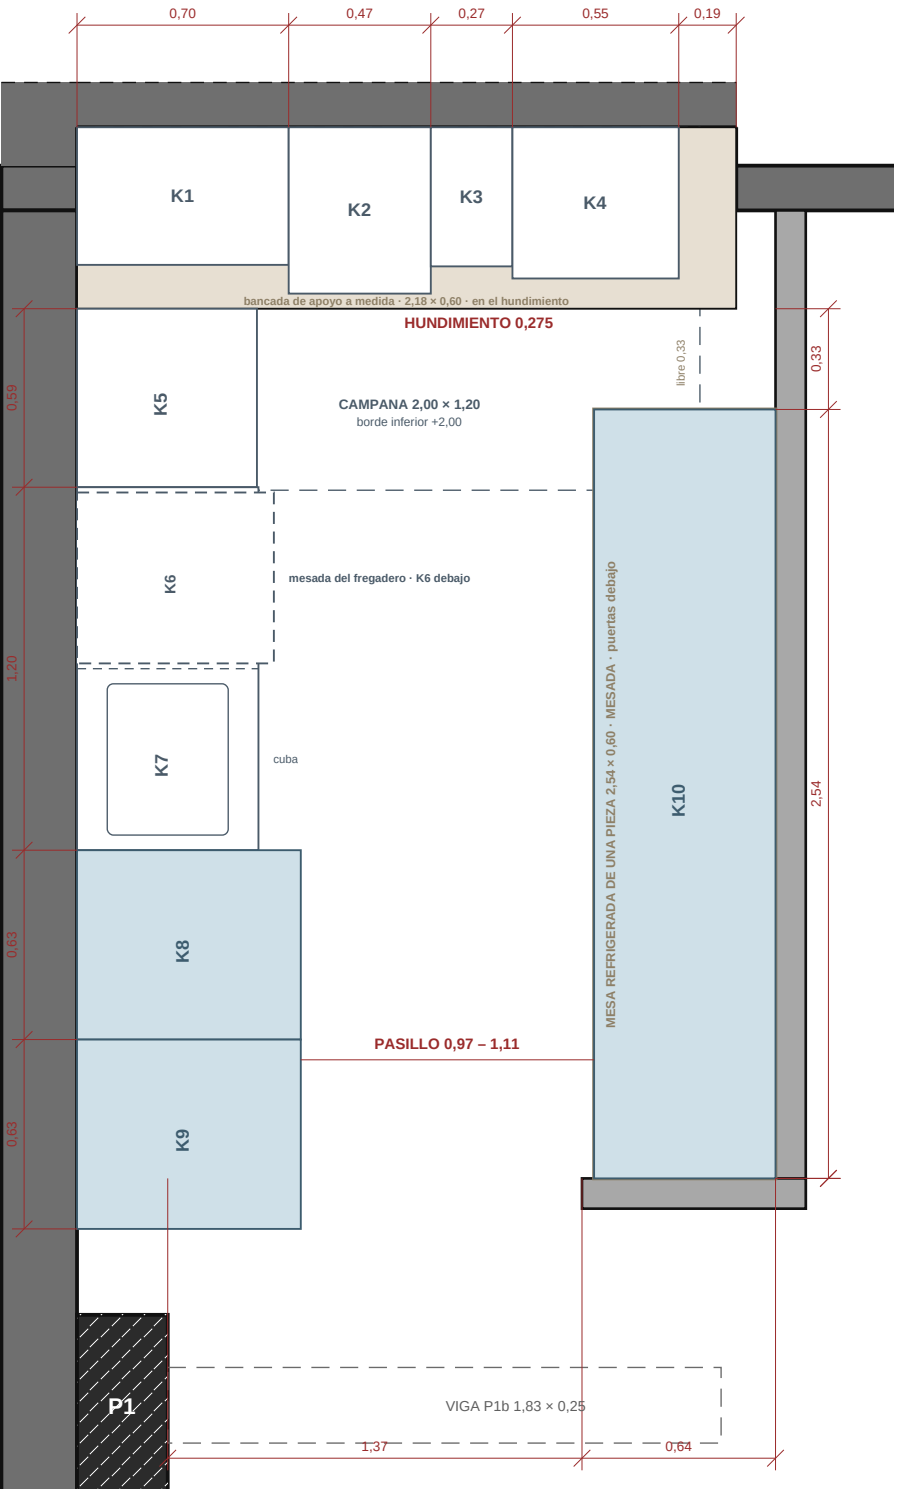

EQUIPAMIENTO · MAKRO

Ancho × fondo × alto en metros, de la ficha de makro.es. Vitrinas y cafetera ya compradas. Tablet y barriles con medida promedio. Enlaces en la lámina 04.

|     |                                                                                |                    |    |                                                                            |                    |
|-----|--------------------------------------------------------------------------------|--------------------|----|----------------------------------------------------------------------------|--------------------|
| K1  | Placa de inducción Bartscher, 2 zonas Ø230, 6 kW, 400 V                        | 0,70 × 0,46 × 0,12 | A2 | Molinillo de café Cunil TRANQUILO de ABC, 275 W, tolva 0,5 kg              | 0,17 × 0,34 × 0,41 |
| K2  | Cocedor de pasta eléctrico METRO Professional GNC1008, 8 L, 4 cestos           | 0,47 × 0,55 × 0,38 | A3 | Máquina de helado y crema fría Bras B-CREAM1HD, 6 L, italiana              | 0,20 × 0,49 × 0,62 |
| K3  | Freidora profesional 1 cuba de 7 L, eléctrica                                  | 0,27 × 0,46 × 0,37 | A4 | Fregadero de pie 1 seno con estante y bastidor, 600 × 600 × 850            | 0,60 × 0,60 × 0,85 |
| K4  | Plancha eléctrica Cleiton 50 cm, placa de 8 mm, sobremesa                      | 0,55 × 0,50 × 0,33 | A5 | Botellero frigorífico BTL1000, 2 puertas correderas, 240 L                 | 1,04 × 0,58 × 0,85 |
| KC  | Campana extractora industrial recta, sin turbina, AISI-304 satinado, 2 × 1,2 m | 2,00 × 1,20 × 0,50 | A6 | Estante mural cartelas compacto Fricosmos 011410, 1250 × 400 × 245         | 1,25 × 0,40 × 0,24 |
| K5  | Horno de convección eléctrico industrial, 4 bandejas 45 × 33                   | 0,59 × 0,59 × 0,57 | V2 | Vitrina refrigerada (comprada), 1,00 × 0,70; debajo, lavavasos             | 1,00 × 0,70 × 1,25 |
| K7  | Fregadero con bastidor con hueco lavavajillas, cuba izquierda, 1200 × 600      | 1,20 × 0,60 × 0,85 | V1 | Vitrina refrigerada (comprada), 1,00 × 0,70; hueco libre debajo            | 1,00 × 0,70 × 1,25 |
| K6  | Lavavajillas industrial ST500, cesta 50 × 50, bajo el escurridor de K7         | 0,56 × 0,65 × 0,86 | B1 | Lavavasos Elettrobar FAST 40, cesta 40 × 40 (bajo la vitrina V2)           | 0,44 × 0,54 × 0,67 |
| K8  | Armario refrigerado vertical Edenox APS-451 I, inox, 1 puerta, 395 L           | 0,63 × 0,74 × 1,86 | B2 | Barriles de cerveza de 30 L, Ø 0,32 (debajo de la tabla de P2)             | 0,32 × 0,32 × 0,60 |
| K9  | Armario refrigerado vertical Edenox APS-451 I, inox, 1 puerta, 395 L           | 0,63 × 0,74 × 1,86 | B3 | Caja: tablet sobre soporte (lo único que queda en el mostrador)            | 0,25 × 0,20 × 0,25 |
| K10 | Mesa refrigerada Infrico 4 puertas, AISI-304, peto 100 mm, -2/+8 °C, 530 L     | 2,54 × 0,60 × 0,85 | B4 | Columna de cerveza en T de 3 grifos, bandeja 40 × 40, sobre la tabla de P2 | 0,40 × 0,40 × 0,55 |
| A1  | Cafetera (comprada), 2 grupos                                                  | 1,00 × 0,60 × 0,50 |    |                                                                            |                    |

LISTA DE EQUIPAMIENTO · MAKRO

Todo lo que hay que comprar para la barra y la cocina, con la ficha de makro.es de cada producto. Medidas en metros, ancho × fondo × alto. Los enlaces de la última columna son clicables en el PDF.

EQUIPOS DIBUJADOS EN LAS LÁMINAS 01 Y 03

| RÓTULO | PRODUCTO                                                                       | MEDIDAS            | DÓNDE VA                                                                                 | FICHA EN MAKRO.ES                                                             |
|--------|--------------------------------------------------------------------------------|--------------------|------------------------------------------------------------------------------------------|-------------------------------------------------------------------------------|
| K1     | Placa de inducción Bartscher, 2 zonas Ø230, 6 kW, 400 V                        | 0,70 × 0,46 × 0,12 | Cocina · cocción, medianera Norte, bajo la campana, 1º desde el Oeste                    | https://www.makro.es/marketplace/product/623ef78b-af50-4e27-a2c5-b3a45089ba59 |
| K2     | Cocedor de pasta eléctrico METRO Professional GNC1008, 8 L, 4 cestos           | 0,47 × 0,55 × 0,38 | Cocina · cocción, bajo la campana, 2º                                                    | https://www.makro.es/marketplace/product/85f3fb44-3f09-463c-ab29-53822c8c1ce7 |
| K3     | Freidora profesional 1 cuba de 7 L, eléctrica                                  | 0,27 × 0,46 × 0,37 | Cocina · cocción, bajo la campana, 3º                                                    | https://www.makro.es/marketplace/product/57e9d9ed-d483-4f88-a049-5597b3a7ad18 |
| K4     | Plancha eléctrica Cleiton 50 cm, placa de 8 mm, sobremesa                      | 0,55 × 0,50 × 0,33 | Cocina · cocción, bajo la campana, 4º, contra la pared en L                              | https://www.makro.es/marketplace/product/acd212b2-73a4-42bc-bea7-329d5ab4771d |
| KC     | Campana extractora industrial recta, sin turbina, AISI-304 satinado, 2 × 1,2 m | 2,00 × 1,20 × 0,50 | Cocina · campana mural corrida sobre K1 a K4, borde inferior a +2,00                     | https://www.makro.es/marketplace/product/a8240770-cb5f-491b-926d-83b1e1e00a22 |
| K5     | Horno de convección eléctrico industrial, 4 bandejas 45 × 33                   | 0,59 × 0,59 × 0,57 | Cocina · muro Oeste, esquina Norte, sobre soporte                                        | https://www.makro.es/marketplace/product/e3c35b3b-14d3-4e2b-a109-373a863ddff9 |
| K7     | Fregadero con bastidor con hueco lavavajillas, cuba izquierda, 1200 × 600      | 1,20 × 0,60 × 0,85 | Cocina · muro Oeste, entre el horno y los frigoríficos; cuba al Sur, escurridor al Norte | https://www.makro.es/marketplace/product/c0cd57f0-35a2-485a-98f4-5dff628d84e  |
| K6     | Lavavajillas industrial ST500, cesta 50 × 50, bajo el escurridor de K7         | 0,56 × 0,65 × 0,86 | Cocina · muro Oeste, bajo el escurridor del fregadero K7 (hueco de lavavajillas)         | https://www.makro.es/marketplace/product/b6893f6e-6c55-499e-8e8b-4e246d107961 |
| K8     | Armario refrigerado vertical Edenox APS-451 I, inox, 1 puerta, 395 L           | 0,63 × 0,74 × 1,86 | Cocina · muro Oeste, vertical, al Sur del fregadero                                      | https://www.makro.es/marketplace/product/2e636462-1801-45f6-a3d8-15413909cb8c |
| K9     | Armario refrigerado vertical Edenox APS-451 I, inox, 1 puerta, 395 L           | 0,63 × 0,74 × 1,86 | Cocina · muro Oeste, vertical, contra P1                                                 | https://www.makro.es/marketplace/product/2e636462-1801-45f6-a3d8-15413909cb8c |
| K10    | Mesa refrigerada Infrico 4 puertas, AISI-304, peto 100 mm, -2/+8 °C, 530 L     | 2,54 × 0,60 × 0,85 | Cocina · pared en L, de una pieza, pegada al doblez; 0,33 libres junto a la cocción      | https://www.makro.es/marketplace/product/764bc52f-1287-4e08-89dc-c2e453dfea49 |
| A1     | Cafetera (comprada), 2 grupos                                                  | 1,00 × 0,60 × 0,50 | Barra · trasbarra, sobre la mesada, pegada a P1 (extremo Norte)                          | ya comprado / medida promedio, sin ficha                                      |
| A2     | Molinillo de café Cunil TRANQUILO de ABC, 275 W, tolva 0,5 kg                  | 0,17 × 0,34 × 0,41 | Barra · trasbarra, en el hueco de 0,20 a la derecha de la cafetera                       | https://www.makro.es/marketplace/product/f2df0f65-b185-40b2-b2e2-2cd42fb2eefd |
| A3     | Máquina de helado y crema fría Bras B-CREAM1HD, 6 L, italiana                  | 0,20 × 0,49 × 0,62 | Barra · trasbarra, sobre la mesada, a la derecha del molinillo                           | https://www.makro.es/marketplace/product/e4ddc7ec-739d-4b14-968b-1d230076b476 |
| A4     | Fregadero de pie 1 seno con estante y bastidor, 600 × 600 × 850                | 0,60 × 0,60 × 0,85 | Barra · trasbarra, de pie contra P2 (extremo Sur); sustituye ese tramo de mesada         | https://www.makro.es/marketplace/product/31bf0e3c-d322-4e34-a968-9bd9ace2024d |
| A5     | Botellero frigorífico BTL1000, 2 puertas correderas, 240 L                     | 1,04 × 0,58 × 0,85 | Barra · trasbarra, debajo de la mesada, bajo el hueco libre                              | https://www.makro.es/marketplace/product/77c7b69b-09e0-4c28-878e-9454ffff60ec |
| A6     | Estante mural cartelas compacto Fricosmos 011410, 1250 × 400 × 245             | 1,25 × 0,40 × 0,24 | Barra · trasbarra, estante mural sobre la mesada (2 piezas, 2,50 en total)               | https://www.makro.es/marketplace/product/8af91e42-ebf3-4239-8e01-9b6b82b73120 |
| V2     | Vitrina refrigerada (comprada), 1,00 × 0,70; debajo, lavavasos                 | 1,00 × 0,70 × 1,25 | Barra · mostrador delantero, junto al zócalo del ventanal (Sur); lavavasos debajo        | ya comprado / medida promedio, sin ficha                                      |
| V1     | Vitrina refrigerada (comprada), 1,00 × 0,70; hueco libre debajo                | 1,00 × 0,70 × 1,25 | Barra · mostrador delantero, al Norte de V2                                              | ya comprado / medida promedio, sin ficha                                      |
| B1     | Lavavasos Elettrobar FAST 40, cesta 40 × 40 (bajo la vitrina V2)               | 0,44 × 0,54 × 0,67 | Barra · bajo la vitrina V2                                                               | https://www.makro.es/marketplace/product/e858e346-8373-4e64-aa03-6f9a559e168e |
| B2     | Barriles de cerveza de 30 L, Ø 0,32 (debajo de la tabla de P2)                 | 0,32 × 0,32 × 0,60 | Barra · debajo de la tabla de P2                                                         | ya comprado / medida promedio, sin ficha                                      |
| B3     | Caja: tablet sobre soporte (lo único que queda en el mostrador)                | 0,25 × 0,20 × 0,25 | Barra · barra de madera del mostrador (única cosa que queda en ella)                     | ya comprado / medida promedio, sin ficha                                      |
| B4     | Columna de cerveza en T de 3 grifos, bandeja 40 × 40, sobre la tabla de P2     | 0,40 × 0,40 × 0,55 | Barra · encima de la tabla de P2                                                         | https://www.makro.es/marketplace/product/f2d9d7ba-6f4f-4feb-b032-641cc4d828fe |

ALTERNATIVAS CON LA MISMA FUNCIÓN · no dibujadas

| SUSTITUYE | PRODUCTO                                                                        | MEDIDAS            | DÓNDE VA                                                                        | FICHA EN MAKRO.ES                                                             |
|-----------|---------------------------------------------------------------------------------|--------------------|---------------------------------------------------------------------------------|-------------------------------------------------------------------------------|
| K10       | Mesa refrigerada Vaiotec EASYLINE, inox, 4 puertas, GN 1/1, 553 L               | 2,23 × 0,70 × 0,85 | Cocina · pared en L, en lugar de K10, pegada al doblez; fondo 0,70; 0,73 libres | https://www.makro.es/marketplace/product/230e627d-7291-43e0-a2b4-ebbf6e783f27 |
| K10       | METRO Professional GCC3100, inox, 3 puertas, 334 L (la de la foto, refrigerada) | 1,79 × 0,70 × 0,85 | Cocina · pared en L, en lugar de K10, pegada al doblez; deja 1,16 libres        | https://www.makro.es/marketplace/product/176b30f1-81b0-4a52-916e-80722d9a9240 |
| K6        | Lavavajillas Eurast 50 × 50, 575 × 600 × 820: cabe seguro bajo el escurridor    | 0,57 × 0,60 × 0,82 | Cocina · en lugar de K6 si el ST500 no entra bajo el escurridor (0,82 de alto)  | https://www.makro.es/marketplace/product/1acedc0e-199c-449c-b390-a8626c771613 |
| K8/K9     | Armario frigorífico ventilado 400 L, acero inoxidable (Diamond)                 | 0,63 × 0,74 × 1,93 | Cocina · muro Oeste, en lugar de K8 y K9; misma huella que el Edenox            | https://www.makro.es/marketplace/product/8969b667-b5cb-4e83-b599-3dd45c112547 |
| K8/K9     | Armario refrigerado AR400L Clima Hostelería, lacado blanco (no inox), 360 L     | 0,60 × 0,61 × 1,87 | Cocina · muro Oeste, en lugar de K8 y K9 (0,60 de ancho, lacado blanco)         | https://www.makro.es/marketplace/product/d48c3c0c-7975-4c22-89c7-64676c23681f |
| A3        | Granizadora GRANICREAM 1S Eurofred, 1 cuba de 10 L, cremas de café              | 0,20 × 0,50 × 0,79 | Barra · alternativa a A3: misma anchura, 10 L, pero 0,79 de alto                | https://www.makro.es/marketplace/product/e826e334-3cba-44fc-a530-627af1dabaf6 |
| A3        | Granizadora GRANISMART 5x1 Eurofred, 1 cuba de 5 L (la más baja)                | 0,26 × 0,40 × 0,63 | Barra · alternativa a A3: cuba de 5 L, 0,26 de ancho y solo 0,40 de fondo       | https://www.makro.es/marketplace/product/635e0924-0d3e-42ca-965e-e66eb41cdee1 |
| A6        | Estante en inox de pared, 2000 × 400 × 250, de una sola pieza                   | 2,00 × 0,40 × 0,25 | Barra · alternativa a A6: una sola pieza de 2,00 en vez de dos de 1,25          | https://www.makro.es/marketplace/product/15f4f100-83b5-4f51-a383-11acf9989372 |
| A4        | Fregadero 1 cubeta con puerta, Gama 600 Distform, 600 × 600 × 850               | 0,60 × 0,60 × 0,85 | Barra · alternativa al fregadero A4, con puerta (mismo hueco)                   | https://www.makro.es/marketplace/product/3efac5b4-e702-4af6-9dd9-533709488190 |
| A4        | Fregadero industrial 1 cuba AISI-304, 700 × 600 × 850                           | 0,70 × 0,60 × 0,85 | Barra · alternativa al fregadero A4 en AISI-304, 0,10 más ancho                 | https://www.makro.es/marketplace/product/95121b55-b486-4a76-a3de-ed7874e75876 |
| A5        | Botellero inox interior y exterior, 2 puertas, 200 L, Eurast                    | 1,02 × 0,55 × 0,85 | Barra · alternativa a la nevera A5 (1,02, inox interior y exterior)             | https://www.makro.es/marketplace/product/a046bf7e-9d25-4304-9593-1cd32668e47f |
| A5        | Botellero refrigerado de bar Yostin, 2 puertas, 100 cm, AISI-304                | 1,00 × 0,55 × 0,84 | Barra · alternativa a la nevera A5 (1,00 exactos, fabricación nacional)         | https://www.makro.es/marketplace/product/6589602e-de66-484c-871f-68f83b182638 |

SIN SITIO EN LA TRASBARRA NUEVA · decidir dónde van

| ERA | PRODUCTO                                                       | MEDIDAS            | DÓNDE VA                                                            | FICHA EN MAKRO.ES                                                             |
|-----|----------------------------------------------------------------|--------------------|---------------------------------------------------------------------|-------------------------------------------------------------------------------|
| A3  | Fabricador de hielo Gastro M CT694, 28 kg/24 h (bajo encimera) | 0,40 × 0,46 × 0,67 | Sin sitio en la trasbarra nueva: decidir dónde va                   | https://www.makro.es/marketplace/product/e3db53e1-8f64-4495-bb2c-59fe355a32e2 |
| A4  | Exprimidor de naranjas Mizumo Next Gen                         | 0,48 × 0,35 × 0,73 | Sin sitio en la trasbarra nueva: cabría en el hueco libre de mesada | https://www.makro.es/marketplace/product/a7c3e878-0cdd-4f7e-b013-897ae4f6120d |
| A2  | Lavamanos inox con grifo y pulsador de pedal, cuba Ø340        | 0,40 × 0,40 × 0,85 | Sin sitio: lo sustituye el fregadero A4, pegado a P2                | https://www.makro.es/marketplace/product/6105678f-3159-4172-a17a-f400760f0b35 |
| A3b | Licudadora industrial Sammic Li-240                            | 0,20 × 0,31 × 0,36 | Sin sitio en la trasbarra nueva: decidir dónde va                   | https://www.makro.es/marketplace/product/2b8d9850-b422-4738-b716-c30da9857300 |

A MEDIDA · no se compran en Makro

- Bancada de apoyo de la línea de cocción, dentro del hundimiento: 2,18 × 0,60, acero inoxidable.
- Mesada de la trasbarra, de P1 al fregadero A4: 2,15 × 0,60 (el fregadero A4, de pie, hace los otros 0,60).
- Hueco de 0,20 para el molinillo A2 y los utensilios, a la derecha de la cafetera.
- Barra de madera del mostrador delantero: 0,79 × 0,76.
- Tabla de P2 al muro: 0,78 × 0,39 (chopera B4 encima, barril B2 debajo).
- Mostrador delantero: 2,79 × 0,76 de fondo, del zócalo del ventanal a P1.

VERIFICACIÓN DE LOS ENLACES

makro.es responde 403 a cualquier acceso desde un servidor, así que las fichas no se pueden abrir desde el entorno de trabajo. Cada enlace se verificó buscando su identificador con el buscador restringido a makro.es: todos devuelven su URL con el título del producto (LISTA\_MAKRO.md). La del fregadero K7 la facilitó el cliente. Confirmar precio y stock.

GRUPO SUMA

Reformas y proyectos · Málaga

PROYECTO

Reforma integral de local de hostelería

EMPLAZAMIENTO

Local en planta baja y altílo  
Málaga

PLANO

EQUIPAMIENTO

Lista de compra · enlaces a makro.es

RESUMEN

|                             |                       |
|-----------------------------|-----------------------|
| Fichas distintas de Makro   | 17                    |
| Unidades a comprar en Makro | 18                    |
| Ya comprado                 | cafetera y 2 vitrinas |
| Medida promedio             | barriles y tablet     |
| A medida                    | 6 elementos           |

NOTAS

Medidas ancho × fondo × alto en metros, tomadas de la ficha de makro.es.

Los enlaces de la última columna son clicables en el PDF; en papel, copiar la dirección o buscar el título en makro.es.

Vitrinas y cafetera ya compradas, con las medidas del cliente. Barriles y tablet con medida promedio.

Confirmar precio y stock antes de comprar.

|            |              |         |
|------------|--------------|---------|
| ESCALA     | FECHA        | PLANO   |
| sin escala | 19 set. 2026 | 04 / 04 |