

GRUPO SUMA

Reformas y proyectos · Málaga

PROYECTO

Reforma integral de local de hostelería

EMPLAZAMIENTO

Local en planta baja y altillo
Málaga

PLANO

PLANTA ALTA

Altillo +3,00 · estructura

LEYENDA

- Muro de carga / medianera
- Pilar o machón de hormigón
- Tabiquería
- Barandilla de vidrio
- Vacío sobre planta baja

SUPERFICIES Y ALTURAS

Forjado de planta alta	33,74 m²
Altillo diáfano	26,17 m²
Aseo (lavabo + inodoro)	3,92 m²
Almacén	2,59 m²
Altura libre de planta alta	2,50 m

PILARES Y MACHONES (secciones en m)

P1 Machón del muro Oeste	0,37 × 0,60
P2 Pilastra del muro Sur	0,60 × 0,30
P3 Pilar central	0,60 × 0,90
P4 Machón de la medianera Este	0,20 × 0,60
P5 Pilar de fachada	0,50 × 0,96


NOTAS

Cotas en metros, tomadas sobre el levantamiento.

Plano de estructura: no se representa mobiliario ni equipamiento.


El forjado del altillo no cubre todo el local: la franja sur y oeste es un vacío a doble altura.

Sección horizontal a 1,20 m sobre el forjado (+4,20).

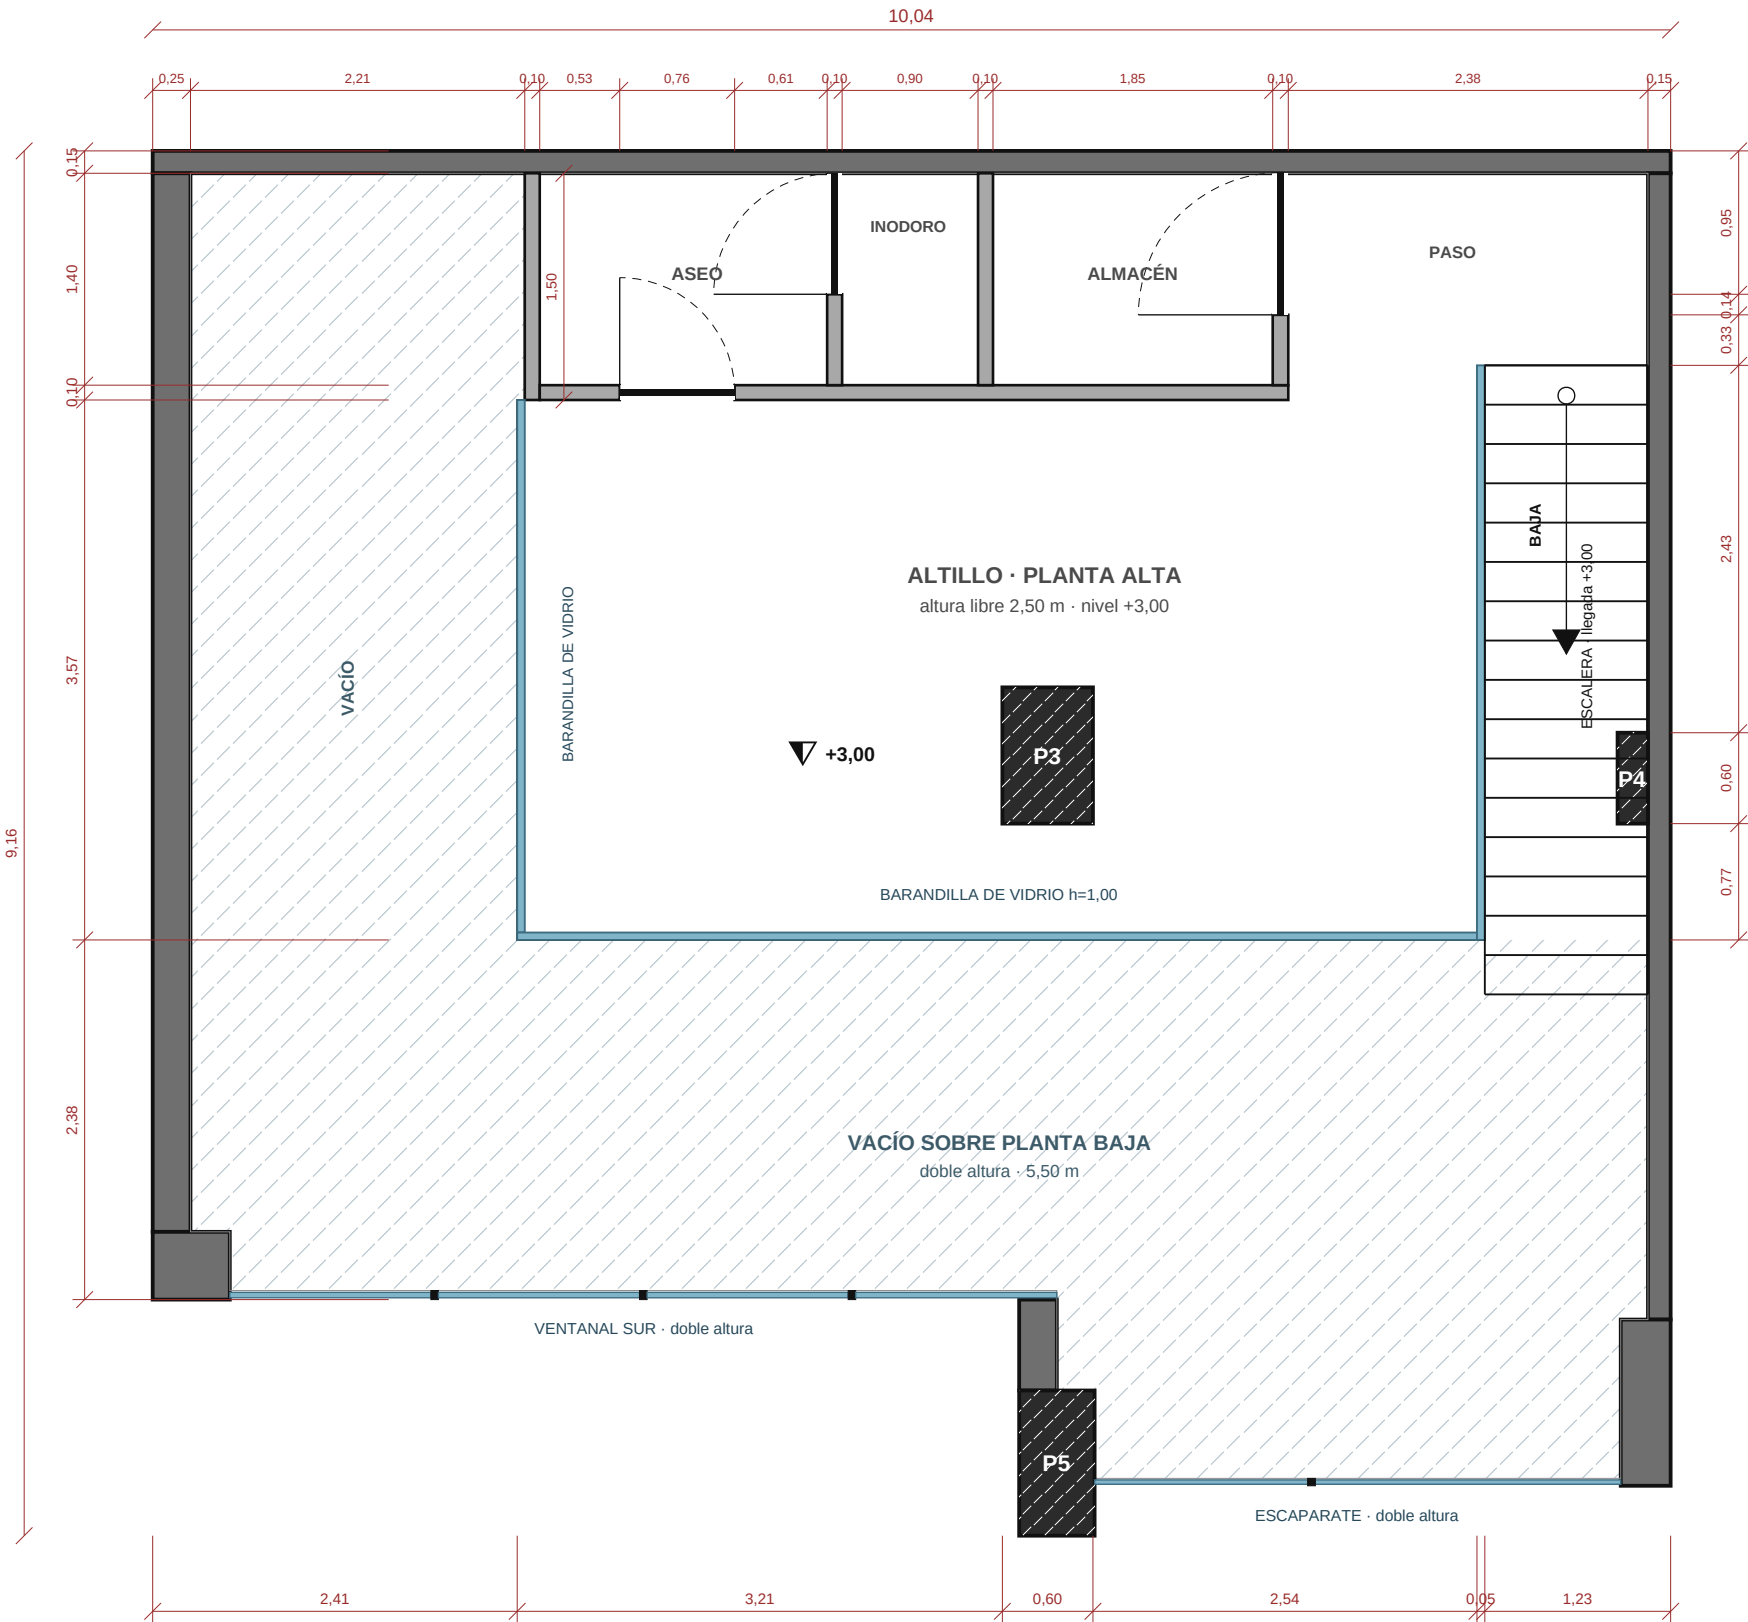

COMPROBAR EN OBRA Puntos en los que los vídeos del local no cuadran con el levantamiento, o que el levantamiento no recoge. Se dibuja el levantamiento por ser la única fuente acotada.

- Retranqueo de 1,23 m entre el ventanal sur (y=1,561) y el escaparate (y=0,330): en obra los dos vidrios parecen casi coplanarios. Medir el fondo del pilar P5.
- Frente real a la calle. El levantamiento da 10,04 m entre medianeras; el acristalamiento visible en obra es sensiblemente menor.
- Puerta de acceso: no figura en el levantamiento. En obra hay una hoja practicable en el escaparate. Situarla y acotarla.
- Chapados de piedra: jamba oscura al oeste, pilastra de arenisca sobre P5 y revestimiento del pilar de esquina. Espesores sin medir.
- Coronación del acristalamiento (≈4,70) y travesaño del ventanal (≈2,30). Solo el nivel +3,00 está acotado en el levantamiento.
- Puntos de luz: en el techo hay más de 20 taladros en retícula de 1,2-1,5 m. El plano recoge los 13 del proyecto de reforma.
- Puerta del aseo: en obra parece situada hacia x=3,9-4,5; el levantamiento la coloca entre 3,09 y 3,85.
- Machones trasdosados con placa de yeso nueva: la sección de hormigón no es verificable a la vista.

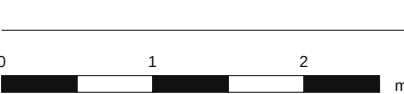

ESCALA

1:50 (A3)

FECHA

12 set. 2026

PLANO

02 / 02