

GRUPO SUMA

Reformas y proyectos · Málaga

PROYECTO

Reforma integral de local de hostelería

EMPLAZAMIENTO

Local en planta baja y attillo
Málaga

PLANO

PLANTA BAJA

Estado actual · estructura

LEYENDA

- Muro de carga / medianera
- Pilar o machón de hormigón
- Carpintería acristalada
- Espacio de doble altura
- Forjado y viga sobre el corte
- Punto de luz s/ proyecto

SUPERFICIES Y ALTURAS

Planta baja, dentro de muros	75,63 m²
Zona de doble altura	37,80 m²
Altura libre bajo forjado	2,70 m
Altura en doble altura	5,50 m
Acristalamiento de fachada	≈ 4,70 m

PILARES Y MACHONES (secciones en m)

P1 Machón del muro Oeste	0,37 × 0,60
P2 Pilastra del muro Sur	0,60 × 0,30
P3 Pilar central	0,60 × 0,90
P4 Machón de la medianera Este	0,20 × 0,60
P5 Pilar de fachada	0,50 × 0,96


NOTAS

Cotas en metros, tomadas sobre el levantamiento.

Plano de estructura: no se representa mobiliario ni equipamiento. Cota de referencia ±0,00 en el pavimento de planta baja.



Sección horizontal a 1,20 m sobre el pavimento.

Los puntos de luz proceden del proyecto de reforma, no están replanteados en obra.

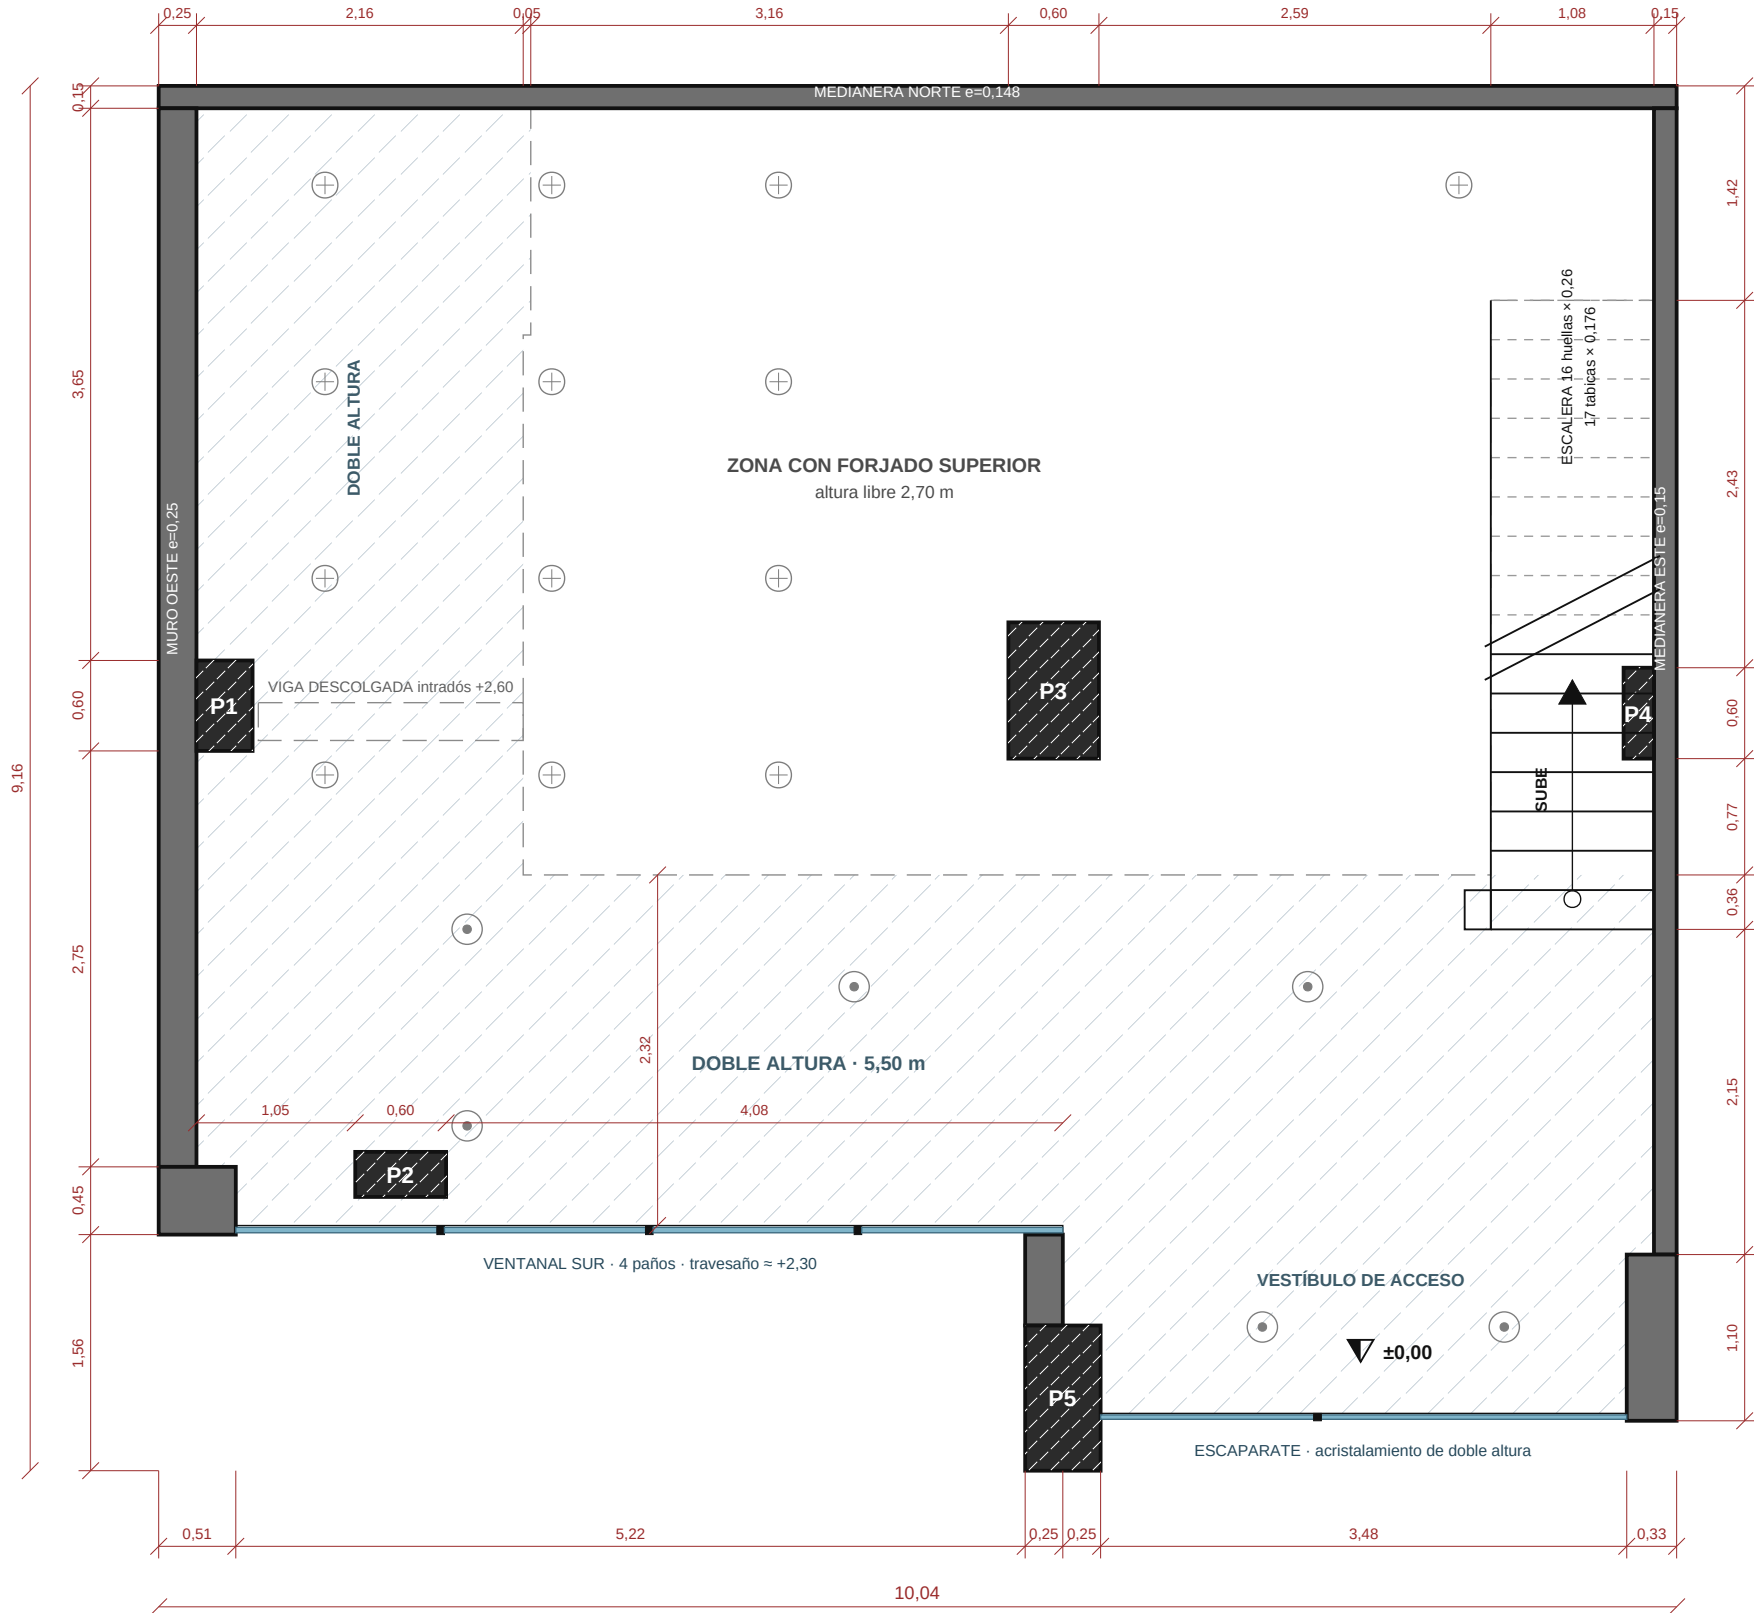

COMPROBAR EN OBRA Puntos en los que los vídeos del local no cuadran con el levantamiento, o que el levantamiento no recoge. Se dibuja el levantamiento por ser la única fuente acotada.

- Retranqueo de 1,23 m entre el ventanal sur (y=1,561) y el escaparate (y=0,330): en obra los dos vidrios parecen casi coplanarios. Medir el fondo del pilar P5.
- Frente real a la calle. El levantamiento da 10,04 m entre medianeras; el acristalamiento visible en obra es sensiblemente menor.
- Puerta de acceso: no figura en el levantamiento. En obra hay una hoja practicable en el escaparate. Situarla y acotarla.
- Chapados de piedra: jamba oscura al oeste, pilastra de arenisca sobre P5 y revestimiento del pilar de esquina. Espesores sin medir.
- Coronación del acristalamiento (≈4,70) y travesaño del ventanal (≈2,30). Solo el nivel +3,00 está acotado en el levantamiento.
- Puntos de luz: en el techo hay más de 20 taladros en retícula de 1,2-1,5 m. El plano recoge los 13 del proyecto de reforma.
- Puerta del aseo: en obra parece situada hacia x=3,9-4,5; el levantamiento la coloca entre 3,09 y 3,85.
- Machones trasdosados con placa de yeso nueva: la sección de hormigón no es verificable a la vista.

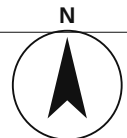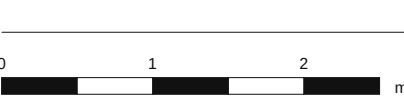

ESCALA

1:50 (A3)

FECHA

12 set. 2026

PLANO

01 / 02