

Reforma integral de local de hostelería

Local en planta baja y altillo
Málaga

PLANTA BAJA

Estado actual · estructura

- Muro de carga / medianera
- Pilar o machón de hormigón
- Pared en L nueva (apoyo del vidrio)
- Carpintería acristalada
- Espacio de doble altura
- Forjado sobre el corte
- Reserva de espacio del cliente
- Mesas dobles de 0,70 x 0,70 y sillas
- Nevera de bebidas A7 (cara Sur de P3)
- Recorrido de sala · 0,74 por el Norte
- Punto de luz s/ proyecto original
- Aire acondicionado (cassette de techo)

Planta baja, dentro de muros	76,23 m ²
Zona de doble altura	38,40 m ²
Suelo a suelo, medido en obra	2,56 m
Altura libre bajo forjado	2,56 – canto
Pared en L, altura	1,22 m
Mesas dobles / plazas sentadas	8 / 20
Acristalamiento de fachada	≈ 4,70 m

P1 Machón del muro Oeste	0,30 × 0,60
P2 Pilastra del muro Sur	0,58 × 0,45
P3 Pilar central	0,65 × 1,07
P4 Machón de la medianera Este	0,20 × 0,60
P5 Pilar de fachada	0,60 × 1,00

Cotas en metros. Hundimiento, pared en L, P3, barra, zócalo y puerta con las medidas del 19 set.; el resto, del levantamiento. Sección a 1,20 m sobre el pavimento. Mesas dobles de 0,70 x 0,70 que el personal junta para formar mesas de cuatro. M4 pegada a P3. El sillón, con 0,60 de fondo: falta medirlo y el trasdosado de 0,10. Luces del proyecto original; los cassettes de aire, de las fotos del cliente.


La nevera A7 sale 0,58 de la cara Sur de P3 y deja 0,45 hasta las sillas de M2: por ahí ya no se pasa y el paso a la barra da la vuelta por el Norte, con 0,74. En la cara Este de P3 serían 1,04. Baño no accesible: 0,70.



1:50 (A3)

19 set. 2026

01 / 04

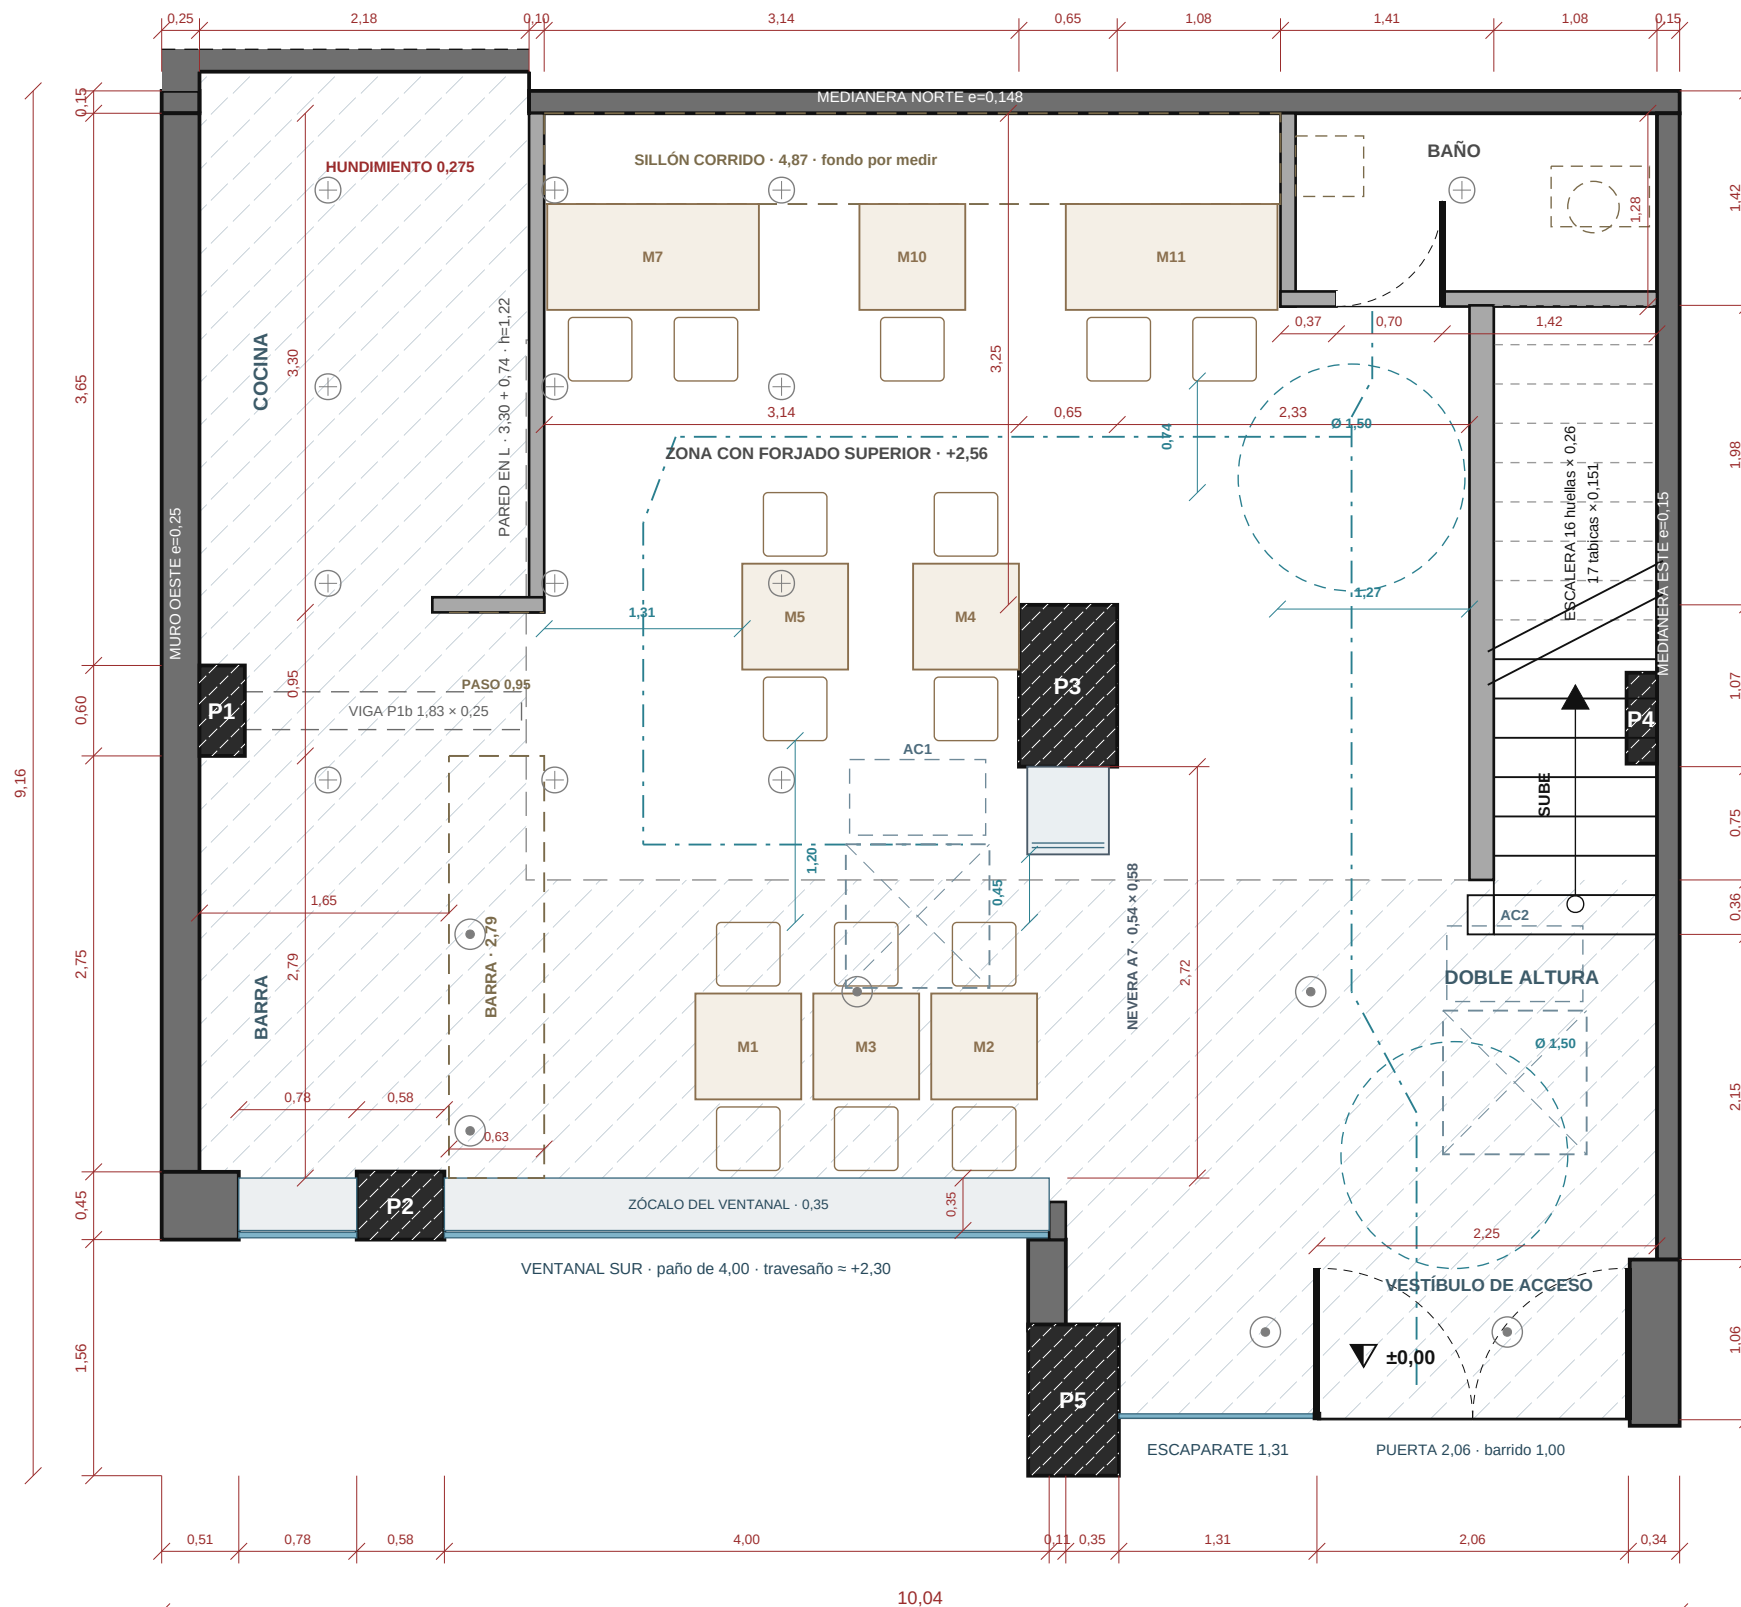

1 Hundimiento de la medianera Norte: 0,275 de fondo en los 2,18 de la cocina. Supera el espesor dibujado (0,148): medir ese cerramiento y lo que hay detrás.

2 Canto del forjado del altillo. Con 2,56 m de suelo a suelo, la altura libre de planta baja es 2,56 menos ese canto, no los 2,70 supuestos.

3 P1b se dibuja como viga ($1,83 \times 0,25$) y no como pilar: si fuera macizo hasta el suelo, la cocina no tendría entrada. Medir su intradós.

4 Zócalo del ventanal: 0,347 desde el vidrio, deducido de los 2,72 de P3 a su cara interior; sobresale 0,16 del muro del ventanal (0,25). Medirlo directamente.

5 Cadena Este-Oeste del cliente (2,18 + 3,01 + 0,65 + 2,33): cierra contra la escalera con 0,13 de pared entre el hundimiento y la L y 0,16 de cerramiento.

6 La pared en L queda 0,10 al Este del borde del forjado del levantamiento: el vidrio de 1,35 sobre ella (2,57 en total) no pasa bajo el altillo. Medir ese borde.

7 Vestíbulo: los 1,31 y 2,23 del cliente suman 3,54 y de P5 al muro Este hay 3,559. Se dibuja el 1,31 medido y el resto queda en 2,25, 2 cm más que su medida.

8 P3 no se mueve: sus 3,23 a la medianera Norte y 3,65 a la cara Norte de P5 lo llevarían 2 cm al Sur y 4 cm al Norte. Se dibujan 3,25 y 3,69. Medir de nuevo.

9 Aire acondicionado: dos cassettes situados con las fotos del cliente, con panel estándar de 0,95 y rejilla de 0,90 × 0,50. Medir posición y tamaño reales.

GRUPO SUMA

Reformas y proyectos · Málaga

PROYECTO

Reforma integral de local de hostelería

EMPLAZAMIENTO

Local en planta baja y altílo
Málaga

PLANO

PLANTA ALTA

Altílo +2,56 · estructura

LEYENDA

- Muro de carga / medianera
- Pilar o machón de hormigón
- Tabiquería
- Barandilla de vidrio
- Mesas y sillas (medidas promedio)
- Paso libre entre mobiliario (m)
- Vacío sobre planta baja

SUPERFICIES Y ALTURAS


Forjado de planta alta	33,74 m²
Altílo diáfano	26,17 m²
Aseo (lavabo + inodoro)	3,92 m²
Almacén	2,59 m²
Nivel del forjado, medido	+2,56 m
Puestos de cowork	14

PILARES Y MACHONES (secciones en m)

P1 Machón del muro Oeste	0,30 × 0,60
P2 Pilastra del muro Sur	0,58 × 0,45
P3 Pilar central	0,65 × 1,07
P4 Machón de la medianera Este	0,20 × 0,60
P5 Pilar de fachada	0,60 × 1,00


NOTAS

Cotas en metros, tomadas sobre el levantamiento.
Nivel del forjado +2,56, medido en obra.
El forjado del altílo no cubre todo el local: la franja sur y oeste es un vacío a doble altura.
Mesa de cowork 2,40 × 1,00 para 8 puestos y una redonda de Ø 1,20 con 6 sillas. Medidas promedio.
Pasos libres entre mobiliario acotados en azul:
1,01 hacia el aseo y el almacén; 1,30 en el desembarco; 0,26 a 0,85 en los accesos a las sillas.

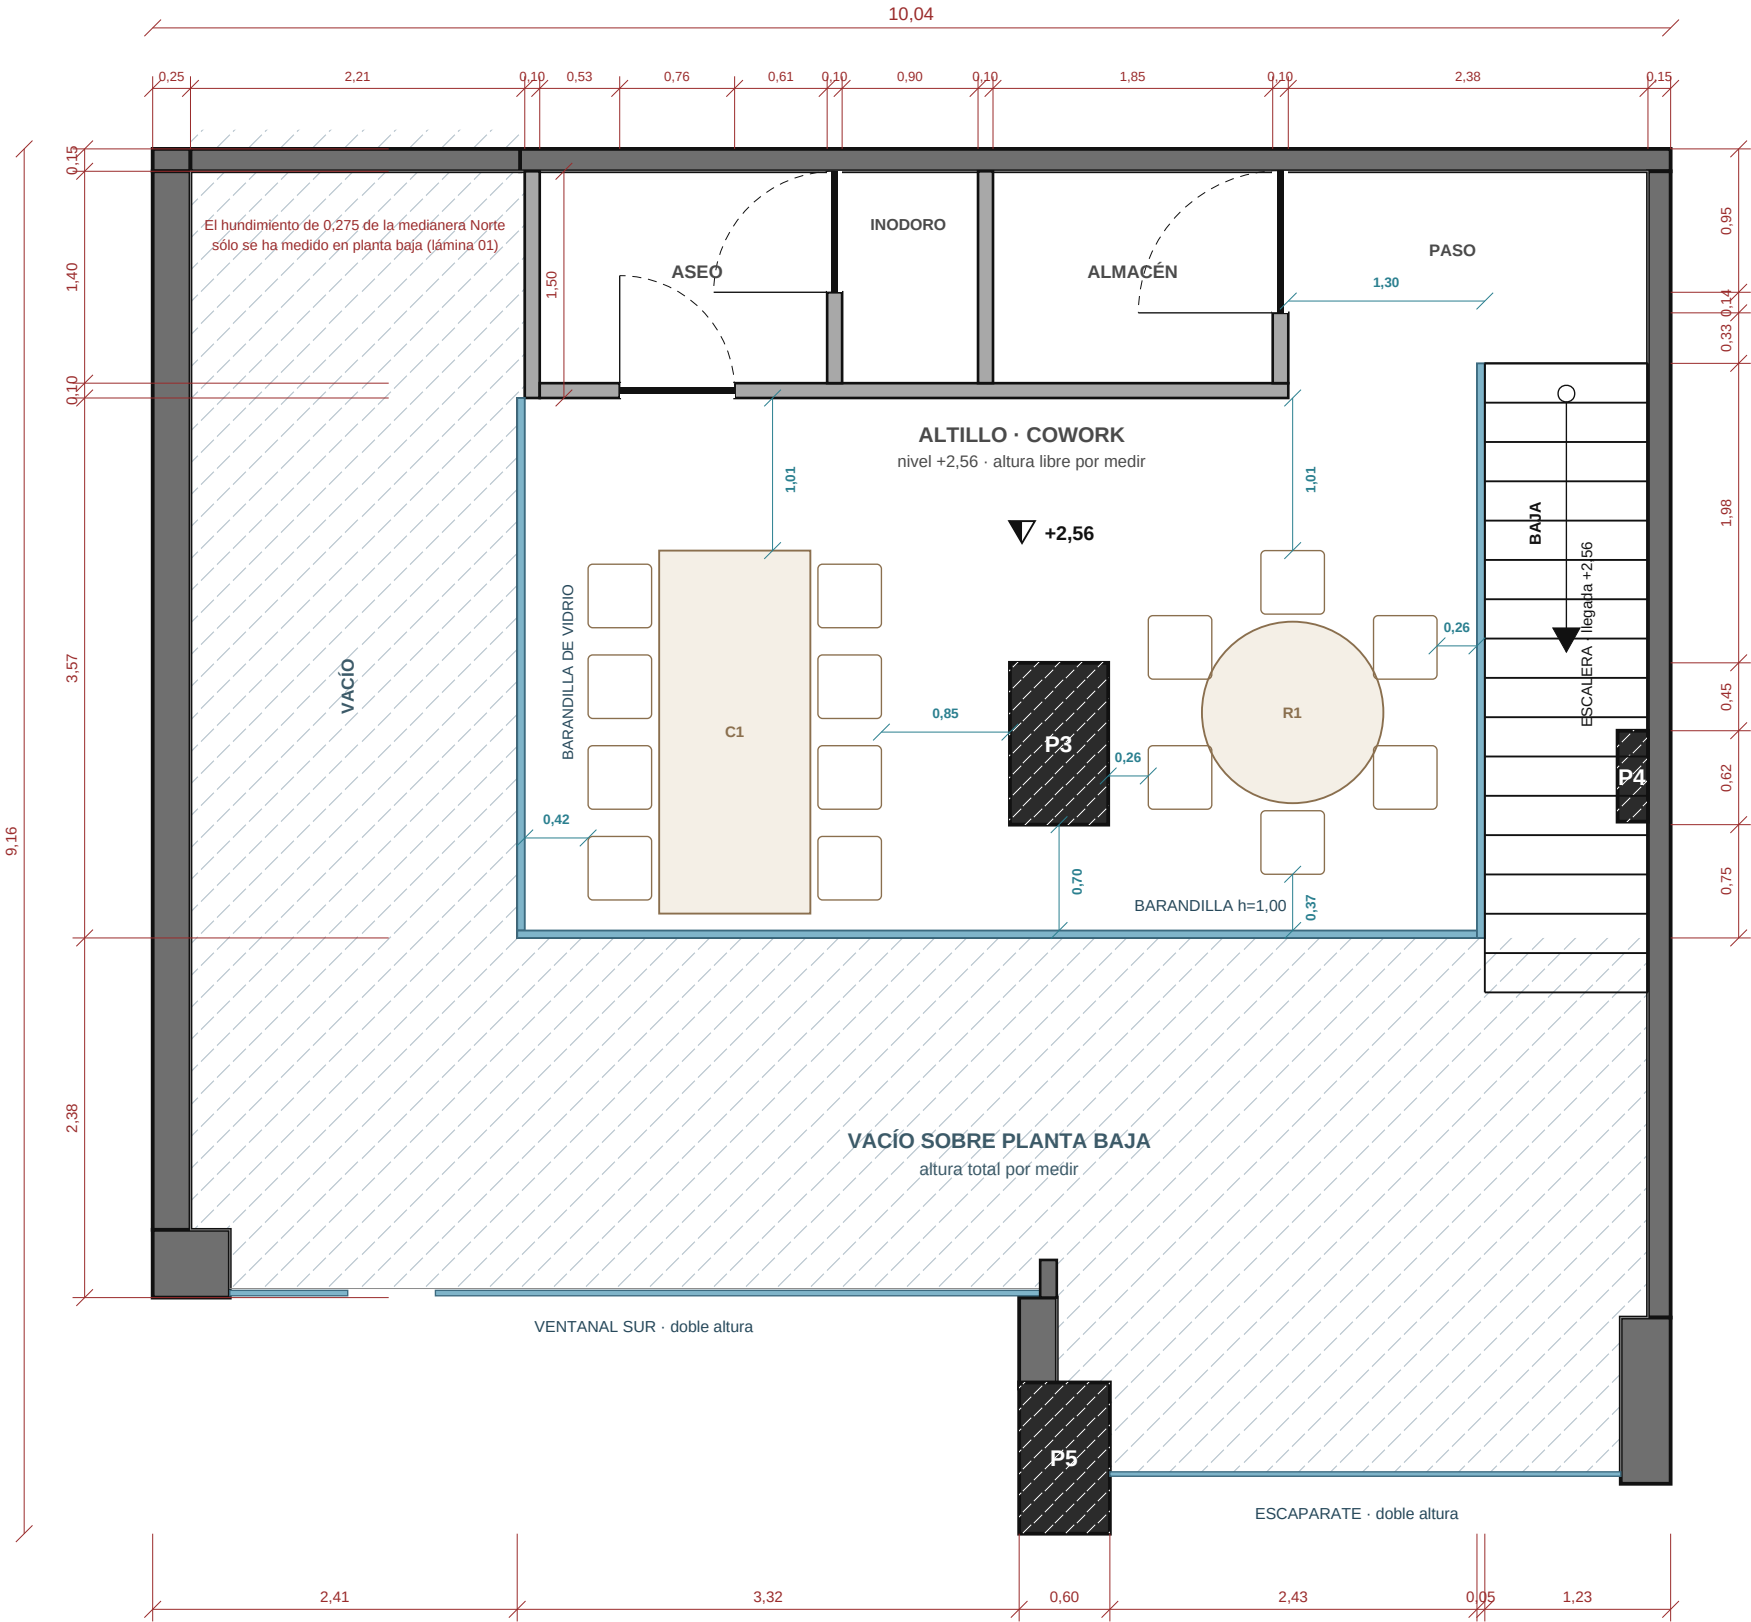

COMPROBAR EN OBRA Puntos en los que los vídeos del local no cuadran con el levantamiento, o que el levantamiento no recoge. Se dibuja el levantamiento por ser la única fuente acotada.

- Hundimiento de la medianera Norte: 0,275 de fondo en los 2,18 de la cocina. Supera el espesor dibujado (0,148): medir ese cerramiento y lo que hay detrás.
- Canto del forjado del altílo. Con 2,56 m de suelo a suelo, la altura libre de planta baja es 2,56 menos ese canto, no los 2,70 supuestos.
- P1b se dibuja como viga (1,83 × 0,25) y no como pilar: si fuera macizo hasta el suelo, la cocina no tendría entrada. Medir su intradós.
- Zócalo del ventanal: 0,347 desde el vidrio, deducido de los 2,72 de P3 a su cara interior; sobresale 0,16 del muro del ventanal (0,25). Medirlo directamente.
- Cadena Este-Oeste del cliente (2,18 + 3,01 + 0,65 + 2,33): cierra contra la escalera con 0,13 de pared entre el hundimiento y la L y 0,16 de cerramiento.
- La pared en L queda 0,10 al Este del borde del forjado del levantamiento: el vidrio de 1,35 sobre ella (2,57 en total) no pasa bajo el altílo. Medir ese borde.
- Vestíbulo: los 1,31 y 2,23 del cliente suman 3,54 y de P5 al muro Este hay 3,559. Se dibuja el 1,31 medido y el resto queda en 2,25, 2 cm más que su medida.
- P3 no se mueve: sus 3,23 a la medianera Norte y 3,65 a la cara Norte de P5 lo llevarían 2 cm al Sur y 4 cm al Norte. Se dibujan 3,25 y 3,69. Medir de nuevo.
- Aire acondicionado: dos cassettes situados con las fotos del cliente, con panel estándar de 0,95 y rejilla de 0,90 × 0,50. Medir posición y tamaño reales.

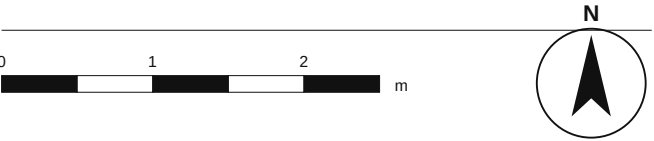

ESCALA	FECHA	PLANO
1:50 (A3)	19 set. 2026	02 / 04

GRUPO SUMA

Reformas y proyectos · Málaga

PROYECTO

Reforma integral de local de hostelería

EMPLAZAMIENTO

Local en planta baja y altílo Málaga

PLANO

EQUIPAMIENTO

Barra y cocina · productos Makro

LEYENDA


- Bancada o mueble bajo
- Equipo refrigerado
- Encimera o tabla corrida
- Aparato (trazos: bajo encimera)
- Tabla de madera
- Muro de carga / medianera

HOLGURAS Y ALTURAS

Pasillo de cocina, mínimo	0,84 m
Paso de servicio en barra	1,05 m
Entrada a la cocina, bajo la viga	1,24 m
Huevo libre de mesada en barra	0,75 m
Altura de encimera	0,90 m
Borde inferior de la campana	2,00 m

NOTAS


Cada máquina es un producto real de makro.es con sus medidas de ficha; la web bloquea el acceso directo, así que las medidas vienen de su buscador. Confirmar en la ficha antes de comprar. Cocción y campana metidas en el hundimiento de 0,275 de la medianera Norte, como pidió el cliente. Mesada refrigerada de una sola pieza (2,54, la más larga de Makro) pegada al doblez de la L; 0,33 libras junto a la cocción. K6 bajo el escurridor de K7. Pasillo de cocina de 0,84 a 0,98. Muro Oeste: 3,04 de aparatos en los 3,33 que hay hasta P1. Trasbarra nueva del 19 set.: mesada corrida de 0,60 entre P1 y P2, con estante encima; la nevera A5 va bajo el hueco libre y nada bajo el fregadero A4. Alturas por confirmar: A4 y A5 miden 0,85 y la encimera va a 0,90, con 5 cm de desnivel en A4 y 1-2 de holgura sobre A5. La altura libre que pide A3 para llenar la cuba no consta: medirla antes de colgar A6.

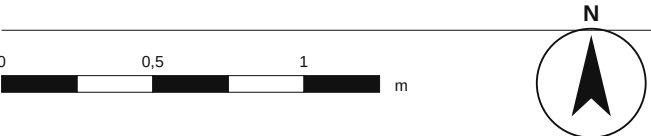

ESCALA	FECHA	PLANO
1:25 (A3)	19 set. 2026	03 / 04


BARRA

trasbarra 2,75 entre P1 y P2 · mostrador 2,79 · paso de personal 0,95

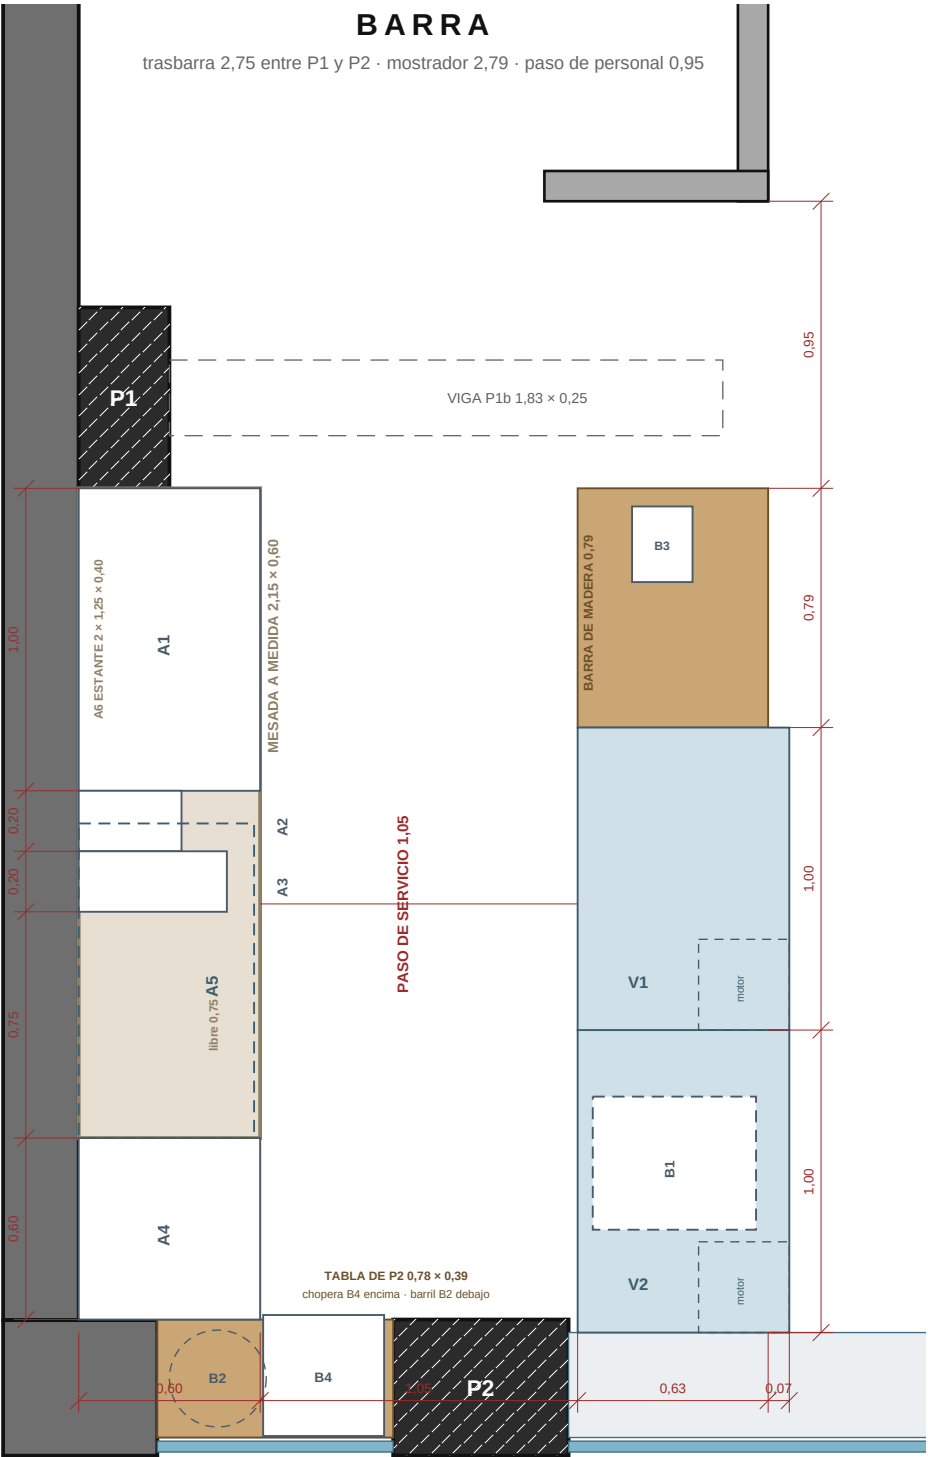

COCINA

2,18 x 3,20 m · hundimiento de 0,275 al Norte · entrada bajo la viga P1b

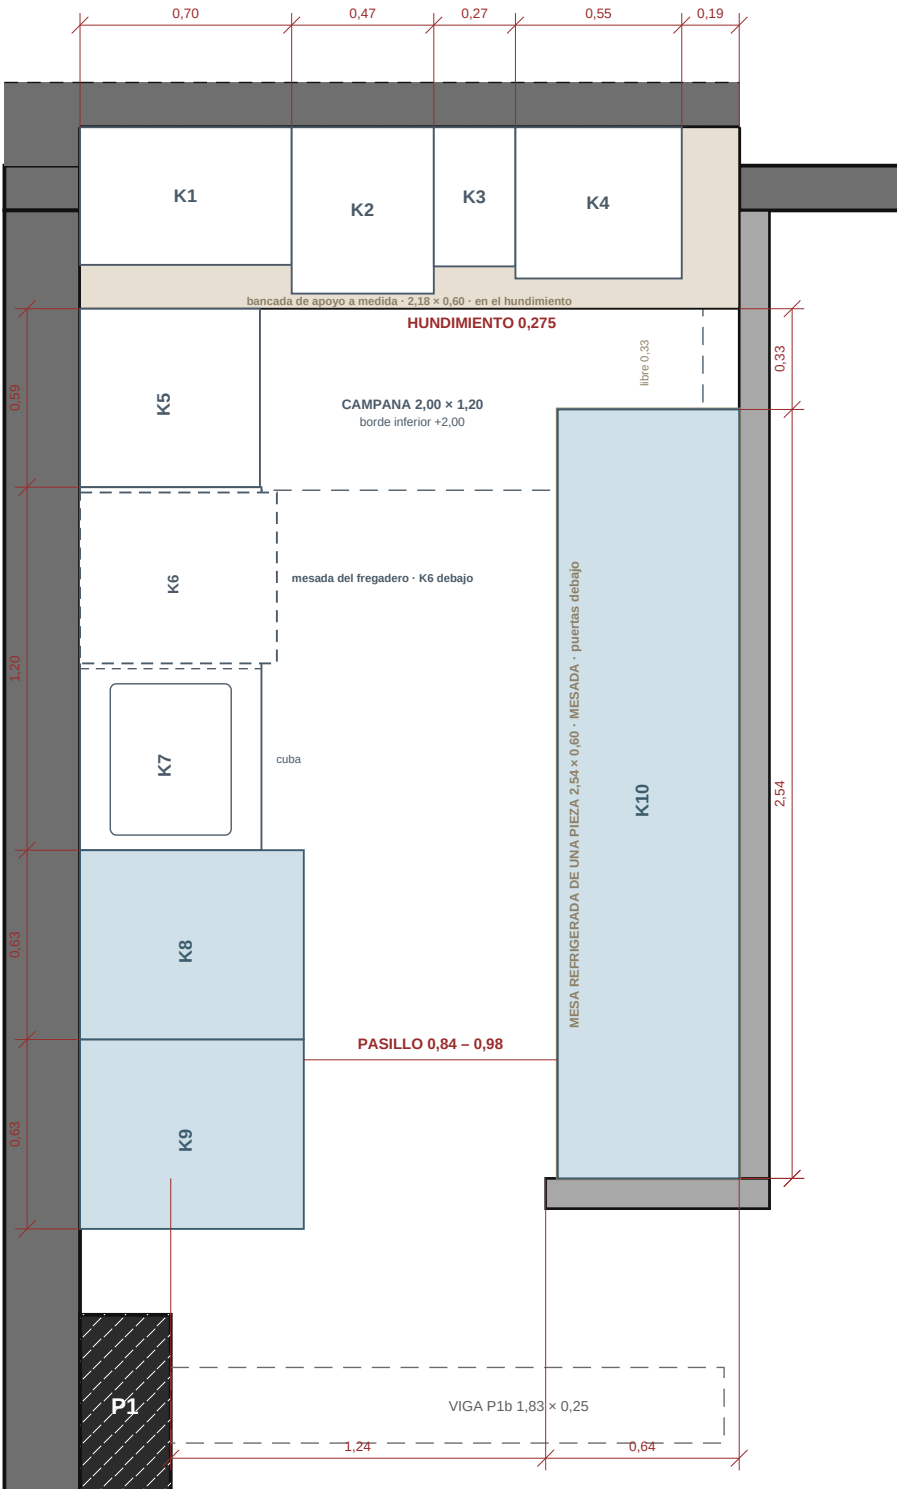

EQUIPAMIENTO · MAKRO

Ancho x fondo x alto en metros, de la ficha de makro.es. Vitrinas y cafetera ya compradas. Tablet y barriles con medida promedio. Enlaces en la lámina 04.

K1	Placa de inducción Bartscher, 2 zonas Ø230, 6 kW, 400 V	0,70 × 0,46 × 0,12	A2	Molinillo de café Cunil TRANQUILO de ABC, 275 W, tolva 0,5 kg	0,17 × 0,34 × 0,41
K2	Cocedor de pasta eléctrico METRO Professional GNC1008, 8 L, 4 cestos	0,47 × 0,55 × 0,38	A3	Máquina de helado y crema fría Bras B-CREAM1HD, 6 L, italiana	0,20 × 0,49 × 0,62
K3	Freidora profesional 1 cuba de 7 L, eléctrica	0,27 × 0,46 × 0,37	A4	Fregadero de pie 1 seno con estante y bastidor, 600 × 600 × 850	0,60 × 0,60 × 0,85
K4	Plancha eléctrica Cleiton 50 cm, placa de 8 mm, sobremesa	0,55 × 0,50 × 0,33	A5	Botellero frigorífico BTL1000, 2 puertas correderas, 240 L	1,04 × 0,58 × 0,85
KC	Campana extractora industrial recta, sin turbina, AISI-304 satinado, 2 × 1,2 m	2,00 × 1,20 × 0,50	A6	Estante mural cartelas compacto Fricosmos 011410, 1250 × 400 × 245	1,25 × 0,40 × 0,24
K5	Horno de convección eléctrico industrial, 4 bandejas 45 × 33	0,59 × 0,59 × 0,57	V2	Vitrina refrigerada (comprada), 1,00 × 0,70; debajo, lavavasos	1,00 × 0,70 × 1,25
K7	Fregadero con bastidor con hueco lavavajillas, cuba izquierda, 1200 × 600	1,20 × 0,60 × 0,85	V1	Vitrina refrigerada (comprada), 1,00 × 0,70; hueco libre debajo	1,00 × 0,70 × 1,25
K6	Lavavajillas industrial ST500, cesta 50 × 50, bajo el escurridor de K7	0,56 × 0,65 × 0,86	B1	Lavavasos Elettrobar FAST 40, cesta 40 × 40 (bajo la vitrina V2)	0,44 × 0,54 × 0,67
K8	Armario refrigerado vertical Edenox APS-451 I, inox, 1 puerta, 395 L	0,63 × 0,74 × 1,86	B2	Barriles de cerveza de 30 L, Ø 0,32 (debajo de la tabla de P2)	0,32 × 0,32 × 0,60
K9	Armario refrigerado vertical Edenox APS-451 I, inox, 1 puerta, 395 L	0,63 × 0,74 × 1,86	B3	Caja: tablet sobre soporte (lo único que queda en el mostrador)	0,25 × 0,20 × 0,25
K10	Mesa refrigerada Infrico 4 puertas, AISI-304, peto 100 mm, -2/+8 °C, 530 L	2,54 × 0,60 × 0,85	B4	Columna de cerveza en T de 3 grifos, bandeja 40 × 40, sobre la tabla de P2	0,40 × 0,40 × 0,55
A1	Cafetera (comprada), 2 grupos	1,00 × 0,60 × 0,50	A7	Armario expositor de bebidas Gasfit, 1 puerta de cristal, 400 L	0,54 × 0,58 × 1,92

LISTA DE EQUIPAMIENTO · MAKRO

Todo lo que hay que comprar para la barra y la cocina, con la ficha de makro.es de cada producto. Medidas en metros, ancho × fondo × alto. Los enlaces de la última columna son clicables en el PDF.

EQUIPOS DIBUJADOS EN LAS LÁMINAS 01 Y 03

RÓTULO	PRODUCTO	MEDIDAS	DÓNDE VA	FICHA EN MAKRO.ES
K1	Placa de inducción Bartscher, 2 zonas Ø230, 6 kW, 400 V	0,70 × 0,46 × 0,12	Cocina · cocción, medianera Norte, bajo la campana, 1º desde el Oeste	https://www.makro.es/marketplace/product/623ef78b-af50-4e27-a2c5-b3a45089ba59
K2	Cocedor de pasta eléctrico METRO Professional GNC1008, 8 L, 4 cestos	0,47 × 0,55 × 0,38	Cocina · cocción, bajo la campana, 2º	https://www.makro.es/marketplace/product/85f3fb44-3f09-463c-ab29-53822c8c1ce7
K3	Freidora profesional 1 cuba de 7 L, eléctrica	0,27 × 0,46 × 0,37	Cocina · cocción, bajo la campana, 3º	https://www.makro.es/marketplace/product/57e9d9ed-d483-4f88-a049-5597b3a7ad18
K4	Plancha eléctrica Cleiton 50 cm, placa de 8 mm, sobremesa	0,55 × 0,50 × 0,33	Cocina · cocción, bajo la campana, 4º, contra la pared en L	https://www.makro.es/marketplace/product/acd212b2-73a4-42bc-bea7-329d5ab4771d
KC	Campana extractora industrial recta, sin turbina, AISI-304 satinado, 2 × 1,2 m	2,00 × 1,20 × 0,50	Cocina · campana mural corrida sobre K1 a K4, borde inferior a +2,00	https://www.makro.es/marketplace/product/a8240770-cb5f-491b-926d-83b1e1e00a22
K5	Horno de convección eléctrico industrial, 4 bandejas 45 × 33	0,59 × 0,59 × 0,57	Cocina · muro Oeste, esquina Norte, sobre soporte	https://www.makro.es/marketplace/product/e3c35b3b-14d3-4e2b-a109-373a863ddff9
K7	Fregadero con bastidor con hueco lavavajillas, cuba izquierda, 1200 × 600	1,20 × 0,60 × 0,85	Cocina · muro Oeste, entre el horno y los frigoríficos; cuba al Sur, escurridor al Norte	https://www.makro.es/marketplace/product/c0cd57f0-35a2-485a-98f4-5dff6c628d84e
K6	Lavavajillas industrial ST500, cesta 50 × 50, bajo el escurridor de K7	0,56 × 0,65 × 0,86	Cocina · muro Oeste, bajo el escurridor del fregadero K7 (hueco de lavavajillas)	https://www.makro.es/marketplace/product/b6893f6e-6c55-499e-8e8b-4e246d107961
K8	Armario refrigerado vertical Edenox APS-451 I, inox, 1 puerta, 395 L	0,63 × 0,74 × 1,86	Cocina · muro Oeste, vertical, al Sur del fregadero	https://www.makro.es/marketplace/product/2e636462-1801-45f6-a3d8-15413909cb8c
K9	Armario refrigerado vertical Edenox APS-451 I, inox, 1 puerta, 395 L	0,63 × 0,74 × 1,86	Cocina · muro Oeste, vertical, contra P1	https://www.makro.es/marketplace/product/2e636462-1801-45f6-a3d8-15413909cb8c
K10	Mesa refrigerada Infrico 4 puertas, AISI-304, peto 100 mm, -2/+8 °C, 530 L	2,54 × 0,60 × 0,85	Cocina · pared en L, de una pieza, pegada al doblez; 0,33 libres junto a la cocción	https://www.makro.es/marketplace/product/764bc52f-1287-4e08-89dc-c2e453dfea49
A1	Cafetera (comprada), 2 grupos	1,00 × 0,60 × 0,50	Barra · trasbarra, sobre la mesada, pegada a P1 (extremo Norte)	ya comprado / medida promedio, sin ficha
A2	Molinillo de café Cunil TRANQUILO de ABC, 275 W, tolva 0,5 kg	0,17 × 0,34 × 0,41	Barra · trasbarra, en el hueco de 0,20 a la derecha de la cafetera	https://www.makro.es/marketplace/product/f2df0f65-b185-40b2-b2e2-2cd42fb2eefd
A3	Máquina de helado y crema fría Bras B-CREAM1HD, 6 L, italiana	0,20 × 0,49 × 0,62	Barra · trasbarra, sobre la mesada, a la derecha del molinillo	https://www.makro.es/marketplace/product/e4ddc7ec-739d-4b14-968b-1d230076b476
A4	Fregadero de pie 1 seno con estante y bastidor, 600 × 600 × 850	0,60 × 0,60 × 0,85	Barra · trasbarra, de pie contra P2 (extremo Sur); sustituye ese tramo de mesada	https://www.makro.es/marketplace/product/31bf0e3c-d322-4e34-a968-9bd9ace2024d
A5	Botellero frigorífico BTL1000, 2 puertas correderas, 240 L	1,04 × 0,58 × 0,85	Barra · trasbarra, debajo de la mesada, bajo el hueco libre	https://www.makro.es/marketplace/product/77c7b69b-09e0-4c28-878e-9454ffff60ec
A6	Estante mural cartelas compacto Fricosmos 011410, 1250 × 400 × 245	1,25 × 0,40 × 0,24	Barra · trasbarra, estante mural sobre la mesada (2 piezas, 2,50 en total)	https://www.makro.es/marketplace/product/8af91e42-ebf3-4239-8e01-9b6b82b73120
V2	Vitrina refrigerada (comprada), 1,00 × 0,70; debajo, lavavasos	1,00 × 0,70 × 1,25	Barra · mostrador delantero, junto al zócalo del ventanal (Sur); lavavasos debajo	ya comprado / medida promedio, sin ficha
V1	Vitrina refrigerada (comprada), 1,00 × 0,70; hueco libre debajo	1,00 × 0,70 × 1,25	Barra · mostrador delantero, al Norte de V2	ya comprado / medida promedio, sin ficha
B1	Lavavasos Elettrobar FAST 40, cesta 40 × 40 (bajo la vitrina V2)	0,44 × 0,54 × 0,67	Barra · bajo la vitrina V2	https://www.makro.es/marketplace/product/e858e346-8373-4e64-aa03-6f9a559e168e
B2	Barriles de cerveza de 30 L, Ø 0,32 (debajo de la tabla de P2)	0,32 × 0,32 × 0,60	Barra · debajo de la tabla de P2	ya comprado / medida promedio, sin ficha
B3	Caja: tablet sobre soporte (lo único que queda en el mostrador)	0,25 × 0,20 × 0,25	Barra · barra de madera del mostrador (única cosa que queda en ella)	ya comprado / medida promedio, sin ficha
B4	Columna de cerveza en T de 3 grifos, bandeja 40 × 40, sobre la tabla de P2	0,40 × 0,40 × 0,55	Barra · encima de la tabla de P2	https://www.makro.es/marketplace/product/f2d9d7ba-6f4f-4feb-b032-641cc4d828fe
A7	Armario expositor de bebidas Gasfrit, 1 puerta de cristal, 400 L	0,54 × 0,58 × 1,92	Sala · contra la cara Sur de P3 (la que mira al ventanal), centrada: 0,055 a cada lado	https://www.makro.es/marketplace/product/838afb41-8f56-42d2-918a-dbbf87166ff8

ALTERNATIVAS CON LA MISMA FUNCIÓN · no dibujadas

SUSTITUYE	PRODUCTO	MEDIDAS	DÓNDE VA	FICHA EN MAKRO.ES
K10	Mesa refrigerada Vaiotec EASYLINE, inox, 4 puertas, GN 1/1, 553 L	2,23 × 0,70 × 0,85	Cocina · pared en L, en lugar de K10, pegada al doblez; fondo 0,70; 0,73 libres	https://www.makro.es/marketplace/product/230e627d-7291-43e0-a2b4-ebbf6e783f27
K10	METRO Professional GCC3100, inox, 3 puertas, 334 L (la de la foto, refrigerada)	1,79 × 0,70 × 0,85	Cocina · pared en L, en lugar de K10, pegada al doblez; deja 1,16 libres	https://www.makro.es/marketplace/product/176b30f1-81b0-4a52-916e-80722d9a9240
K6	Lavavajillas Eurast 50 × 50, 575 × 600 × 820: cabe seguro bajo el escurridor	0,57 × 0,60 × 0,82	Cocina · en lugar de K6 si el ST500 no entra bajo el escurridor (0,82 de alto)	https://www.makro.es/marketplace/product/1acedc0e-199c-449c-b390-a8626c771613
K8/K9	Armario frigorífico ventilado 400 L, acero inoxidable (Diamond)	0,63 × 0,74 × 1,93	Cocina · muro Oeste, en lugar de K8 y K9; misma huella que el Edenox	https://www.makro.es/marketplace/product/8969b667-b5cb-4e83-b599-3dd45c112547
K8/K9	Armario refrigerado AR400L Clima Hostelería, lacado blanco (no inox), 360 L	0,60 × 0,61 × 1,87	Cocina · muro Oeste, en lugar de K8 y K9 (0,60 de ancho, lacado blanco)	https://www.makro.es/marketplace/product/d48c3c0c-7975-4c22-89c7-64676c23681f
A3	Granizadora GRANICREAM 1S Eurofred, 1 cuba de 10 L, cremas de café	0,20 × 0,50 × 0,79	Barra · alternativa a A3: misma anchura, 10 L, pero 0,79 de alto	https://www.makro.es/marketplace/product/e826e334-3cba-44fc-a530-627af1dabaf6
A3	Granizadora GRANISMART 5x1 Eurofred, 1 cuba de 5 L (la más baja)	0,26 × 0,40 × 0,63	Barra · alternativa a A3: cuba de 5 L, 0,26 de ancho y solo 0,40 de fondo	https://www.makro.es/marketplace/product/635e0924-0d3e-42ca-965e-e66eb41cdee1
A6	Estante en inox de pared, 2000 × 400 × 250, de una sola pieza	2,00 × 0,40 × 0,25	Barra · alternativa a A6: una sola pieza de 2,00 en vez de dos de 1,25	https://www.makro.es/marketplace/product/15f4f100-83b5-4f51-a383-11acf9989372
A4	Fregadero 1 cubeta con puerta, Gama 600 Distform, 600 × 600 × 850	0,60 × 0,60 × 0,85	Barra · alternativa al fregadero A4, con puerta (mismo hueco)	https://www.makro.es/marketplace/product/3efac5b4-e702-4af6-9dd9-533709488190
A4	Fregadero industrial 1 cuba AISI-304, 700 × 600 × 850	0,70 × 0,60 × 0,85	Barra · alternativa al fregadero A4 en AISI-304, 0,10 más ancho	https://www.makro.es/marketplace/product/95121b55-b486-4a76-a3de-ed7874e75876
A5	Botellero inox interior y exterior, 2 puertas, 200 L, Eurast	1,02 × 0,55 × 0,85	Barra · alternativa a la nevera A5 (1,02, inox interior y exterior)	https://www.makro.es/marketplace/product/a046bf7e-9d25-4304-9593-1cd32668e47f
A5	Botellero refrigerado de bar Yostin, 2 puertas, 100 cm, AISI-304	1,00 × 0,55 × 0,84	Barra · alternativa a la nevera A5 (1,00 exactos, fabricación nacional)	https://www.makro.es/marketplace/product/6589602e-de66-484c-871f-68f83b182638
A7	Expositor de bebidas Cleiton 300 L, 600 × 550 × 1950 (el de menos fondo)	0,60 × 0,55 × 1,95	Sala · alternativa a A7: 0,55 de fondo, deja 0,95 de paso; 0,60 de ancho y 300 L	https://www.makro.es/marketplace/product/f5b5e547-6c80-49b0-8b30-5ef9fb3fdc97
A7	Expositor slimline Polar CS586, 300 L, 448 × 680 × 1900 (el más estrecho)	0,45 × 0,68 × 1,90	Sala · alternativa a A7: 0,45 de ancho, pero 0,68 de fondo, con lo que el paso baja a 0,82	https://www.makro.es/marketplace/product/59efd1b6-9520-4ee6-8f04-ecc98098a572

SIN SITIO EN LA TRASBARRA NUEVA · decidir dónde van

ERA	PRODUCTO	MEDIDAS	DÓNDE VA	FICHA EN MAKRO.ES
A3	Fabricador de hielo Gastro M CT694, 28 kg/24 h (bajo encimera)	0,40 × 0,46 × 0,67	Sin sitio en la trasbarra nueva: decidir dónde va	https://www.makro.es/marketplace/product/e3db53e1-8f64-4495-bb2c-59fe355a32e2
A4	Exprimidor de naranjas Mizumo Next Gen	0,48 × 0,35 × 0,73	Sin sitio en la trasbarra nueva: cabría en el hueco libre de mesada	https://www.makro.es/marketplace/product/a7c3e878-0ccd-4f7e-b013-897ae4f6120d
A2	Lavamanos inox con grifo y pulsador de pedal, cuba Ø340	0,40 × 0,40 × 0,85	Sin sitio: lo sustituye el fregadero A4, pegado a P2	https://www.makro.es/marketplace/product/6105678f-3159-4172-a17a-f400760f0b35
A3b	Licuadaora industrial Sammic Li-240	0,20 × 0,31 × 0,36	Sin sitio en la trasbarra nueva: decidir dónde va	https://www.makro.es/marketplace/product/2b8d9850-b422-4738-b716-c30da9857300

A MEDIDA · no se compran en Makro

- Bancada de apoyo de la línea de cocción, dentro del hundimiento: 2,18 × 0,60, acero inoxidable.
- Mesada de la trasbarra, de P1 al fregadero A4: 2,15 × 0,60 (el fregadero A4, de pie, hace los otros 0,60).
- Hueco de 0,20 para el molinillo A2 y los utensilios, a la derecha de la cafetera.
- Barra de madera del mostrador delantero: 0,79 × 0,63.
- Tabla de P2 al muro: 0,78 × 0,39 (chopera B4 encima, barril B2 debajo).
- Mostrador delantero: 2,79 × 0,63 de fondo, del zócalo del ventanal a P1.

VERIFICACIÓN DE LOS ENLACES

makro.es responde 403 a cualquier acceso desde un servidor, así que las fichas no se pueden abrir desde el entorno de trabajo. Cada enlace se verificó buscando su identificador con el buscador restringido a makro.es: todos devuelven su URL con el título del producto (LISTA_MAKRO.md). La del fregadero K7 la facilitó el cliente. Confirmar precio y stock.

GRUPO SUMA

Reformas y proyectos · Málaga

PROYECTO

Reforma integral de local de hostelería

EMPLAZAMIENTO

Local en planta baja y altillo

Málaga

PLANO

EQUIPAMIENTO

Lista de compra · enlaces a makro.es

RESUMEN

Fichas distintas de Makro	18
Unidades a comprar en Makro	19
Ya comprado	cafetera y 2 vitrinas
Medida promedio	barriles y tablet
A medida	6 elementos

NOTAS

Medidas ancho × fondo × alto en metros, tomadas de la ficha de makro.es.

Los enlaces de la última columna son clicables en el PDF; en papel, copiar la dirección o buscar el título en makro.es.

Vitrinas y cafetera ya compradas, con las medidas del cliente. Barriles y tablet con medida promedio.

Confirmar precio y stock antes de comprar.

ESCALA	FECHA	PLANO
sin escala	19 set. 2026	04 / 04