

GRUPO SUMA

Reformas y proyectos · Málaga

PROYECTO

Reforma integral de local de hostelería

EMPLAZAMIENTO

Local en planta baja y altílo
Málaga

PLANO

PLANTA BAJA

Estado actual · estructura

LEYENDA

- Muro de carga / medianera
- Pilar o machón de hormigón
- Pared en L nueva (apoyo del vidrio)
- Carpintería acristalada
- Espacio de doble altura
- Forjado sobre el corte
- Reserva de espacio del cliente
- Mesas y sillas (medidas promedio)
- Itinerario accesible $\geq 1,20$ · giro $\varnothing 1,50$
- Punto de luz s/ proyecto original

SUPERFICIES Y ALTURAS

Planta baja, dentro de muros	75,63 m²
Zona de doble altura	37,80 m²
Suelo a suelo, medido en obra	2,56 m
Altura libre bajo forjado	2,56 – canto
Pared en L, altura	1,22 m
Plazas sentadas en planta baja	28
Acristalamiento de fachada	≈ 4,70 m

PILARES Y MACHONES (secciones en m)

P1 Machón del muro Oeste	0,30 × 0,60
P2 Pilastra del muro Sur	0,58 × 0,45
P3 Pilar central	0,65 × 1,07
P4 Machón de la medianera Este	0,20 × 0,60
P5 Pilar de fachada	0,60 × 1,00

NOTAS

Cotas en metros; pilares, pared en L, ventanal y puerta medidos en obra (14 set. 2026), el resto del levantamiento previo. $\pm 0,00$ en el pavimento de planta baja; sección horizontal a 1,20 m.
Mesas cuádruples de $1,20 \times 0,70$ (medida promedio).
Puntos de luz: los del proyecto de reforma original.
Itinerario accesible de 1,20 desde la puerta a la barra, al baño y a la plaza PMR de M2, con giros de $\varnothing 1,50$ en la entrada y ante el baño (DB-SUA).
El baño dibujado no es accesible: no cabe el giro.
Equipamiento de barra y cocina en la lámina 03; lista de compra con enlaces en la lámina 04.



ESCALA


1:50 (A3)

FECHA

15 set. 2026

PLANO

01 / 04

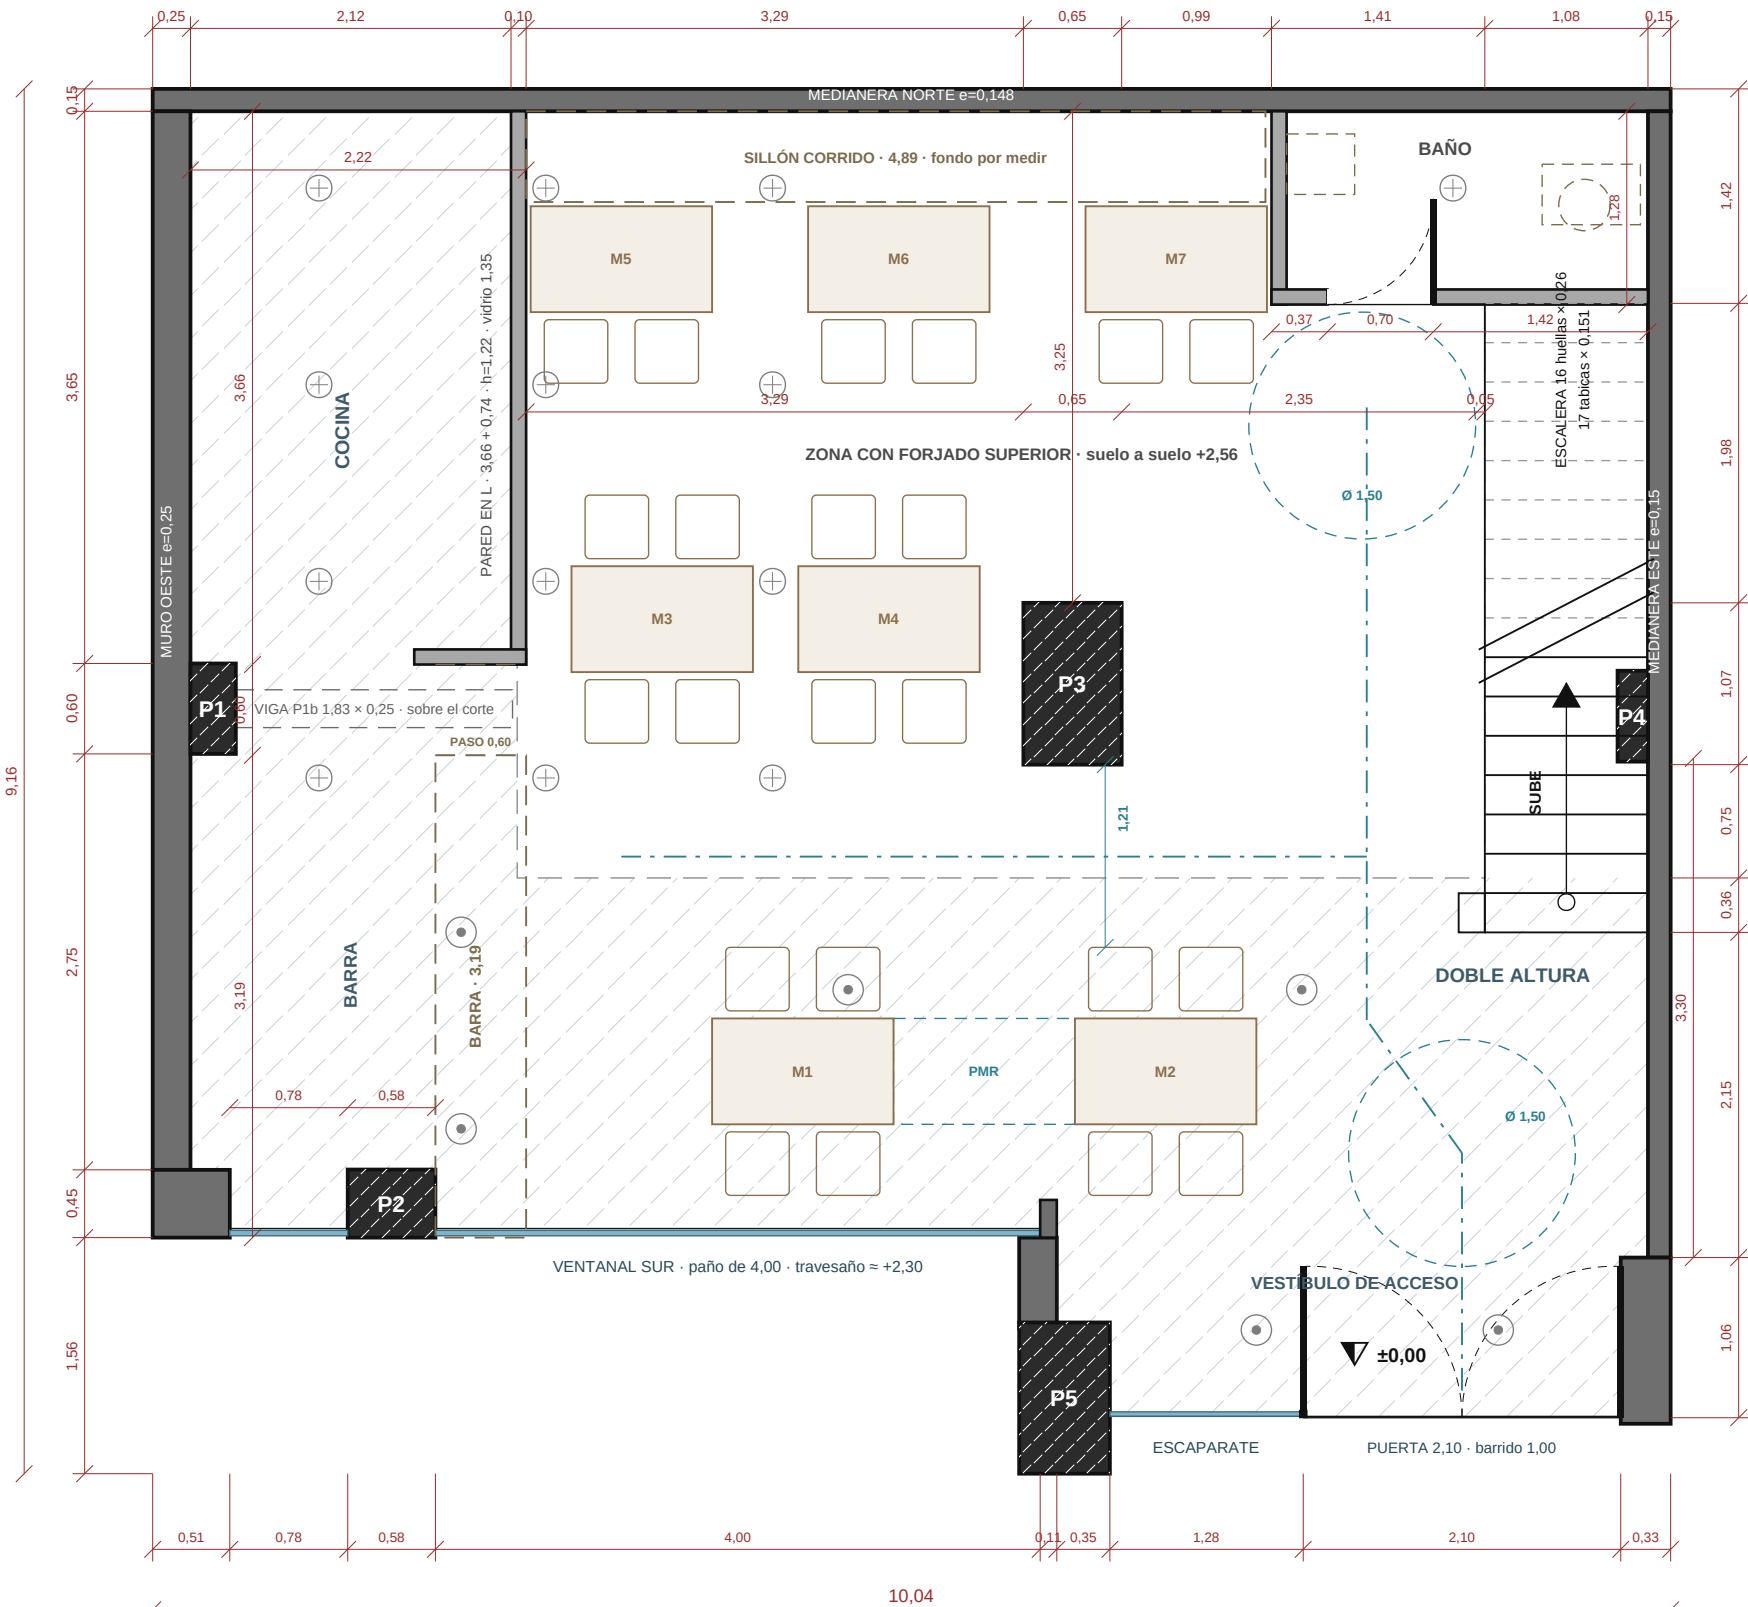

COMPROBAR EN OBRA

Puntos en los que los vídeos del local no cuadran con el levantamiento, o que el levantamiento no recoge. Se dibuja el levantamiento por ser la única fuente acotada.

- Pared en L: en el segundo croquis termina en $y=5,35$ (3,66 m) y la barra sube hasta 4,75 con el paso de 0,60 entre ambas. Antes se midió 4,22.
- Canto del forjado del altílo. Con 2,56 m de suelo a suelo, la altura libre de planta baja es 2,56 menos ese canto, no los 2,70 supuestos.
- P1b se dibuja como viga ($1,83 \times 0,25$) y no como pilar: si fuera macizo hasta el suelo, la cocina no tendría entrada. Medir su intradós.
- Baño nuevo: tabiques de 0,10 y puerta de 0,70 tomados del croquis, sin medir. Comprobar que la puerta abre hacia dentro sin chocar.
- P3 con las medidas de obra: 3,25 a la medianera Norte, 0,70 a la barandilla del altílo y 2,35 a la caja de escalera; a la pared en L quedan 3,29 (medido 3,20).
- En planta alta se midió 2,50 de P3 a la escalera (2,35 en baja) y 1,90 al tabique del aseo (plano 1,75); del arranque a la fachada 3,30 (plano 3,21).
- Pasillo de cocina: 0,78 m frente a los frigoríficos (0,74 de fondo) y hasta 0,92 en el resto. Por debajo de 0,90 con permiso del cliente.
- Tabica de la escalera: $2,56/17 = 0,151$ m. Contar los peldaños en obra.
- Máquinas: medidas de makro.es. Confirmar que el ST500 (0,83 de alto) cabe bajo el escurridor de K7 (0,85 total) y el alto de la columna B4 (0,55 estimado).

GRUPO SUMA

Reformas y proyectos · Málaga

PROYECTO

Reforma integral de local de hostelería

EMPLAZAMIENTO

Local en planta baja y altillo
Málaga

PLANO

PLANTA ALTA

Altillo +2,56 · estructura

LEYENDA

- Muro de carga / medianera
- Pilar o machón de hormigón
- Tabiquería
- Barandilla de vidrio
- Mesas y sillas (medidas promedio)
- Paso libre entre mobiliario (m)
- Vacío sobre planta baja

SUPERFICIES Y ALTURAS


Forjado de planta alta	33,74 m²
Altillo diáfano	26,17 m²
Aseo (lavabo + inodoro)	3,92 m²
Almacén	2,59 m²
Nivel del forjado, medido	+2,56 m
Puestos de cowork	14

PILARES Y MACHONES (secciones en m)


P1 Machón del muro Oeste	0,30 × 0,60
P2 Pilastra del muro Sur	0,58 × 0,45
P3 Pilar central	0,65 × 1,07
P4 Machón de la medianera Este	0,20 × 0,60
P5 Pilar de fachada	0,60 × 1,00

NOTAS

Cotas en metros, tomadas sobre el levantamiento.
Nivel del forjado +2,56, medido en obra.
El forjado del altillo no cubre todo el local: la franja sur y oeste es un vacío a doble altura.
Mesa de cowork 2,40 × 1,00 para 8 puestos y una redonda de Ø 1,20 con 6 sillas. Medidas promedio.
Pasos libres entre mobiliario acotados en azul:
1,01 hacia el aseo y el almacén; 1,30 en el desembarco; 0,37 a 0,80 en los accesos a las sillas.

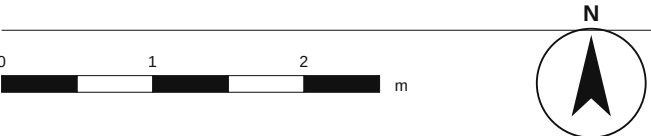

ESCALA	FECHA	PLANO
1:50 (A3)	15 set. 2026	02 / 04

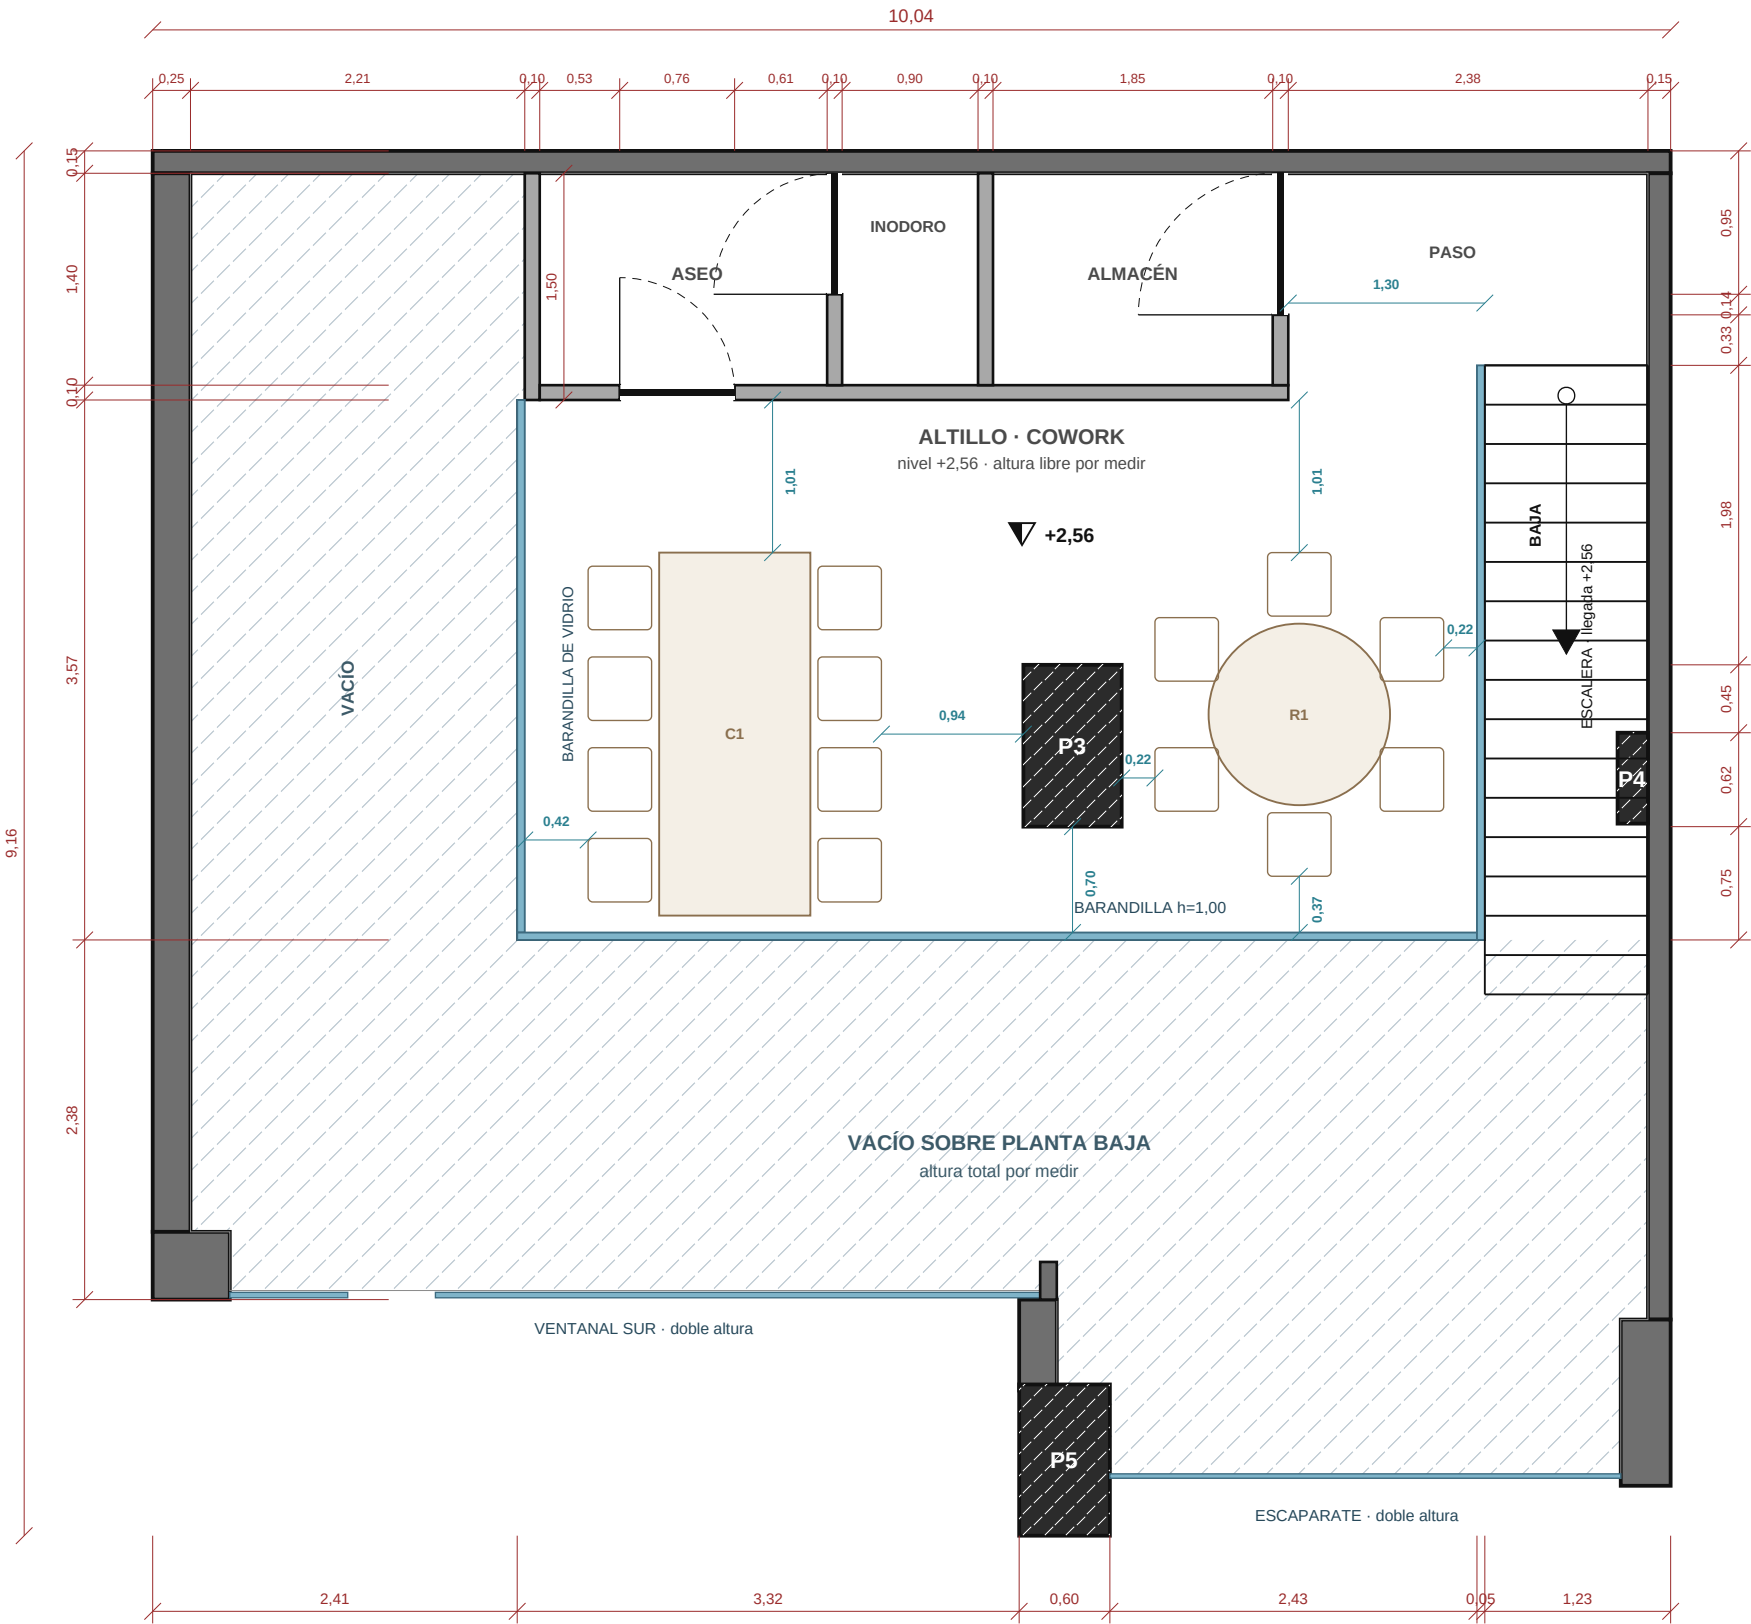

COMPROBAR EN OBRA Puntos en los que los vídeos del local no cuadran con el levantamiento, o que el levantamiento no recoge. Se dibuja el levantamiento por ser la única fuente acotada.

- Pared en L: en el segundo croquis termina en y=5,35 (3,66 m) y la barra sube hasta 4,75 con el paso de 0,60 entre ambas. Antes se midió 4,22.
- Canto del forjado del altillo. Con 2,56 m de suelo a suelo, la altura libre de planta baja es 2,56 menos ese canto, no los 2,70 supuestos.
- P1b se dibuja como viga (1,83 × 0,25) y no como pilar: si fuera macizo hasta el suelo, la cocina no tendría entrada. Medir su intradós.
- Baño nuevo: tabiques de 0,10 y puerta de 0,70 tomados del croquis, sin medir. Comprobar que la puerta abre hacia dentro sin chocar.
- P3 con las medidas de obra: 3,25 a la medianera Norte, 0,70 a la barandilla del altillo y 2,35 a la caja de escalera; a la pared en L quedan 3,29 (medido 3,20).
- En planta alta se midió 2,50 de P3 a la escalera (2,35 en baja) y 1,90 al tabique del aseo (plano 1,75); del arranque a la fachada 3,30 (plano 3,21).
- Pasillo de cocina: 0,78 m frente a los frigoríficos (0,74 de fondo) y hasta 0,92 en el resto. Por debajo de 0,90 con permiso del cliente.
- Tabica de la escalera: 2,56/17 = 0,151 m. Contar los peldaños en obra.
- Máquinas: medidas de makro.es. Confirmar que el ST500 (0,83 de alto) cabe bajo el escurridor de K7 (0,85 total) y el alto de la columna B4 (0,55 estimado).