

PROYECTO

Reforma integral de local de hostelería

EMPLAZAMIENTO

Local en planta baja y altillo
Málaga

PLANO

REPLANTEO DE LUCES

Planta baja · huecos en el techo

LEYENDA

- Luz empotrada y colgante
- Borde del forjado del altillo
- Viga P1b y campana de la cocina
- Cassette del aire acondicionado
- Cota de replanteo (m)
- Muro de carga / medianera
- Pilar, machón o montante
- Pared en L y tabiquería
- Carpintería acristalada

PUNTOS DE LUZ


Empotrados	13
Colgantes	6
Total	19

TECHO DONDE VA CADA LUZ

1 a 9 · bajo el altillo	2,56 – canto
10 a 12 · cocina, pladur	+2,31
13 a 18 · doble altura	≈ +5,06
19 · vestíbulo, pladur	+2,10

NOTAS

Cada luz lleva su número, el mismo que en la lámina 01.
Medidas en metros, al centro de cada luz, desde la cara sin revestir de la pared, del pilar o del borde del forjado; en el dibujo, en cadena por filas, y al pie, las dos de cada luz. El diámetro del hueco lo da la luminaria que se compre. Colgantes: punto de anclaje.
La fila 4-5-6 va 2 cm al Norte de la cara Norte de P3.
* 10: cae dentro de la campana de la cocina.
* 13: fuera del techo de la cocina, en la doble altura.
* 19: cuelga en el barrido de la hoja derecha de la puerta.

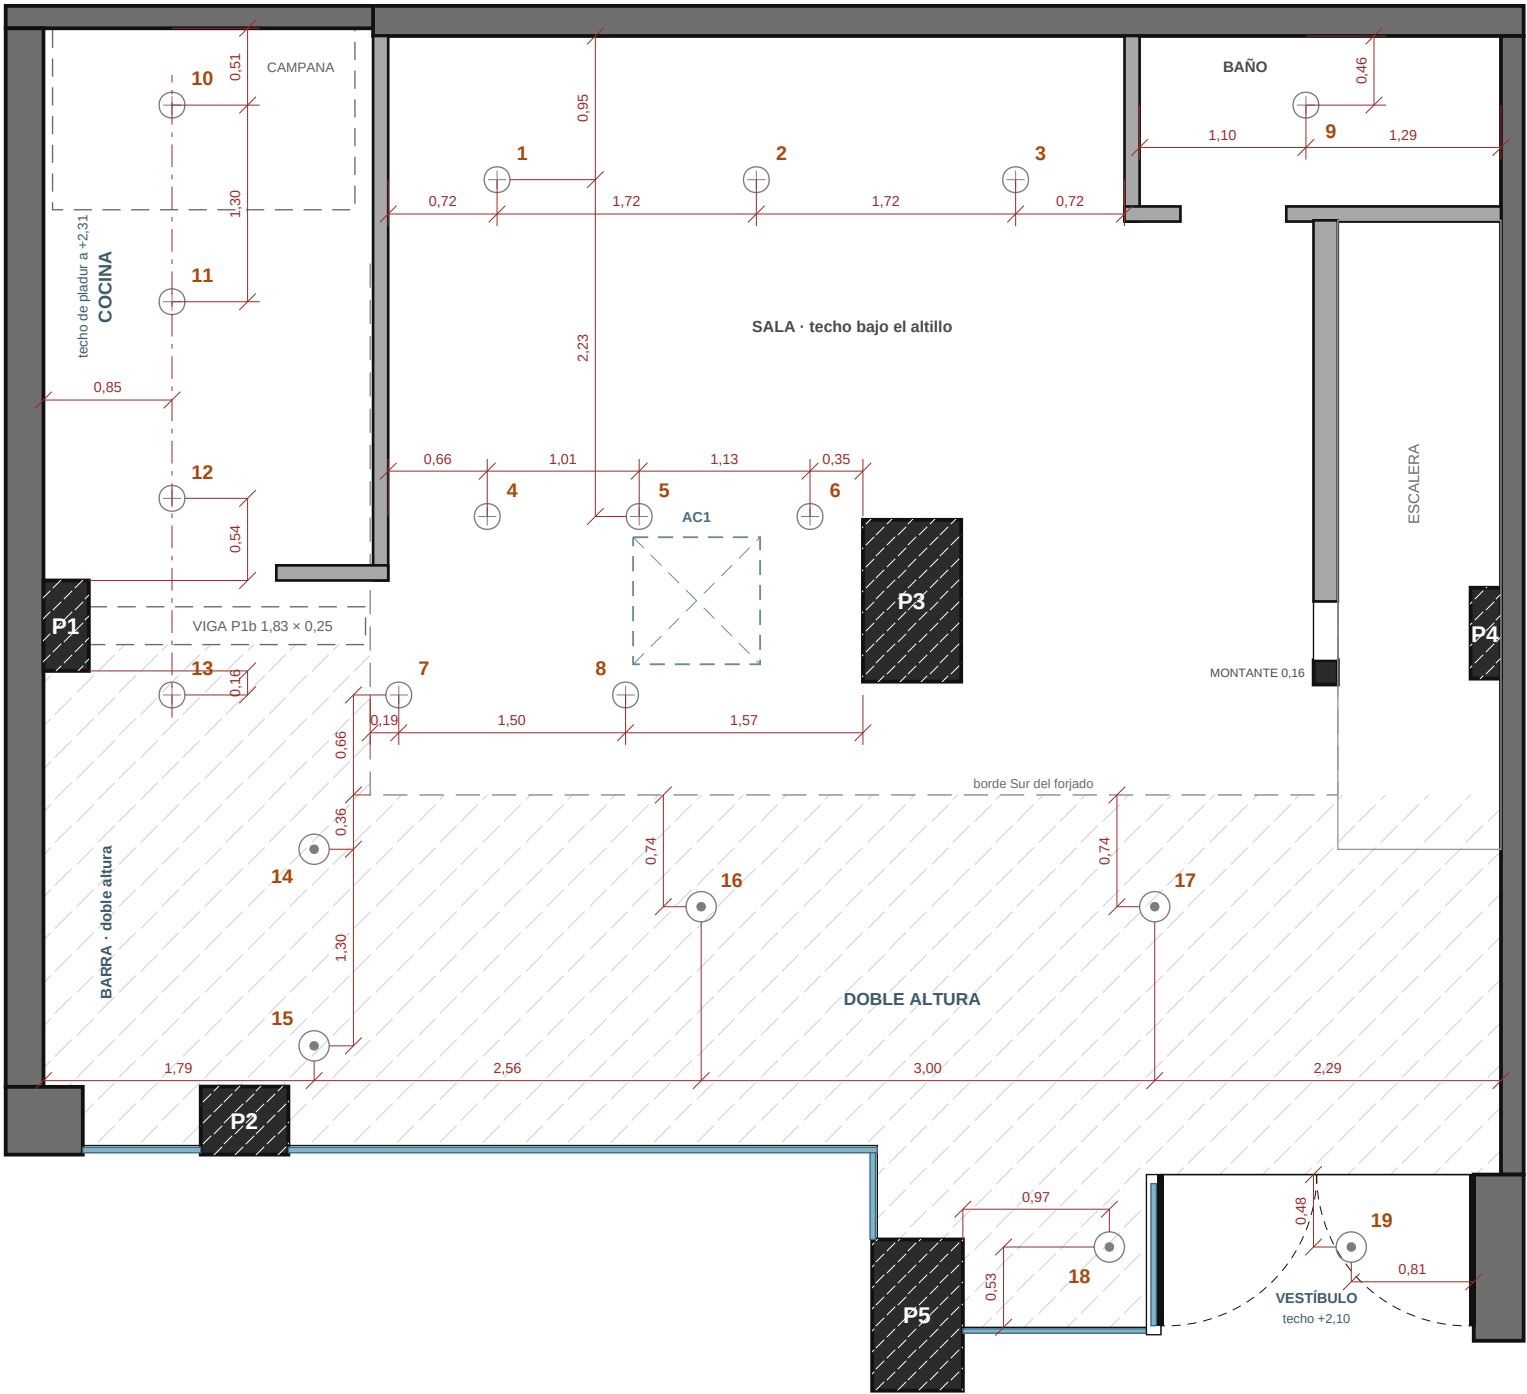

REPLANTEO DE LOS HUECOS

Metros, al centro de cada luz, desde la cara sin revestir de la pared, del pilar o del borde del forjado. * ver aviso en las notas.

Nº	Sitio	Este – Oeste	Norte – Sur	Nº	Sitio	Este – Oeste	Norte – Sur
1	mesa M7 · empotrado	0,72 de la pared en L	0,95 del muro Norte	11	cocina · empotrado	0,85 del muro Oeste	1,81 del muro Norte
2	mesa M10 · empotrado	2,44 de la pared en L	0,95 del muro Norte	12	cocina · empotrado	0,85 del muro Oeste	0,54 de la cara Norte de P1
3	mesa M11 · empotrado	0,72 del tabique del baño	0,95 del muro Norte	13 *	paso de personal · empotrado	0,85 del muro Oeste	0,16 de la cara Sur de P1
4	paso junto a la L · empotrado	0,66 de la pared en L	3,18 del muro Norte	14	barra · colgante	1,79 del muro Oeste	0,36 del borde Sur del forjado
5	mesa M5 · empotrado	1,48 de la cara Oeste de P3	3,18 del muro Norte	15	barra · colgante	1,79 del muro Oeste	1,66 del borde Sur del forjado
6	mesa M4 · empotrado	0,35 de la cara Oeste de P3	3,18 del muro Norte	16	sala · colgante	4,35 del muro Oeste	0,74 del borde Sur del forjado
7	sala, junto a la barra · empotrado	0,19 del borde Oeste del forjado	0,66 del borde Sur del forjado	17	sala · colgante	2,29 de la medianera Este	0,74 del borde Sur del forjado
8	sala · empotrado	1,57 de la cara Oeste de P3	0,66 del borde Sur del forjado	18	escaparate · colgante	0,97 de la cara Este de P5	0,53 del vidrio del escaparate
9	baño · empotrado	1,10 del tabique Oeste del baño	0,46 del muro Norte	19 *	vestíbulo · colgante	0,81 del cuello de la medianera	0,48 de la puerta de acceso
10 *	cocina · empotrado	0,85 del muro Oeste	0,51 del muro Norte				

ESCALA

1:50 (A3)

FECHA

29 set. 2026

PLANO

05 / 05