

PROYECTO

Reforma integral de local de hostelería

EMPLAZAMIENTO

Local en planta baja y altílo Málaga

PLANO

PLANTA BAJA

Estado actual · estructura

LEYENDA

- Muro de carga / medianera
- Pilar o machón de hormigón
- Pared en L nueva (apoyo del vidrio)
- Carpintería acristalada
- Espacio de doble altura
- Forjado sobre el corte
- Reserva de espacio del cliente
- Mesas y sillas (medidas promedio)
- Itinerario accesible  $\geq 1,20$  · giro  $\varnothing 1,50$
- Punto de luz: colgante / empotrado

SUPERFICIES Y ALTURAS

|                                |              |
|--------------------------------|--------------|
| Planta baja, dentro de muros   | 75,63 m²     |
| Zona de doble altura           | 37,80 m²     |
| Suelo a suelo, medido en obra  | 2,56 m       |
| Altura libre bajo forjado      | 2,56 – canto |
| Pared en L, altura             | 1,22 m       |
| Plazas sentadas en planta baja | 28           |
| Acristalamiento de fachada     | ≈ 4,70 m     |

PILARES Y MACHONES (secciones en m)

|                                |             |
|--------------------------------|-------------|
| P1 Machón del muro Oeste       | 0,30 × 0,60 |
| P2 Pilastra del muro Sur       | 0,58 × 0,45 |
| P3 Pilar central               | 0,65 × 1,07 |
| P4 Machón de la medianera Este | 0,20 × 0,60 |
| P5 Pilar de fachada            | 0,60 × 1,00 |

NOTAS

Cotas en metros; pilares, pared en L, ventanal y puerta medidos en obra (14 set. 2026), el resto del levantamiento previo.  $\pm 0,00$  en el pavimento de planta baja; sección horizontal a 1,20 m. Mesas de  $1,20 \times 0,70$  y  $0,70 \times 0,70$  (medida promedio); un colgante por mesa y empotrados en los pasos. Itinerario accesible de 1,20 desde la puerta a la barra, al baño y a la plaza PMR de M2, con giros de  $\varnothing 1,50$  en la entrada y ante el baño (DB-SUA). El baño dibujado no es accesible: no cabe el giro. Equipamiento de barra y cocina en la lámina 03; lista de compra con enlaces en la lámina 04.



ESCALA


1:50 (A3)

FECHA

15 set. 2026

PLANO

01 / 04

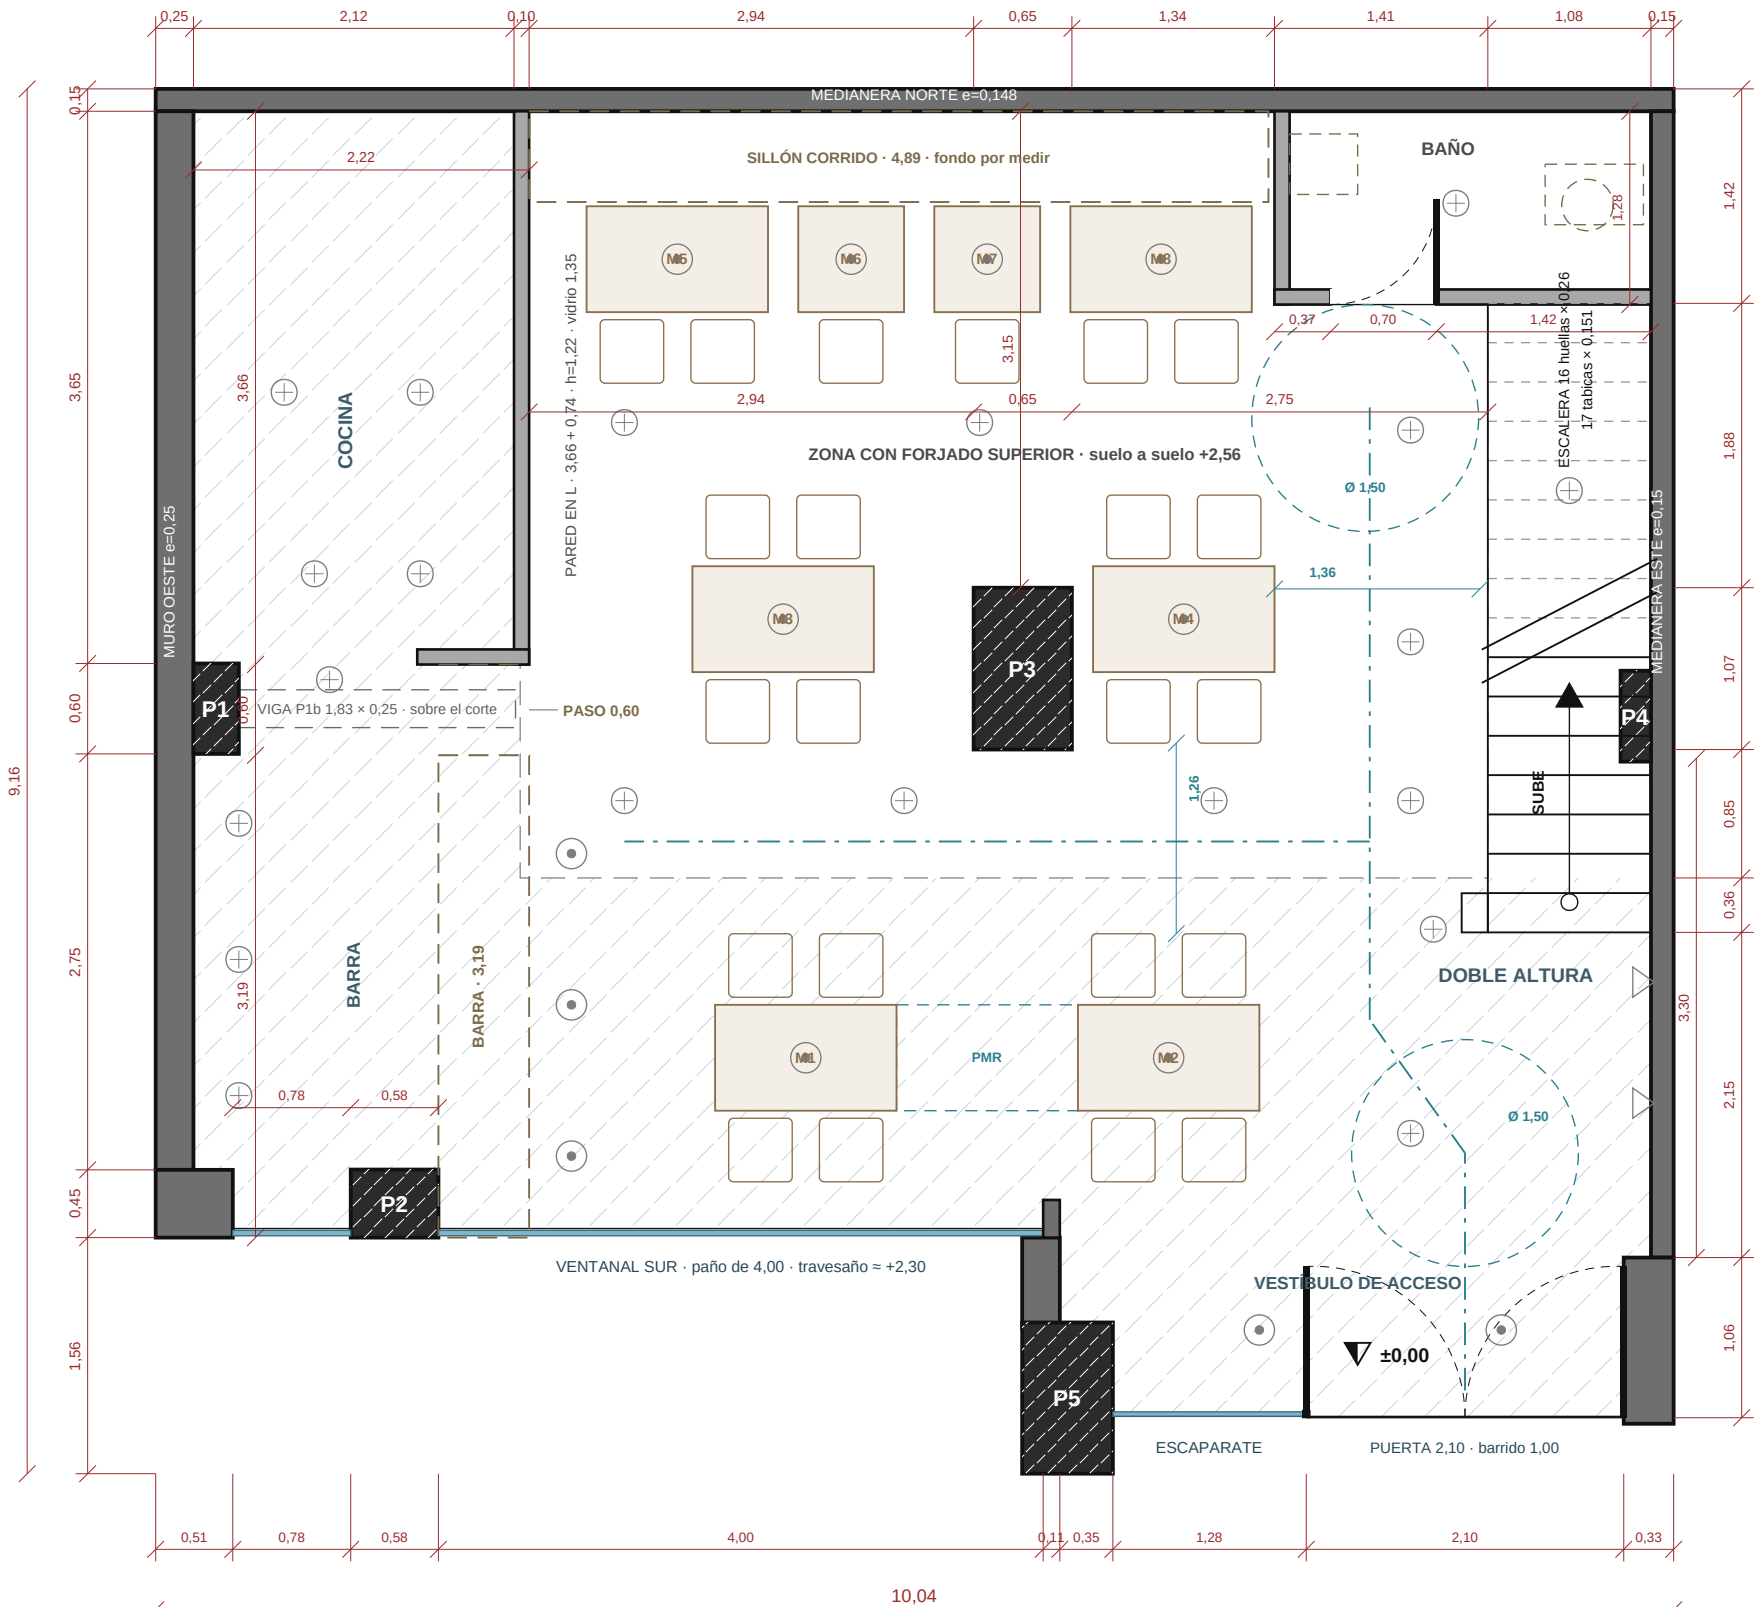

COMPROBAR EN OBRA Puntos en los que los vídeos del local no cuadran con el levantamiento, o que el levantamiento no recoge. Se dibuja el levantamiento por ser la única fuente acotada.

- Pared en L: en el segundo croquis termina en  $y=5,35$  (3,66 m) y la barra sube hasta 4,75 con el paso de 0,60 entre ambas. Antes se midió 4,22.
- Canto del forjado del altílo. Con 2,56 m de suelo a suelo, la altura libre de planta baja es 2,56 menos ese canto, no los 2,70 supuestos.
- P1b se dibuja como viga ( $1,83 \times 0,25$ ) y no como pilar: si fuera macizo hasta el suelo, la cocina no tendría entrada. Medir su intradós.
- Baño nuevo: tabiques de 0,10 y puerta de 0,70 tomados del croquis, sin medir. Comprobar que la puerta abre hacia dentro sin chocar.
- Posición de P3: el 3,15 de planta baja y el 1,90 de planta alta se llevan 0,15; el 2,94 y el 3,20 se llevan 0,26. Se usa la cadena de PB.
- Del P3 a la escalera se midió 2,35 y en el plano salen 2,75. Los 0,40 no cierran contra la medianera Este.
- Pasillo de cocina: 0,78 m frente a los frigoríficos (0,74 de fondo) y hasta 0,92 en el resto. Por debajo de 0,90 con permiso del cliente.
- Tabica de la escalera:  $2,56/17 = 0,151$  m. Contar los peldaños en obra.
- Máquinas: medidas de las fichas de makro.es según su buscador (la web bloquea el acceso directo). Sin dato: alto de la columna B4, 0,55 estimado.