

PROYECTO

Reforma integral de local de hostelería

EMPLAZAMIENTO

Local en planta baja y altílo Málaga

PLANO

PLANTA BAJA

Estado actual · estructura

LEYENDA

- Muro de carga / medianera
- Pilar o machón de hormigón
- Pared en L nueva (apoyo del vidrio)
- Carpintería acristalada
- Espacio de doble altura
- Forjado sobre el corte
- Reserva de espacio del cliente
- Mesas y sillas (medidas promedio)
- Itinerario accesible  $\geq 1,20$  · giro  $\varnothing 1,50$
- Punto de luz: colgante / empotrado

SUPERFICIES Y ALTURAS


|                                |              |
|--------------------------------|--------------|
| Planta baja, dentro de muros   | 75,63 m²     |
| Zona de doble altura           | 37,80 m²     |
| Suelo a suelo, medido en obra  | 2,56 m       |
| Altura libre bajo forjado      | 2,56 – canto |
| Pared en L, altura             | 1,22 m       |
| Plazas sentadas en planta baja | 28           |
| Acristalamiento de fachada     | ≈ 4,70 m     |

PILARES Y MACHONES (secciones en m)


|                                |             |
|--------------------------------|-------------|
| P1 Machón del muro Oeste       | 0,30 × 0,60 |
| P2 Pilastra del muro Sur       | 0,58 × 0,45 |
| P3 Pilar central               | 0,65 × 1,07 |
| P4 Machón de la medianera Este | 0,20 × 0,60 |
| P5 Pilar de fachada            | 0,60 × 1,00 |

NOTAS

Cotas en metros; pilares, pared en L, ventanal y puerta medidos en obra (14 set. 2026), el resto del levantamiento previo.  $\pm 0,00$  en el pavimento de planta baja; sección horizontal a 1,20 m. Mesas de  $1,20 \times 0,70$  y  $0,70 \times 0,70$  (medida promedio); un colgante por mesa y empotrados en los pasos. Itinerario accesible de 1,20 desde la puerta a la barra, al baño y a la plaza PMR de M2, con giros de  $\varnothing 1,50$  en la entrada y ante el baño (DB-SUA). El baño dibujado no es accesible: no cabe el giro. Equipamiento de barra y cocina en la lámina 03; lista de compra con enlaces en la lámina 04.

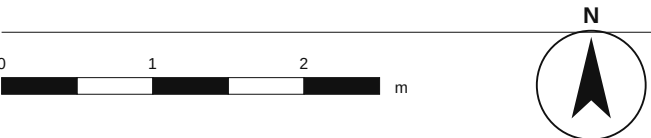

|           |              |         |
|-----------|--------------|---------|
| ESCALA    | FECHA        | PLANO   |
| 1:50 (A3) | 15 set. 2026 | 01 / 04 |

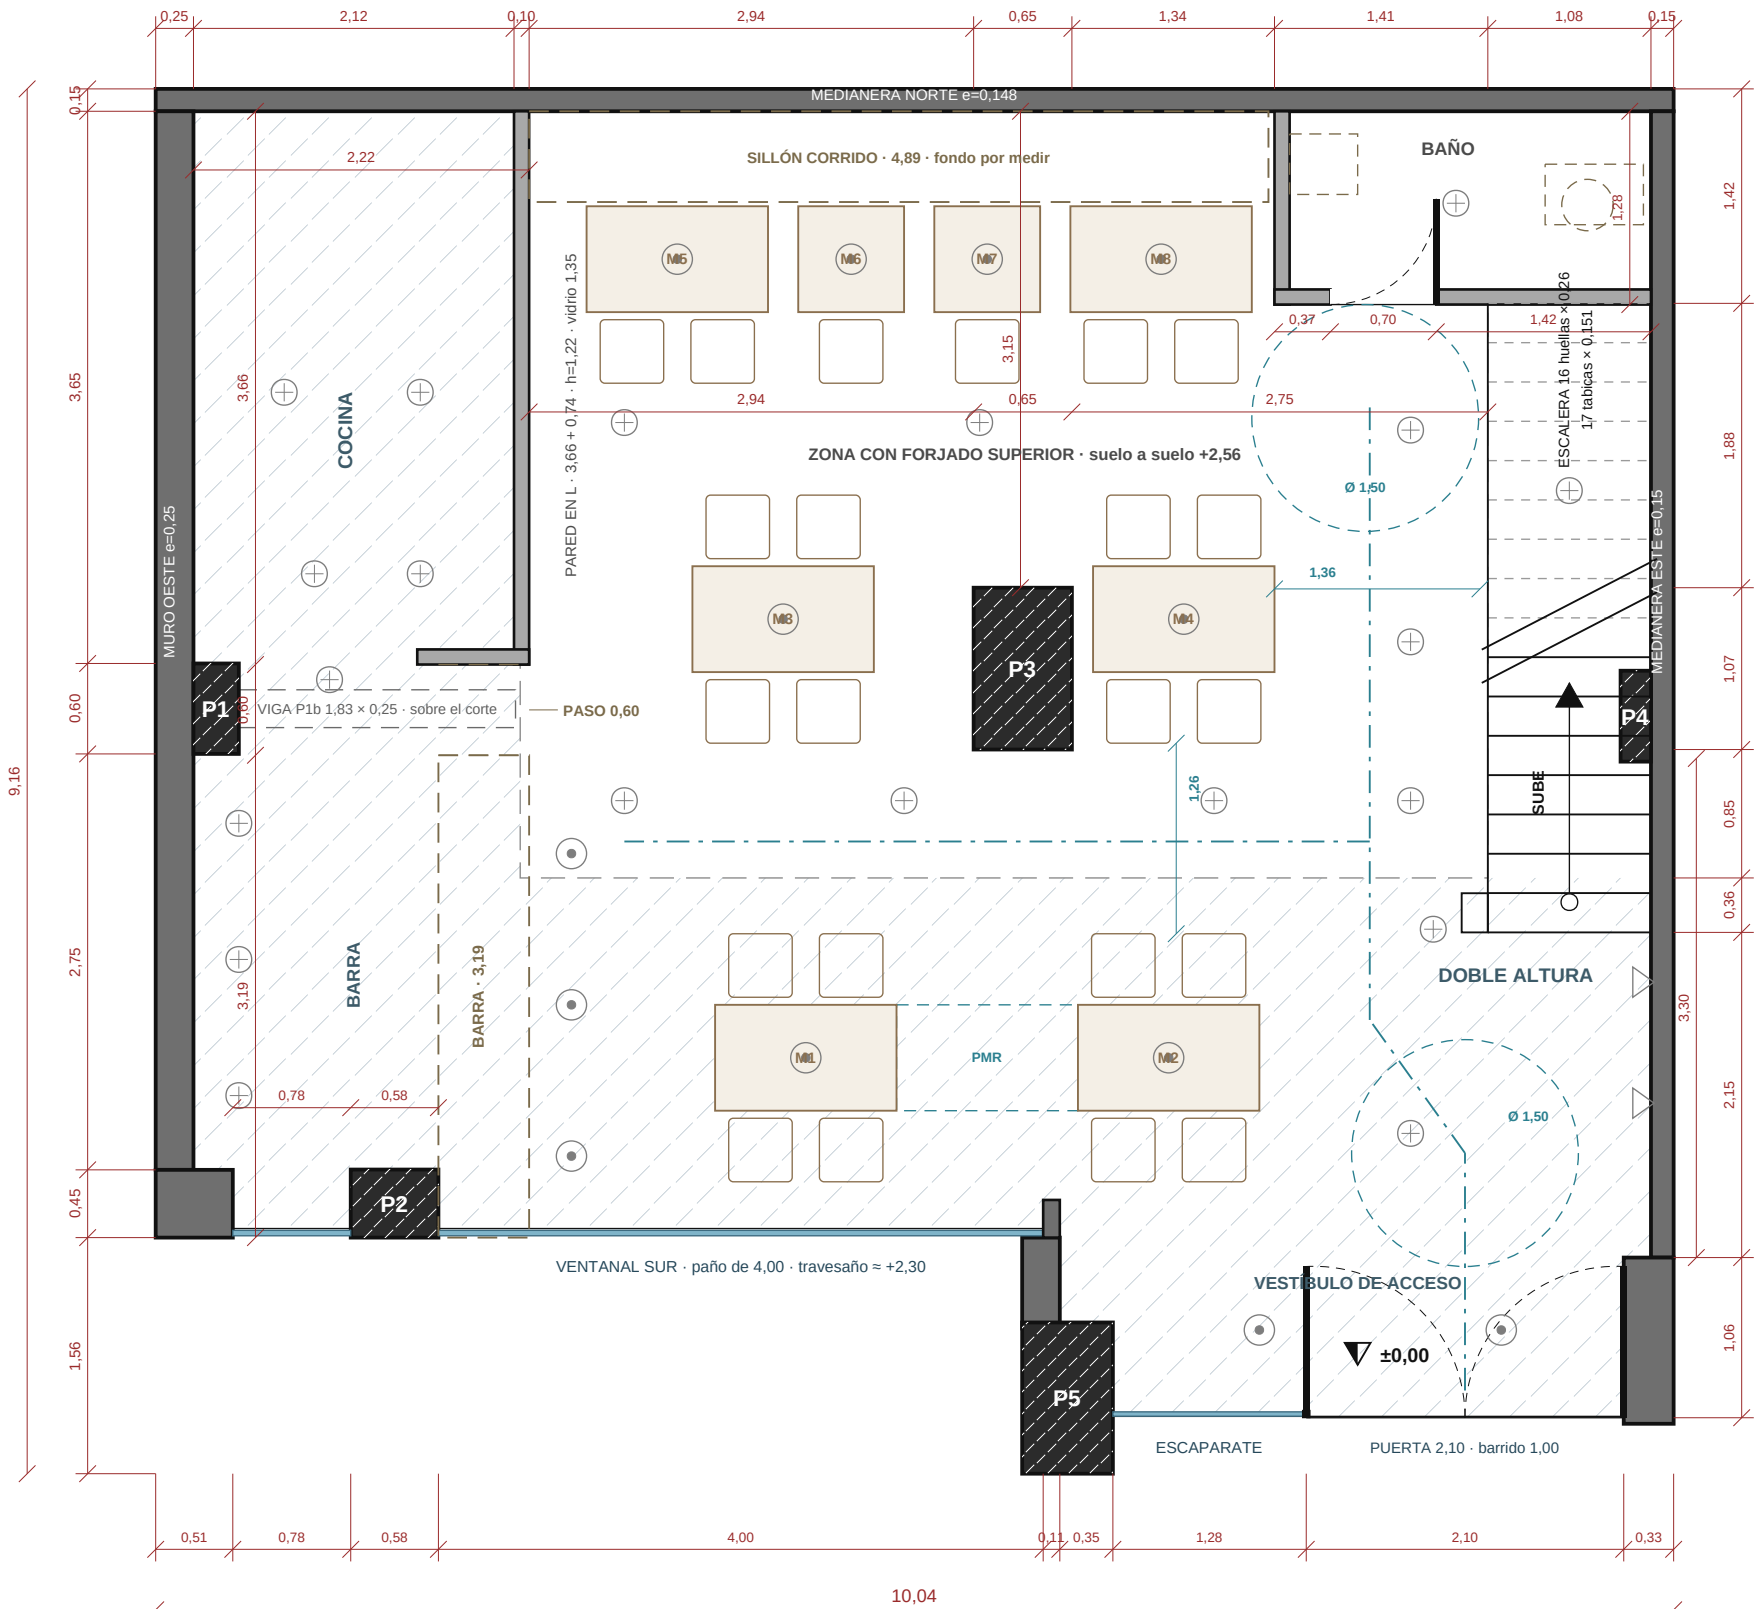

COMPROBAR EN OBRA Puntos en los que los vídeos del local no cuadran con el levantamiento, o que el levantamiento no recoge. Se dibuja el levantamiento por ser la única fuente acotada.

- Pared en L: en el segundo croquis termina en  $y=5,35$  (3,66 m) y la barra sube hasta 4,75 con el paso de 0,60 entre ambas. Antes se midió 4,22.
- Canto del forjado del altílo. Con 2,56 m de suelo a suelo, la altura libre de planta baja es 2,56 menos ese canto, no los 2,70 supuestos.
- P1b se dibuja como viga ( $1,83 \times 0,25$ ) y no como pilar: si fuera macizo hasta el suelo, la cocina no tendría entrada. Medir su intradós.
- Baño nuevo: tabiques de 0,10 y puerta de 0,70 tomados del croquis, sin medir. Comprobar que la puerta abre hacia dentro sin chocar.
- Posición de P3: el 3,15 de planta baja y el 1,90 de planta alta se llevan 0,15; el 2,94 y el 3,20 se llevan 0,26. Se usa la cadena de PB.
- Del P3 a la escalera se midió 2,35 y en el plano salen 2,75. Los 0,40 no cierran contra la medianera Este.
- Pasillo de cocina: 0,78 m frente a los frigoríficos (0,74 de fondo) y hasta 0,92 en el resto. Por debajo de 0,90 con permiso del cliente.
- Tabica de la escalera:  $2,56/17 = 0,151$  m. Contar los peldaños en obra.
- Máquinas: medidas de las fichas de makro.es según su buscador (la web bloquea el acceso directo). Sin dato: alto de la columna B4, 0,55 estimado.

# GRUPO SUMA

Reformas y proyectos · Málaga

## PROYECTO

Reforma integral de local de hostelería

## EMPLAZAMIENTO

Local en planta baja y altillo  
Málaga

## PLANO

PLANTA ALTA

Altillo +2,56 · estructura

## LEYENDA

- Muro de carga / medianera
- Pilar o machón de hormigón
- Tabiquería
- Barandilla de vidrio
- Mesas y sillas (medidas promedio)
- Punto de luz
- Vacío sobre planta baja

## SUPERFICIES Y ALTURAS

|                           |          |
|---------------------------|----------|
| Forjado de planta alta    | 33,74 m² |
| Altillo diáfano           | 26,17 m² |
| Aseo (lavabo + inodoro)   | 3,92 m²  |
| Almacén                   | 2,59 m²  |
| Nivel del forjado, medido | +2,56 m  |
| Puestos de cowork         | 14       |

## PILARES Y MACHONES (secciones en m)

|                                |             |
|--------------------------------|-------------|
| P1 Machón del muro Oeste       | 0,30 × 0,60 |
| P2 Pilastra del muro Sur       | 0,58 × 0,45 |
| P3 Pilar central               | 0,65 × 1,07 |
| P4 Machón de la medianera Este | 0,20 × 0,60 |
| P5 Pilar de fachada            | 0,60 × 1,00 |


## NOTAS

Cotas en metros, tomadas sobre el levantamiento.

Nivel del forjado +2,56, medido en obra.

El forjado del altillo no cubre todo el local: la franja sur y oeste es un vacío a doble altura.

Mesa de cowork 2,40 × 1,00 para 8 puestos y dos redondas de Ø 0,80 con 3 sillas. Medidas promedio.  
Un colgante por mesa y empotrados en el resto.

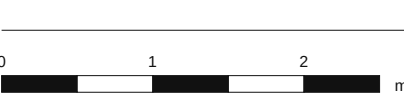

## ESCALA


1:50 (A3)

## FECHA

15 set. 2026

## PLANO

02 / 04

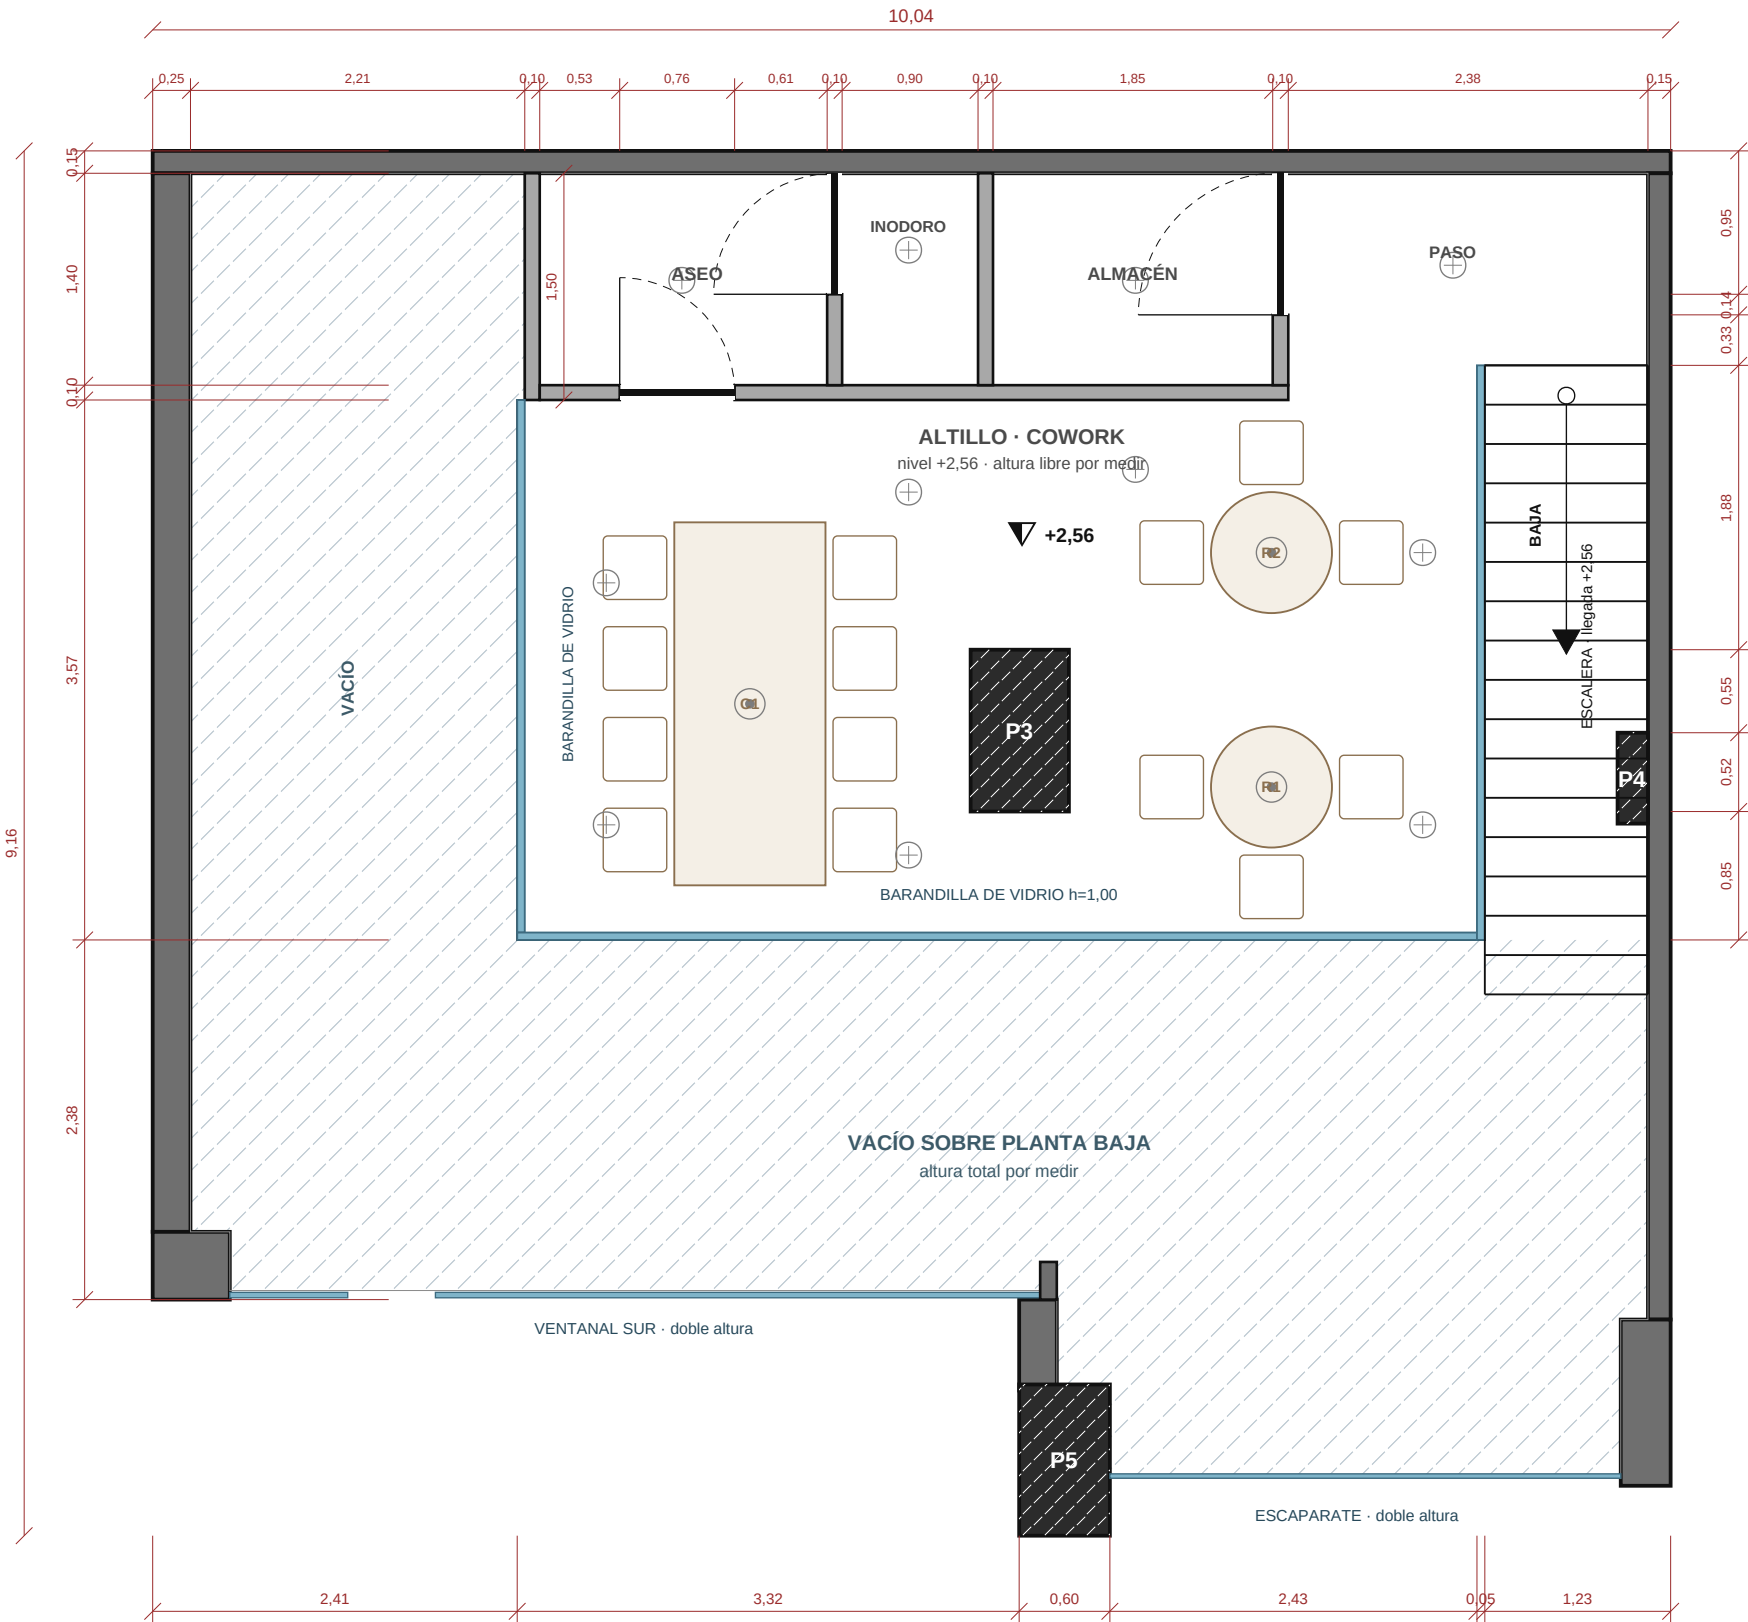

## COMPROBAR EN OBRA

Puntos en los que los vídeos del local no cuadran con el levantamiento, o que el levantamiento no recoge. Se dibuja el levantamiento por ser la única fuente acotada.

- Pared en L: en el segundo croquis termina en y=5,35 (3,66 m) y la barra sube hasta 4,75 con el paso de 0,60 entre ambas. Antes se midió 4,22.
- Canto del forjado del altillo. Con 2,56 m de suelo a suelo, la altura libre de planta baja es 2,56 menos ese canto, no los 2,70 supuestos.
- P1b se dibuja como viga (1,83 × 0,25) y no como pilar: si fuera macizo hasta el suelo, la cocina no tendría entrada. Medir su intradós.
- Baño nuevo: tabiques de 0,10 y puerta de 0,70 tomados del croquis, sin medir. Comprobar que la puerta abre hacia dentro sin chocar.
- Posición de P3: el 3,15 de planta baja y el 1,90 de planta alta se llevan 0,15; el 2,94 y el 3,20 se llevan 0,26. Se usa la cadena de PB.
- Del P3 a la escalera se midió 2,35 y en el plano salen 2,75. Los 0,40 no cierran contra la medianera Este.
- Pasillo de cocina: 0,78 m frente a los frigoríficos (0,74 de fondo) y hasta 0,92 en el resto. Por debajo de 0,90 con permiso del cliente.
- Tabica de la escalera: 2,56/17 = 0,151 m. Contar los peldaños en obra.
- Máquinas: medidas de las fichas de makro.es según su buscador (la web bloquea el acceso directo). Sin dato: alto de la columna B4, 0,55 estimado.

GRUPO SUMA

Reformas y proyectos · Málaga

PROYECTO  
Reforma integral de local de hostelería

EMPLAZAMIENTO  
Local en planta baja y altílo  
Málaga

PLANO  
EQUIPAMIENTO

Barra y cocina · productos Makro

LEYENDA

- Bancada o mueble bajo
- Equipo refrigerado
- Encimera o tabla corrida
- Aparato (trazos: bajo encimera)
- Tabla de madera
- Muro de carga / medianera

HOLGURAS Y ALTURAS



|                                   |        |
|-----------------------------------|--------|
| Pasillo de cocina, mínimo         | 0,78 m |
| Paso de servicio en barra         | 1,02 m |
| Entrada a la cocina, bajo la viga | 1,18 m |
| Altura de encimera                | 0,90 m |
| Borde inferior de la campana      | 2,00 m |

NOTAS

Cada máquina es un producto real de makro.es con sus medidas de ficha; la web bloquea el acceso directo, así que las medidas vienen de su buscador. Confirmar en la ficha antes de comprar.

Cocción corrida en la medianera Norte bajo campana de 2,00 sobre K1 a K4. Mesada refrigerada de una sola pieza (2,54, la más larga de Makro) en la pared en L; quedan 0,42 libres. La tabla cubre K6.

Pasillo de cocina de 0,78 a 0,92: por debajo de 0,90 con permiso del cliente. Muro Oeste: 3,01 de aparatos en los 3,05 que hay hasta P1.

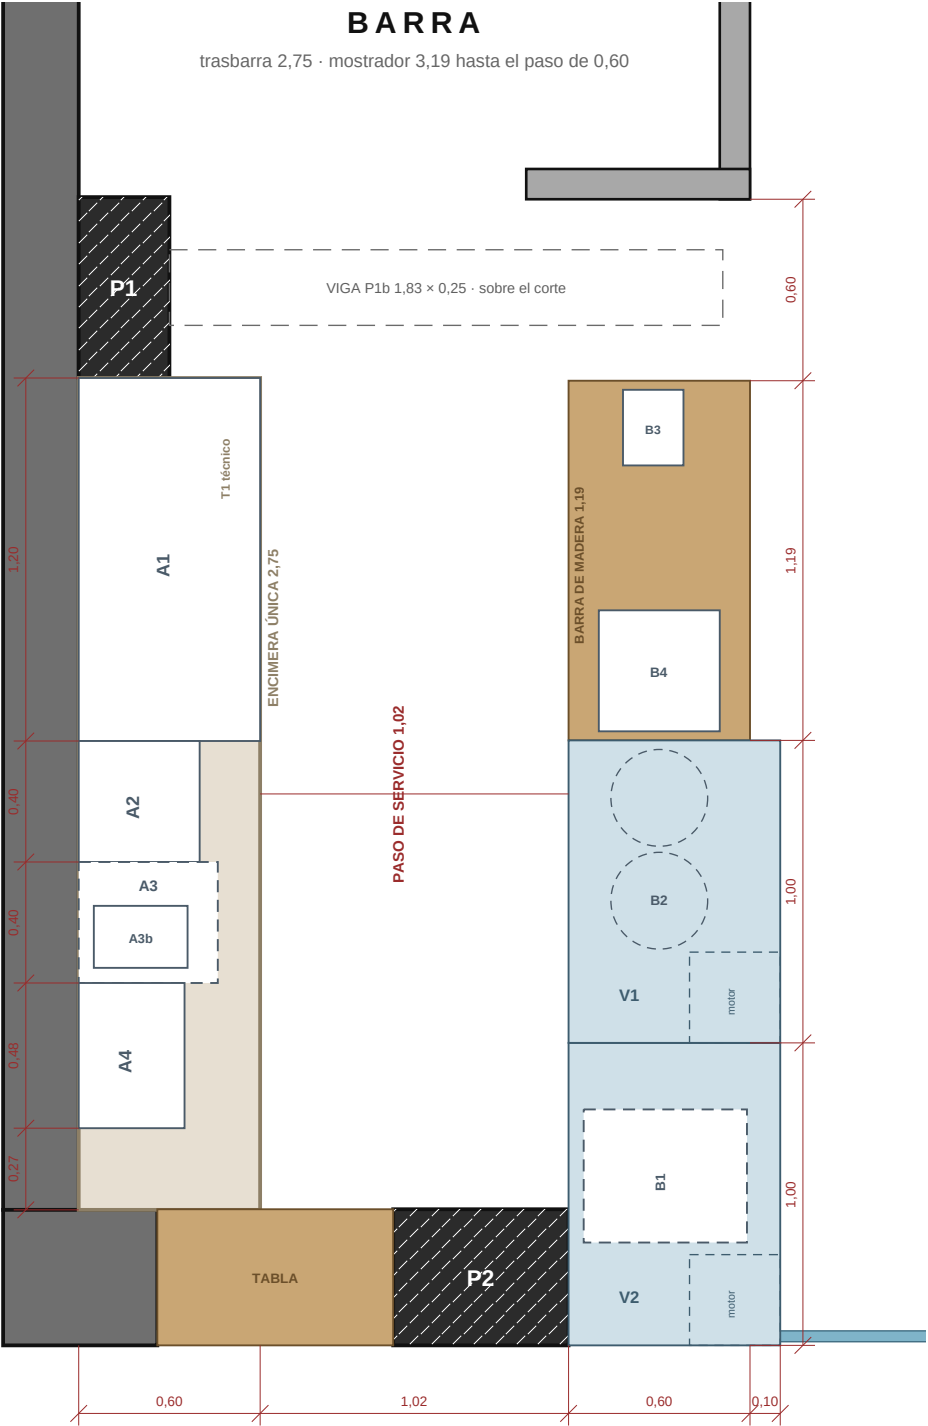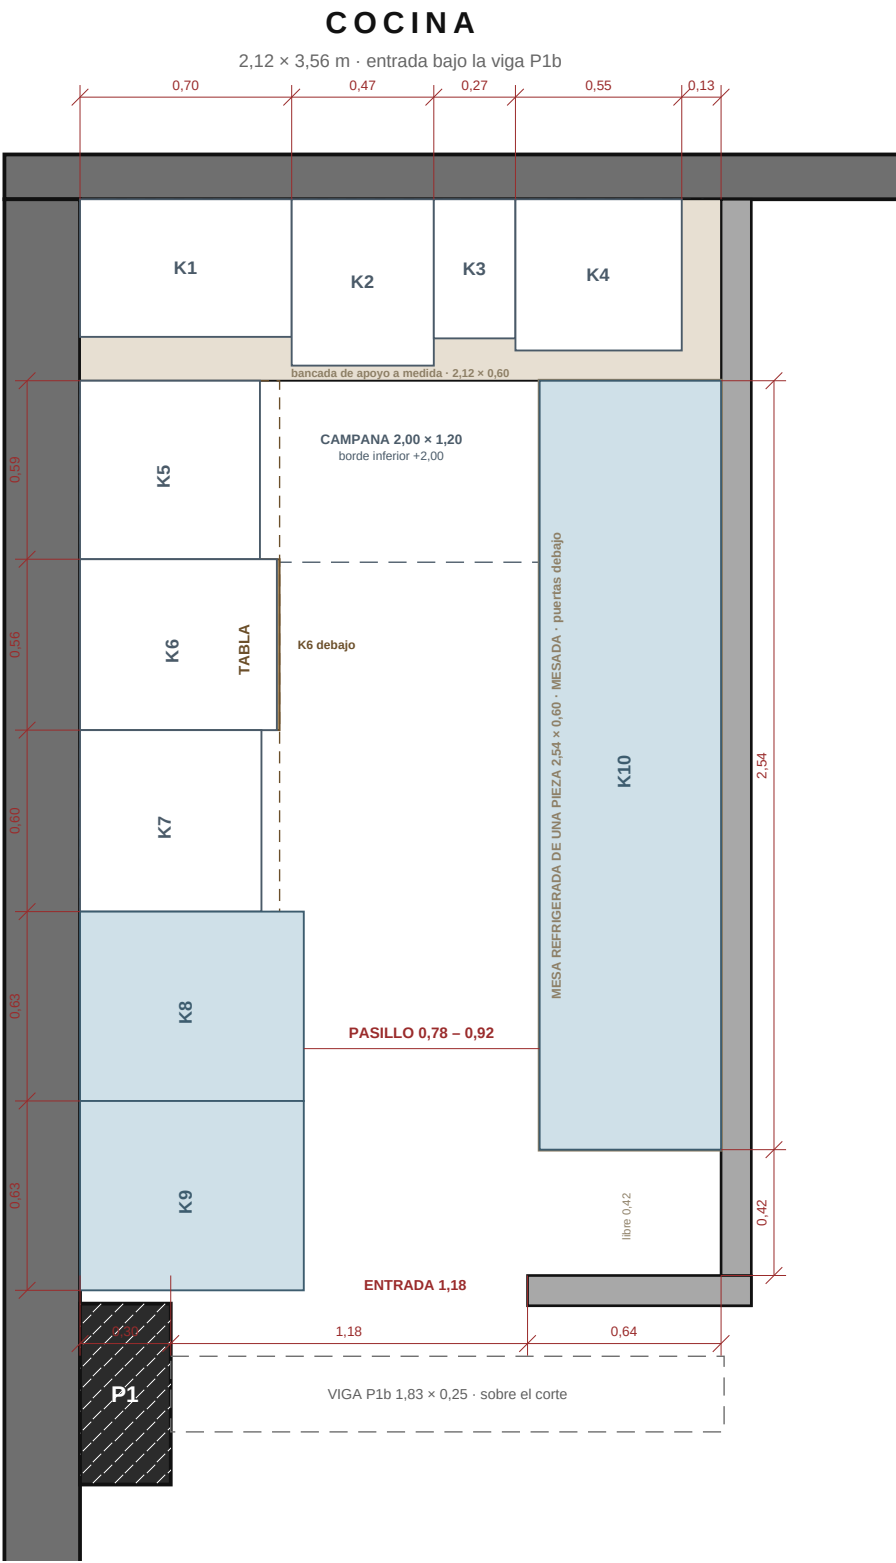

EQUIPAMIENTO · MAKRO

Ancho × fondo × alto en metros, de la ficha de makro.es. Vitrinas y cafetera ya compradas. Tablet y barriles con medida promedio. Enlaces en la lámina 04.

|     |                                                                                |                    |     |                                                                                |                    |
|-----|--------------------------------------------------------------------------------|--------------------|-----|--------------------------------------------------------------------------------|--------------------|
| K1  | Placa de inducción Bartscher, 2 zonas Ø230, 6 kW, 400 V                        | 0,70 × 0,46 × 0,12 | A1  | Cafetera (comprada), 2 grupos                                                  | 1,20 × 0,60 × 0,50 |
| K2  | Cocedor de pasta eléctrico METRO Professional GNC1008, 8 L, 4 cestos           | 0,47 × 0,55 × 0,38 | A2  | Lavamanos inox con grifo y pulsador de pedal, cuba Ø340                        | 0,40 × 0,40 × 0,85 |
| K3  | Freidora profesional 1 cuba de 7 L, eléctrica                                  | 0,27 × 0,46 × 0,37 | A3  | Fabricador de hielo Gastro M CT694, 28 kg/24 h (bajo encimera)                 | 0,40 × 0,46 × 0,67 |
| K4  | Plancha eléctrica Cleiton 50 cm, placa de 8 mm, sobremesa                      | 0,55 × 0,50 × 0,33 | A4  | Exprimidor de naranjas Mizumo Next Gen                                         | 0,48 × 0,35 × 0,73 |
| KC  | Campana extractora industrial recta, sin turbina, AISI-304 satinado, 2 × 1,2 m | 2,00 × 1,20 × 0,50 | A3b | Licuada industrial Sammic Li-240                                               | 0,20 × 0,31 × 0,36 |
| K5  | Horno de convección eléctrico industrial, 4 bandejas 45 × 33                   | 0,59 × 0,59 × 0,57 | V2  | Vitrina refrigerada (comprada), 1,00 × 0,70; debajo, lavavasos                 | 1,00 × 0,70 × 1,25 |
| K6  | Lavavajillas industrial ST500, cesta 50 × 50, bajo la tabla                    | 0,56 × 0,65 × 0,86 | V1  | Vitrina refrigerada (comprada), 1,00 × 0,70; debajo, barriles                  | 1,00 × 0,70 × 1,25 |
| K7  | Fregadero industrial Distform gama 600, 1 cubeta 50 × 40, con puerta, peto 105 | 0,60 × 0,60 × 0,85 | B1  | Lavavasos Elettrobar FAST 40, cesta 40 × 40 (bajo la vitrina V2)               | 0,44 × 0,54 × 0,67 |
| K8  | Armario refrigerado vertical Edenox APS-451 I, inox, 1 puerta, 395 L           | 0,63 × 0,74 × 1,86 | B2  | Barriles de cerveza de 30 L, Ø 0,32 (bajo la vitrina V1)                       | 0,32 × 0,32 × 0,60 |
| K9  | Armario refrigerado vertical Edenox APS-451 I, inox, 1 puerta, 395 L           | 0,63 × 0,74 × 1,86 | B3  | Caja: tablet sobre soporte                                                     | 0,25 × 0,20 × 0,25 |
| K10 | Mesa refrigerada Infrico 4 puertas, AISI-304, peto 100 mm, -2/+8 °C, 530 L     | 2,54 × 0,60 × 0,85 | B4  | Columna de cerveza en T de 3 grifos, bandeja 40 × 40 (no la hay de 2 en Makro) | 0,40 × 0,40 × 0,55 |

ESCALA

1:25 (A3)

FECHA

15 set. 2026

PLANO

03 / 04

LISTA DE EQUIPAMIENTO · MAKRO

Todo lo que hay que comprar para la barra y la cocina, con la ficha de makro.es de cada producto. Medidas en metros, ancho × fondo × alto. Los enlaces de la última columna son clicables en el PDF.

EQUIPOS DIBUJADOS EN LAS LÁMINAS 01 Y 03

| RÓTULO | PRODUCTO                                                                       | MEDIDAS            | DÓNDE VA                                                                    | FICHA EN MAKRO.ES   |
|--------|--------------------------------------------------------------------------------|--------------------|-----------------------------------------------------------------------------|---|
| K1     | Placa de inducción Bartscher, 2 zonas Ø230, 6 kW, 400 V                        | 0,70 × 0,46 × 0,12 | Cocina · cocción, medianera Norte, bajo la campana, 1º desde el Oeste       | <a href="https://www.makro.es/marketplace/product/623ef78b-af50-4e27-a2c5-b3a45089ba59">https://www.makro.es/marketplace/product/623ef78b-af50-4e27-a2c5-b3a45089ba59</a> |
| K2     | Cocedor de pasta eléctrico METRO Professional GNC1008, 8 L, 4 cestos           | 0,47 × 0,55 × 0,38 | Cocina · cocción, bajo la campana, 2º                                       | <a href="https://www.makro.es/marketplace/product/85f3fb44-3f09-463c-ab29-53822c8c1ce7">https://www.makro.es/marketplace/product/85f3fb44-3f09-463c-ab29-53822c8c1ce7</a> |
| K3     | Freidora profesional 1 cuba de 7 L, eléctrica                                  | 0,27 × 0,46 × 0,37 | Cocina · cocción, bajo la campana, 3º                                       | <a href="https://www.makro.es/marketplace/product/57e9d9ed-d483-4f88-a049-5597b3a7ad18">https://www.makro.es/marketplace/product/57e9d9ed-d483-4f88-a049-5597b3a7ad18</a> |
| K4     | Plancha eléctrica Cleiton 50 cm, placa de 8 mm, sobremesa                      | 0,55 × 0,50 × 0,33 | Cocina · cocción, bajo la campana, 4º, contra la pared en L                 | <a href="https://www.makro.es/marketplace/product/acd212b2-73a4-42bc-bea7-329d5ab4771d">https://www.makro.es/marketplace/product/acd212b2-73a4-42bc-bea7-329d5ab4771d</a> |
| KC     | Campana extractora industrial recta, sin turbina, AISI-304 satinado, 2 × 1,2 m | 2,00 × 1,20 × 0,50 | Cocina · campana mural corrida sobre K1 a K4, borde inferior a +2,00        | <a href="https://www.makro.es/marketplace/product/a8240770-cb5f-491b-926d-83b1e1e00a22">https://www.makro.es/marketplace/product/a8240770-cb5f-491b-926d-83b1e1e00a22</a> |
| K5     | Horno de convección eléctrico industrial, 4 bandejas 45 × 33                   | 0,59 × 0,59 × 0,57 | Cocina · muro Oeste, esquina Norte, sobre soporte                           | <a href="https://www.makro.es/marketplace/product/e3c35b3b-14d3-4e2b-a109-373a863ddff9">https://www.makro.es/marketplace/product/e3c35b3b-14d3-4e2b-a109-373a863ddff9</a> |
| K6     | Lavavajillas industrial ST500, cesta 50 × 50, bajo la tabla                    | 0,56 × 0,65 × 0,86 | Cocina · muro Oeste, bajo la tabla que enlaza fregadero y horno             | <a href="https://www.makro.es/marketplace/product/b6893f6e-6c55-499e-8e8b-4e246d107961">https://www.makro.es/marketplace/product/b6893f6e-6c55-499e-8e8b-4e246d107961</a> |
| K7     | Fregadero industrial Distform gama 600, 1 cubeta 50 × 40, con puerta, peto 105 | 0,60 × 0,60 × 0,85 | Cocina · muro Oeste, al Sur de la tabla (0,60 para que entren K8 y K9)      | <a href="https://www.makro.es/marketplace/product/3efac5b4-e702-4af6-9dd9-533709488190">https://www.makro.es/marketplace/product/3efac5b4-e702-4af6-9dd9-533709488190</a> |
| K8     | Armario refrigerado vertical Edenox APS-451 I, inox, 1 puerta, 395 L           | 0,63 × 0,74 × 1,86 | Cocina · muro Oeste, vertical, al Sur del fregadero                         | <a href="https://www.makro.es/marketplace/product/2e636462-1801-45f6-a3d8-15413909cb8c">https://www.makro.es/marketplace/product/2e636462-1801-45f6-a3d8-15413909cb8c</a> |
| K9     | Armario refrigerado vertical Edenox APS-451 I, inox, 1 puerta, 395 L           | 0,63 × 0,74 × 1,86 | Cocina · muro Oeste, vertical, contra P1                                    | <a href="https://www.makro.es/marketplace/product/2e636462-1801-45f6-a3d8-15413909cb8c">https://www.makro.es/marketplace/product/2e636462-1801-45f6-a3d8-15413909cb8c</a> |
| K10    | Mesa refrigerada Infrico 4 puertas, AISI-304, peto 100 mm, -2/+8 °C, 530 L     | 2,54 × 0,60 × 0,85 | Cocina · pared en L, de una pieza, como mesada; 0,42 libras junto al doblez | <a href="https://www.makro.es/marketplace/product/764bc52f-1287-4e08-89dc-c2e453dfea49">https://www.makro.es/marketplace/product/764bc52f-1287-4e08-89dc-c2e453dfea49</a> |
| A1     | Cafetera (comprada), 2 grupos                                                  | 1,20 × 0,60 × 0,50 | Barra · trasbarra, extremo Norte, sobre el módulo técnico T1                | ya comprado / medida promedio, sin ficha   |
| A2     | Lavamanos inox con grifo y pulsador de pedal, cuba Ø340                        | 0,40 × 0,40 × 0,85 | Barra · trasbarra, al Sur de la cafetera                                    | <a href="https://www.makro.es/marketplace/product/6105678f-3159-4172-a17a-f400760f0b35">https://www.makro.es/marketplace/product/6105678f-3159-4172-a17a-f400760f0b35</a> |
| A3     | Fabricador de hielo Gastro M CT694, 28 kg/24 h (bajo encimera)                 | 0,40 × 0,46 × 0,67 | Barra · trasbarra, bajo la encimera, al Sur del lavamanos                   | <a href="https://www.makro.es/marketplace/product/e3db53e1-8f64-4495-bb2c-59fe355a32e2">https://www.makro.es/marketplace/product/e3db53e1-8f64-4495-bb2c-59fe355a32e2</a> |
| A4     | Exprimidor de naranjas Mizumo Next Gen                                         | 0,48 × 0,35 × 0,73 | Barra · trasbarra, extremo Sur                                              | <a href="https://www.makro.es/marketplace/product/a7c3e878-0cdd-4f7e-b013-897ae4f6120d">https://www.makro.es/marketplace/product/a7c3e878-0cdd-4f7e-b013-897ae4f6120d</a> |
| A3b    | Licuadaora industrial Sammic Li-240                                            | 0,20 × 0,31 × 0,36 | Barra · trasbarra, sobre la encimera, encima de la hielera                  | <a href="https://www.makro.es/marketplace/product/2b8d9850-b422-4738-b716-c30da9857300">https://www.makro.es/marketplace/product/2b8d9850-b422-4738-b716-c30da9857300</a> |
| V2     | Vitrina refrigerada (comprada), 1,00 × 0,70; debajo, lavavasos                 | 1,00 × 0,70 × 1,25 | Barra · mostrador delantero, junto a P2 (Sur); lavavasos debajo             | ya comprado / medida promedio, sin ficha   |
| V1     | Vitrina refrigerada (comprada), 1,00 × 0,70; debajo, barriles                  | 1,00 × 0,70 × 1,25 | Barra · mostrador delantero, al Norte de V2; barriles debajo                | ya comprado / medida promedio, sin ficha   |
| B1     | Lavavasos Elettrobar FAST 40, cesta 40 × 40 (bajo la vitrina V2)               | 0,44 × 0,54 × 0,67 | Barra · bajo la vitrina V2                                                  | <a href="https://www.makro.es/marketplace/product/e858e346-8373-4e64-aa03-6f9a559e168e">https://www.makro.es/marketplace/product/e858e346-8373-4e64-aa03-6f9a559e168e</a> |
| B2     | Barriles de cerveza de 30 L, Ø 0,32 (bajo la vitrina V1)                       | 0,32 × 0,32 × 0,60 | Barra · bajo la vitrina V1                                                  | ya comprado / medida promedio, sin ficha   |
| B3     | Caja: tablet sobre soporte                                                     | 0,25 × 0,20 × 0,25 | Barra · barra de madera, extremo Norte, junto a la viga P1b                 | ya comprado / medida promedio, sin ficha   |
| B4     | Columna de cerveza en T de 3 grifos, bandeja 40 × 40 (no la hay de 2 en Makro) | 0,40 × 0,40 × 0,55 | Barra · barra de madera, extremo Sur                                        | <a href="https://www.makro.es/marketplace/product/f2d9d7ba-6f4f-4feb-b032-641cc4d828fe">https://www.makro.es/marketplace/product/f2d9d7ba-6f4f-4feb-b032-641cc4d828fe</a> |

ALTERNATIVAS CON LA MISMA FUNCIÓN · no dibujadas

| SUSTITUYE | PRODUCTO                                                                        | MEDIDAS            | DÓNDE VA                                                                     | FICHA EN MAKRO.ES   |
|-----------|---------------------------------------------------------------------------------|--------------------|------------------------------------------------------------------------------|---|
| K10       | Mesa refrigerada Vaiotec EASYLINE, inox, 4 puertas, GN 1/1, 553 L               | 2,23 × 0,70 × 0,85 | Cocina · pared en L, en lugar de K10; fondo 0,70 como la foto; 0,73 libras   | <a href="https://www.makro.es/marketplace/product/230e627d-7291-43e0-a2b4-ebb6fe783f27">https://www.makro.es/marketplace/product/230e627d-7291-43e0-a2b4-ebb6fe783f27</a> |
| K10       | METRO Professional GCC3100, inox, 3 puertas, 334 L (la de la foto, refrigerada) | 1,79 × 0,70 × 0,85 | Cocina · pared en L, en lugar de K10; deja 1,16 libras                       | <a href="https://www.makro.es/marketplace/product/176b30f1-81b0-4a52-916e-80722d9a9240">https://www.makro.es/marketplace/product/176b30f1-81b0-4a52-916e-80722d9a9240</a> |
| K8/K9     | Armario frigorífico ventilado 400 L, acero inoxidable (Diamond)                 | 0,63 × 0,74 × 1,93 | Cocina · muro Oeste, en lugar de K8 y K9; misma huella que el Edenox         | <a href="https://www.makro.es/marketplace/product/8969b667-b5cb-4e83-b599-3dd45c112547">https://www.makro.es/marketplace/product/8969b667-b5cb-4e83-b599-3dd45c112547</a> |
| K8/K9     | Armario refrigerado AR400L Clima Hostelería, lacado blanco (no inox), 360 L     | 0,60 × 0,61 × 1,87 | Cocina · muro Oeste, en lugar de K8 y K9; con éste cabe el fregadero de 0,70 | <a href="https://www.makro.es/marketplace/product/d48c3c0c-7975-4c22-89c7-64676c23681f">https://www.makro.es/marketplace/product/d48c3c0c-7975-4c22-89c7-64676c23681f</a> |
| K7        | Fregadero Royal Catering, 1 cubeta 50 × 50, 70 × 70 (alto sin dato en ficha)    | 0,70 × 0,70 × 0,85 | Cocina · muro Oeste, en lugar de K7; sólo con los frigoríficos AR400L        | <a href="https://www.makro.es/marketplace/product/987fd316-3c44-48e2-a628-d88809ed245c">https://www.makro.es/marketplace/product/987fd316-3c44-48e2-a628-d88809ed245c</a> |

A MEDIDA · no se compran en Makro

- Bancada de apoyo de la línea de cocción: 2,12 × 0,60, acero inoxidable.
- Tabla de madera sobre el lavavajillas K6, del fregadero al horno: 0,57 × 0,66.
- Encimera única de la trasbarra: 2,75 × 0,60.
- Barra de madera del mostrador delantero: 1,19 × 0,60.
- Tabla de P2 al muro: 0,78 × 0,45.
- Módulo técnico T1 bajo la cafetera: 0,60 de ancho.

VERIFICACIÓN DE LOS ENLACES

makro.es responde 403 a cualquier acceso desde un servidor (curl, Playwright o un navegador en la nube), así que las fichas no se pueden abrir desde el entorno de trabajo. Cada enlace se verificó buscando su identificador con el buscador restringido a makro.es: los 21 devuelven exactamente su URL con el título del producto (LISTA\_MAKRO.md). Precios y stock no se han podido leer con fiabilidad: confirmar en la ficha antes de comprar. Si un enlace dejara de funcionar, buscar el título literal de la ficha en makro.es.

GRUPO SUMA

Reformas y proyectos · Málaga

PROYECTO

Reforma integral de local de hostelería

EMPLAZAMIENTO

Local en planta baja y altillo Málaga

PLANO

EQUIPAMIENTO

Lista de compra · enlaces a makro.es

RESUMEN

|                             |                       |
|-----------------------------|-----------------------|
| Fichas distintas de Makro   | 16                    |
| Unidades a comprar en Makro | 17                    |
| Ya comprado                 | cafetera y 2 vitrinas |
| Medida promedio             | barriles y tablet     |
| A medida                    | 6 elementos           |

NOTAS

Medidas ancho × fondo × alto en metros, tomadas de la ficha de makro.es. Los enlaces de la última columna son clicables en el PDF; en papel, copiar la dirección o buscar el título en makro.es. Vitrinas y cafetera ya compradas, con las medidas del cliente. Barriles y tablet con medida promedio. Confirmar precio y stock antes de comprar.

|            |              |         |
|------------|--------------|---------|
| ESCALA     | FECHA        | PLANO   |
| sin escala | 15 set. 2026 | 04 / 04 |