

GRUPO SUMA

Reformas y proyectos · Málaga

PROYECTO

Reforma integral de local de hostelería

EMPLAZAMIENTO

Local en planta baja y attillo Málaga

PLANO

PLANTA BAJA

Estado actual · estructura

LEYENDA

- Muro de carga / medianera
- Pilar o machón de hormigón
- Carpintería acristalada
- Espacio de doble altura
- Forjado y viga sobre el corte
- Punto de luz s/ proyecto

SUPERFICIES Y ALTURAS

Planta baja, dentro de muros	75,63 m²
Zona de doble altura	37,80 m²
Altura libre bajo forjado	2,70 m
Altura en doble altura	5,50 m
Acristalamiento de fachada	≈ 4,70 m

PILARES Y MACHONES (secciones en m)

P1 Machón del muro Oeste	0,37 × 0,60
P2 Pilastra del muro Sur	0,60 × 0,30
P3 Pilar central	0,60 × 0,90
P4 Machón de la medianera Este	0,20 × 0,60
P5 Pilar de fachada	0,50 × 0,96


NOTAS

Cotas en metros, tomadas sobre el levantamiento.

Plano de estructura: no se representa mobiliario ni equipamiento. Cota de referencia ±0,00 en el pavimento de planta baja.

Sección horizontal a 1,20 m sobre el pavimento.

Los puntos de luz proceden del proyecto de reforma, no están replanteados en obra.

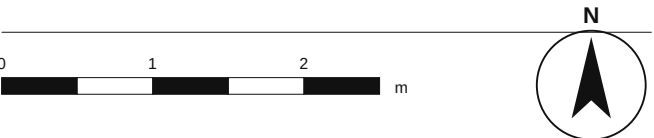

ESCALA

1:50 (A3)

FECHA

12 set. 2026

PLANO

01 / 02

