

GRUPO SUMA

Reformas y proyectos · Málaga

PROYECTO
Reforma integral de local de hostelería

EMPLAZAMIENTO
Local en planta baja y altílo
Málaga

PLANO
EQUIPAMIENTO

Barra y cocina · productos Makro

LEYENDA

- Bancada o mueble bajo
- Equipo refrigerado
- Encimera o tabla corrida
- Aparato (trazos: bajo encimera)
- Tabla de madera
- Muro de carga / medianera

HOLGURAS Y ALTURAS



Pasillo de cocina, mínimo	0,77 m
Paso de servicio en barra	1,02 m
Entrada a la cocina, bajo la viga	1,18 m
Altura de encimera	0,90 m
Borde inferior de la campana	2,00 m

NOTAS

Cada máquina es un producto real de makro.es con sus medidas de ficha; la web bloquea el acceso directo, así que las medidas vienen de su buscador. Confirmar en la ficha antes de comprar.

Cocción corrida en la medianera Norte bajo campana de 2,00; con la pared en L de 4,22 la cocina gana 0,62 m y la barra los pierde.

Pasillo de cocina de 0,77 a 0,82: por debajo de 0,90 con permiso del cliente. El frigorífico K9 topa con P1 (ajuste de 4 mm).

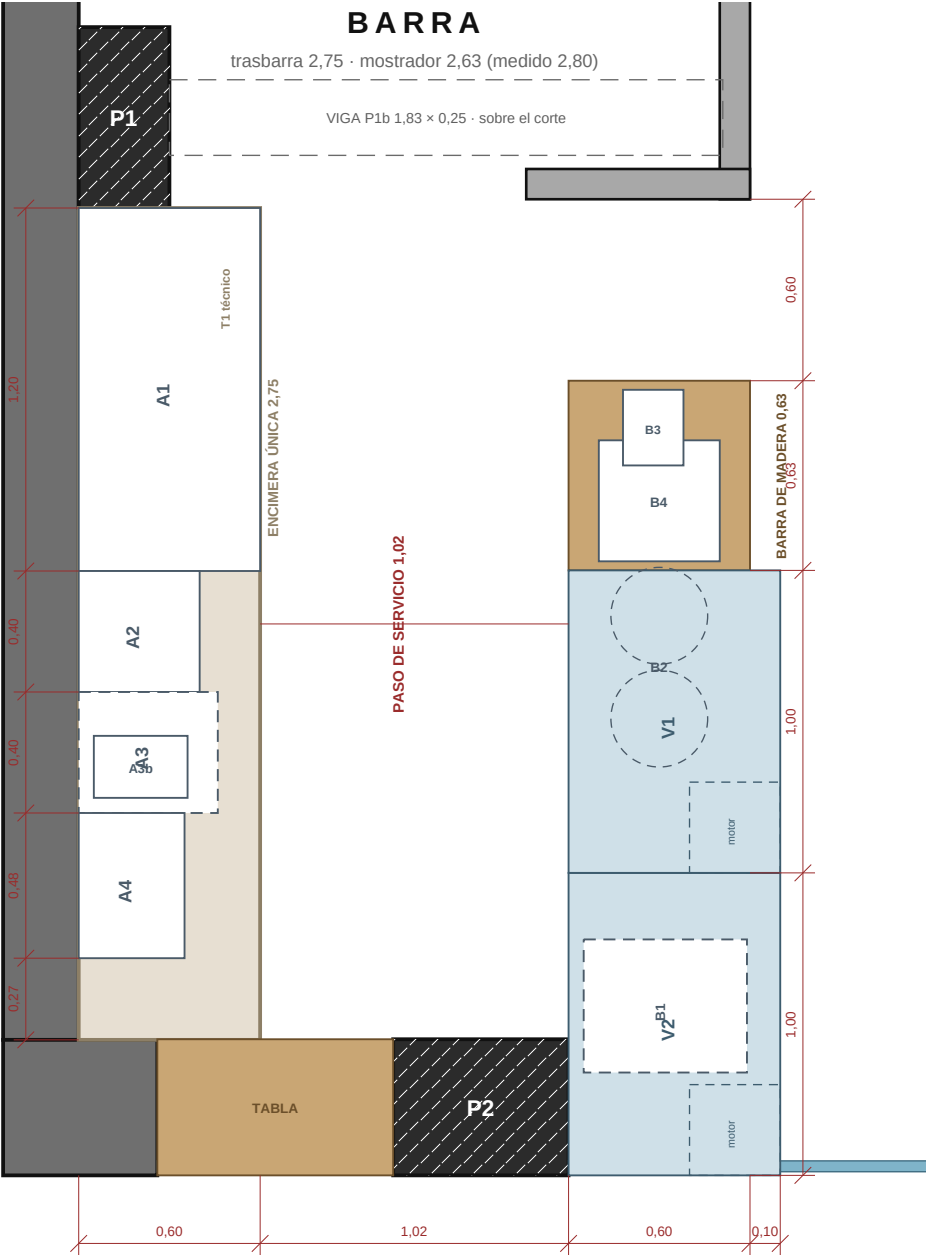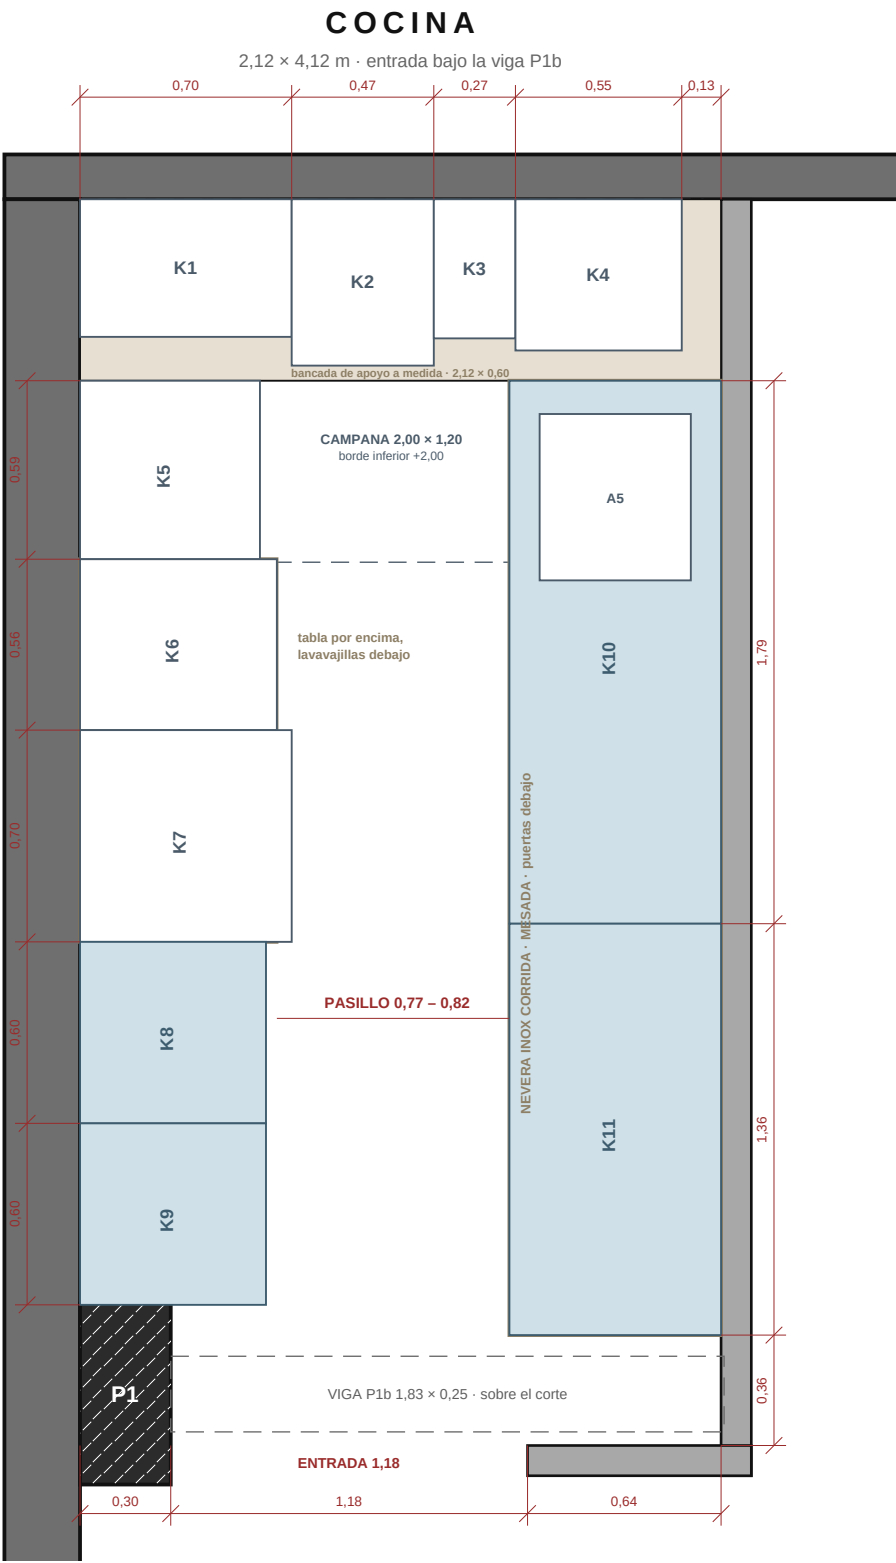

EQUIPAMIENTO · MAKRO

Ancho × fondo × alto en metros, de la ficha de makro.es. Vitrinas y cafetera ya compradas. Cortadora, tablet y barriles con medida promedio.

K1	Placa de inducción Bartscher, 2 zonas Ø230, 6 kW, 400 V	0,70 × 0,46 × 0,12	A5	Cortadora de fiambre (medida promedio)	0,55 × 0,50 × 0,45
K2	Cocedor de pasta eléctrico METRO Professional GNC1008, 8 L, 4 cestos	0,47 × 0,55 × 0,38	A1	Cafetera (comprada), 2 grupos	1,20 × 0,60 × 0,50
K3	Freidora profesional 1 cuba de 7 L, eléctrica	0,27 × 0,46 × 0,37	A2	Lavamanos inox con grifo y pulsador de pedal, cuba Ø340	0,40 × 0,40 × 0,85
K4	Plancha eléctrica Cleiton 50 cm, placa de 8 mm, sobremesa	0,55 × 0,50 × 0,33	A3	Fabricador de hielo Gastro M CT694, 28 kg/24 h (bajo encimera)	0,40 × 0,46 × 0,67
KC	Campana extractora industrial recta, sin turbina, AISI-304 satinado, 2000 × 12	2,00 × 1,20 × 0,50	A4	Exprimidor de naranjas Mizumo Next Gen	0,48 × 0,35 × 0,73
K5	Horno de convección eléctrico industrial, 4 bandejas 45 × 33	0,59 × 0,59 × 0,57	A3b	Licuada industrial Sammic Li-240	0,20 × 0,31 × 0,36
K6	Lavavajillas industrial ST500, cesta 50 × 50, bajo la tabla	0,56 × 0,65 × 0,83	V2	Vitrina refrigerada (comprada), 1,00 × 0,70; debajo, lavavasos	1,00 × 0,70 × 1,25
K7	Fregadero industrial Royal Catering, 1 cubeta 50 × 50, 70 × 70	0,70 × 0,70 × 0,85	V1	Vitrina refrigerada (comprada), 1,00 × 0,70; debajo, barriles	1,00 × 0,70 × 1,25
K8	Armario refrigerado vertical AR400L Clima Hostelería, inox, 360 L	0,60 × 0,61 × 1,87	B1	Lavavasos Elettrobar FAST 40, cesta 40 × 40 (bajo la vitrina V2)	0,44 × 0,54 × 0,67
K9	Armario refrigerado vertical AR400L Clima Hostelería, inox, 360 L	0,60 × 0,61 × 1,87	B2	Barriles de cerveza de 30 L, Ø 0,32 (bajo la vitrina V1)	0,32 × 0,32 × 0,60
K10	Mesa refrigerada METRO Professional GCC3100, inox, 3 puertas, 334 L	1,79 × 0,70 × 0,85	B3	Caja: tablet sobre soporte	0,25 × 0,20 × 0,25
K11	Mesa refrigerada bajo mostrador, 2 puertas, ventilada, mural	1,36 × 0,70 × 0,85	B4	Columna de cerveza de 2 grifos (Makro sólo lista la de 3, bandeja 40 × 40)	0,40 × 0,40 × 0,55

ESCALA

1:25 (A3)

FECHA

15 set. 2026

PLANO

03 / 03