

PROYECTO

Reforma integral de local de hostelería

EMPLAZAMIENTO

Local en planta baja y altillo Málaga

PLANO

PLANTA BAJA

Estado actual · estructura

LEYENDA

- Muro de carga / medianera
- Pilar o machón de hormigón
- Pared en L nueva (apoyo del vidrio)
- Carpintería acristalada
- Espacio de doble altura
- Forjado sobre el corte
- Reserva de espacio del cliente
- Mesas y sillas (medidas promedio)
- Punto de luz: colgante / empotrado

SUPERFICIES Y ALTURAS


Planta baja, dentro de muros	75,63 m²
Zona de doble altura	37,80 m²
Suelo a suelo, medido en obra	2,56 m
Altura libre bajo forjado	2,56 – canto
Pared en L, altura	1,22 m
Plazas sentadas en planta baja	32
Acristalamiento de fachada	≈ 4,70 m

PILARES Y MACHONES (secciones en m)


P1 Machón del muro Oeste	0,30 × 0,60
P2 Pilastra del muro Sur	0,58 × 0,45
P3 Pilar central	0,65 × 1,07
P4 Machón de la medianera Este	0,20 × 0,60
P5 Pilar de fachada	0,60 × 1,00

NOTAS

Cotas en metros. Las de los pilares, la pared en L, el ventanal y la puerta están medidas en obra (revisión del 14 set. 2026); el resto procede del levantamiento previo.
Cota de referencia ±0,00 en el pavimento de planta baja. Sección horizontal a 1,20 m.
Mesas con medidas promedio (doble 0,70 × 0,70; cuádruple 1,20 × 0,70). Puntos de luz replanteados sobre el mobiliario: un colgante por mesa, tres sobre la barra y empotrados en pasillos y cocina.
El equipamiento de barra y cocina va en la lámina 03.

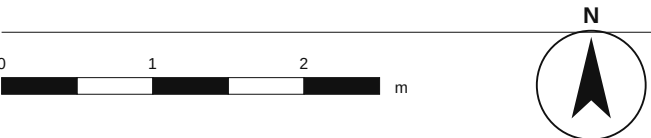

ESCALA	FECHA	PLANO
1:50 (A3)	15 set. 2026	01 / 03

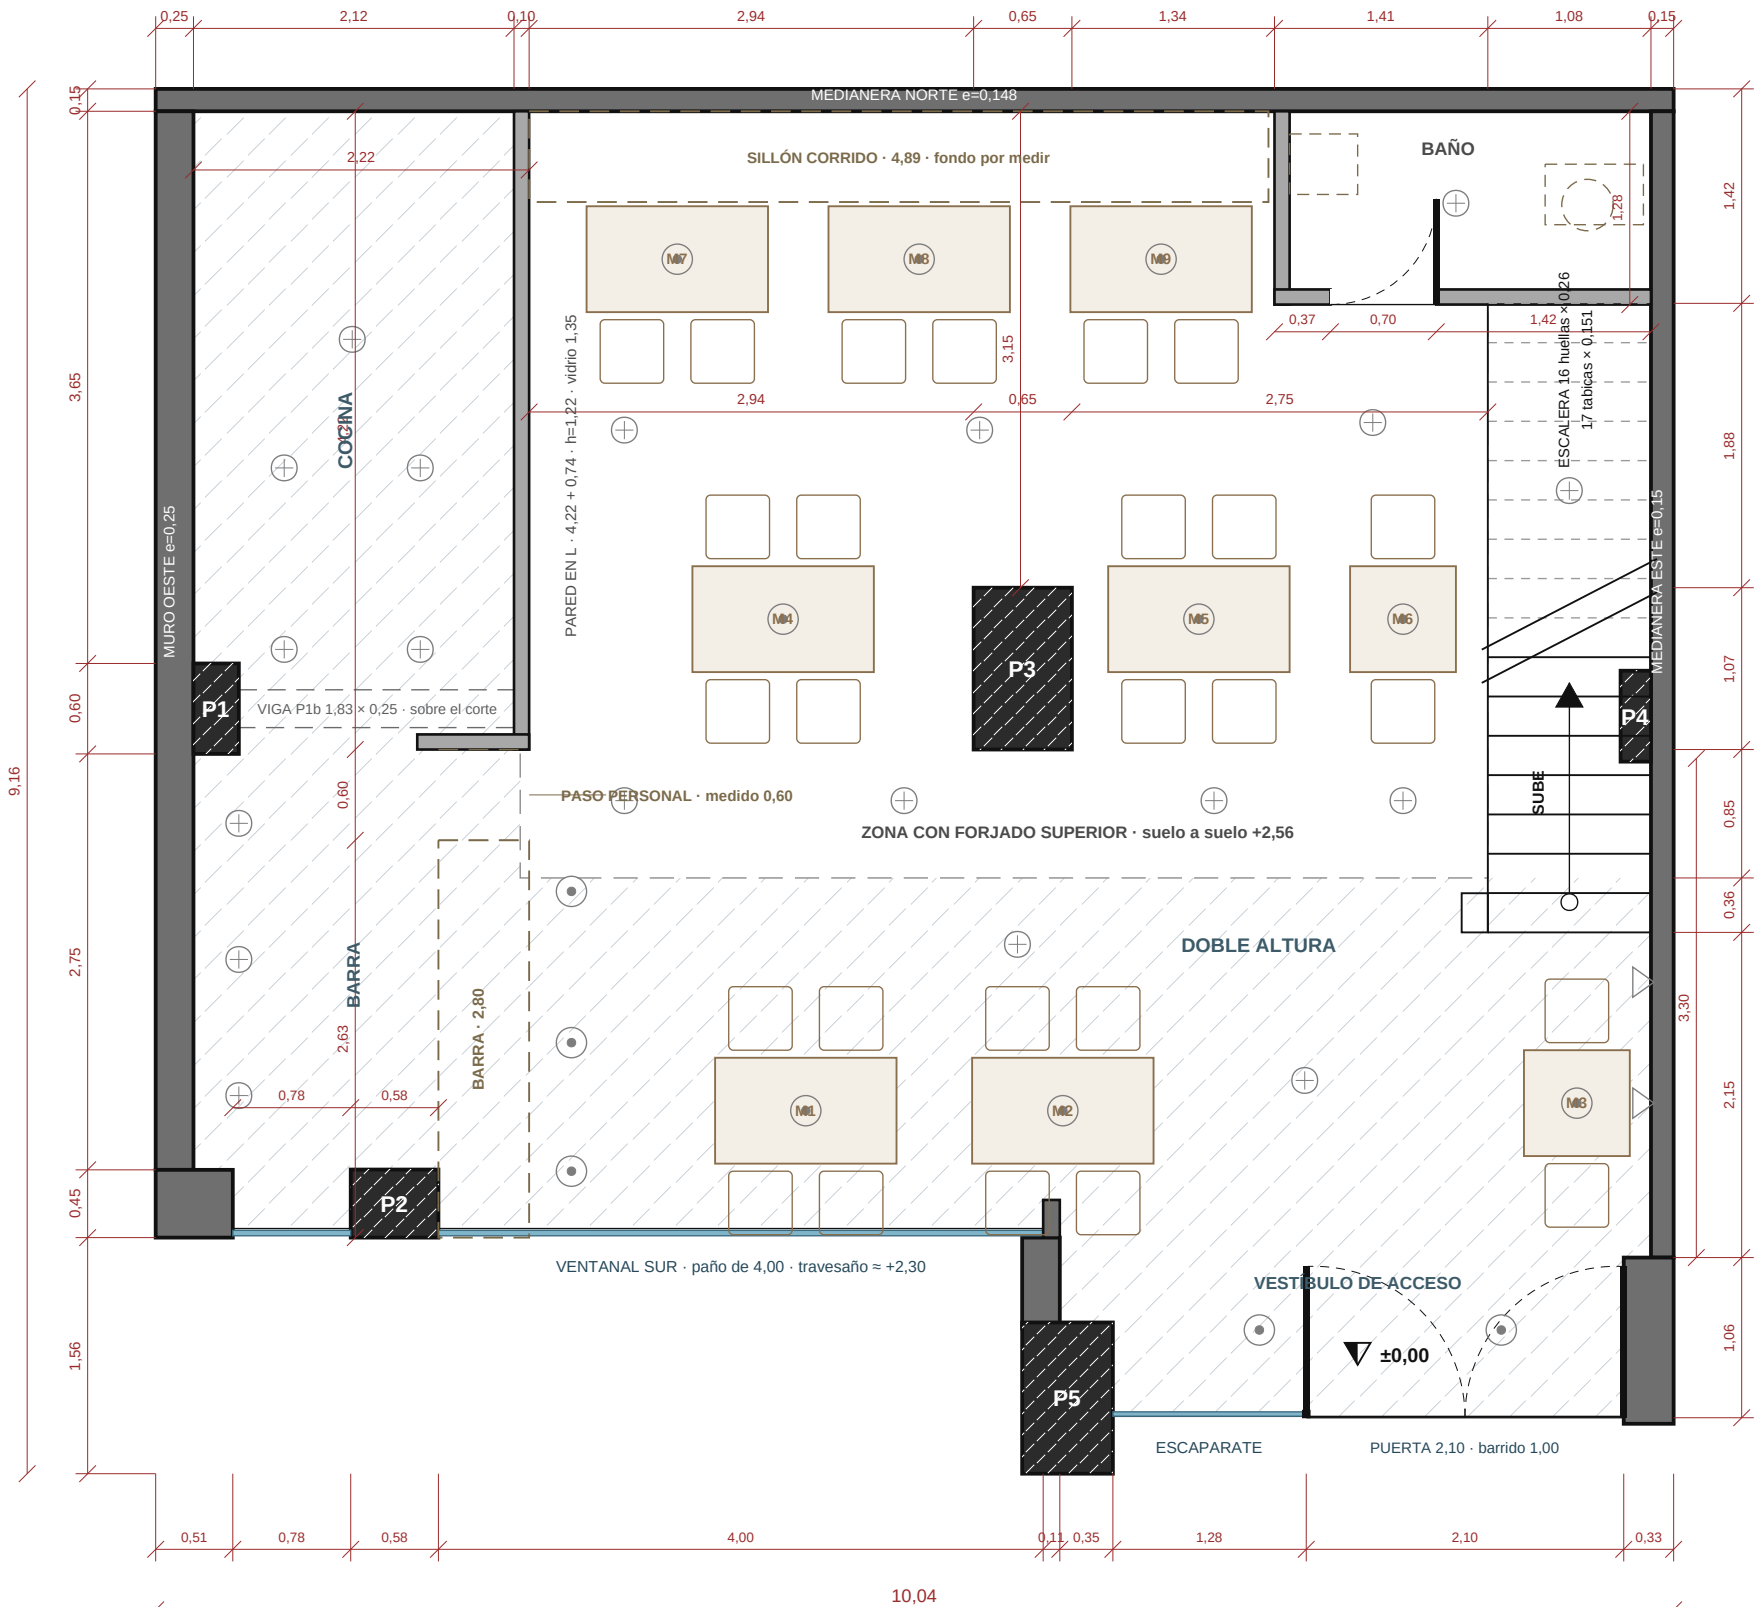

COMPROBAR EN OBRA Puntos en los que los vídeos del local no cuadran con el levantamiento, o que el levantamiento no recoge. Se dibuja el levantamiento por ser la única fuente acotada.

- Barra: medida 2,80 y dibujada 2,63, porque entre la pared en L de 4,22, el paso de 0,60 y el ventanal sólo quedan 2,63. Los 0,17 no cierran.
- Canto del forjado del altillo. Con 2,56 m de suelo a suelo, la altura libre de planta baja es 2,56 menos ese canto, no los 2,70 supuestos.
- P1b se dibuja como viga (1,83 × 0,25) y no como pilar: si fuera macizo hasta el suelo, la cocina no tendría entrada. Medir su intradós.
- Baño nuevo: tabiques de 0,10 y puerta de 0,70 tomados del croquis, sin medir. Comprobar que la puerta abre hacia dentro sin chocar.
- Posición de P3: el 3,15 de planta baja y el 1,90 de planta alta se llevan 0,15; el 2,94 y el 3,20 se llevan 0,26. Se usa la cadena de PB.
- Del P3 a la escalera se midió 2,35 y en el plano salen 2,75. Los 0,40 no cierran contra la medianera Este.
- Pasillo de cocina: 0,77 m en el lavavajillas (0,651 de fondo) y 0,82 en el resto. Por debajo de 0,90 con permiso del cliente.
- Tabica de la escalera: 2,56/17 = 0,151 m. Contar los peldaños en obra.
- Máquinas: medidas de las fichas de makro.es tal y como las indexa su buscador; la web bloquea el acceso directo. Confirmar en la ficha.