

PROYECTO

Reforma integral de local de hostelería

EMPLAZAMIENTO

Local en planta baja y altílo Málaga

PLANO

PLANTA BAJA

Estado actual · estructura

LEYENDA

- Muro de carga / medianera
- Pilar o machón de hormigón
- Pared en L nueva (apoyo del vidrio)
- Carpintería acristalada
- Espacio de doble altura
- Forjado sobre el corte
- Reserva de espacio del cliente
- Mesas y sillas (medidas promedio)
- Punto de luz: colgante / empotrado

SUPERFICIES Y ALTURAS


Planta baja, dentro de muros	75,63 m²
Zona de doble altura	37,80 m²
Suelo a suelo, medido en obra	2,56 m
Altura libre bajo forjado	2,56 – canto
Pared en L, altura	1,22 m
Plazas sentadas en planta baja	32
Acristalamiento de fachada	≈ 4,70 m

PILARES Y MACHONES (secciones en m)


P1 Machón del muro Oeste	0,30 × 0,60
P2 Pilastra del muro Sur	0,58 × 0,45
P3 Pilar central	0,65 × 1,07
P4 Machón de la medianera Este	0,20 × 0,60
P5 Pilar de fachada	0,60 × 1,00

NOTAS

Cotas en metros. Las de los pilares, la pared en L, el ventanal y la puerta están medidas en obra (revisión del 14 set. 2026); el resto procede del levantamiento previo.
Cota de referencia ±0,00 en el pavimento de planta baja. Sección horizontal a 1,20 m.
Mesas con medidas promedio (doble 0,70 × 0,70; cuádruple 1,20 × 0,70). Puntos de luz replanteados sobre el mobiliario: un colgante por mesa, tres sobre la barra y empotrados en pasillos y cocina.
El equipamiento de barra y cocina va en la lámina 03.

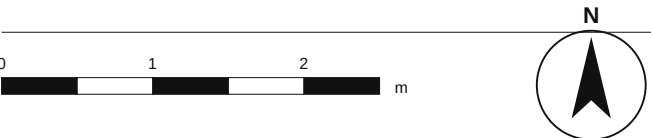

ESCALA	FECHA	PLANO
1:50 (A3)	15 set. 2026	01 / 03

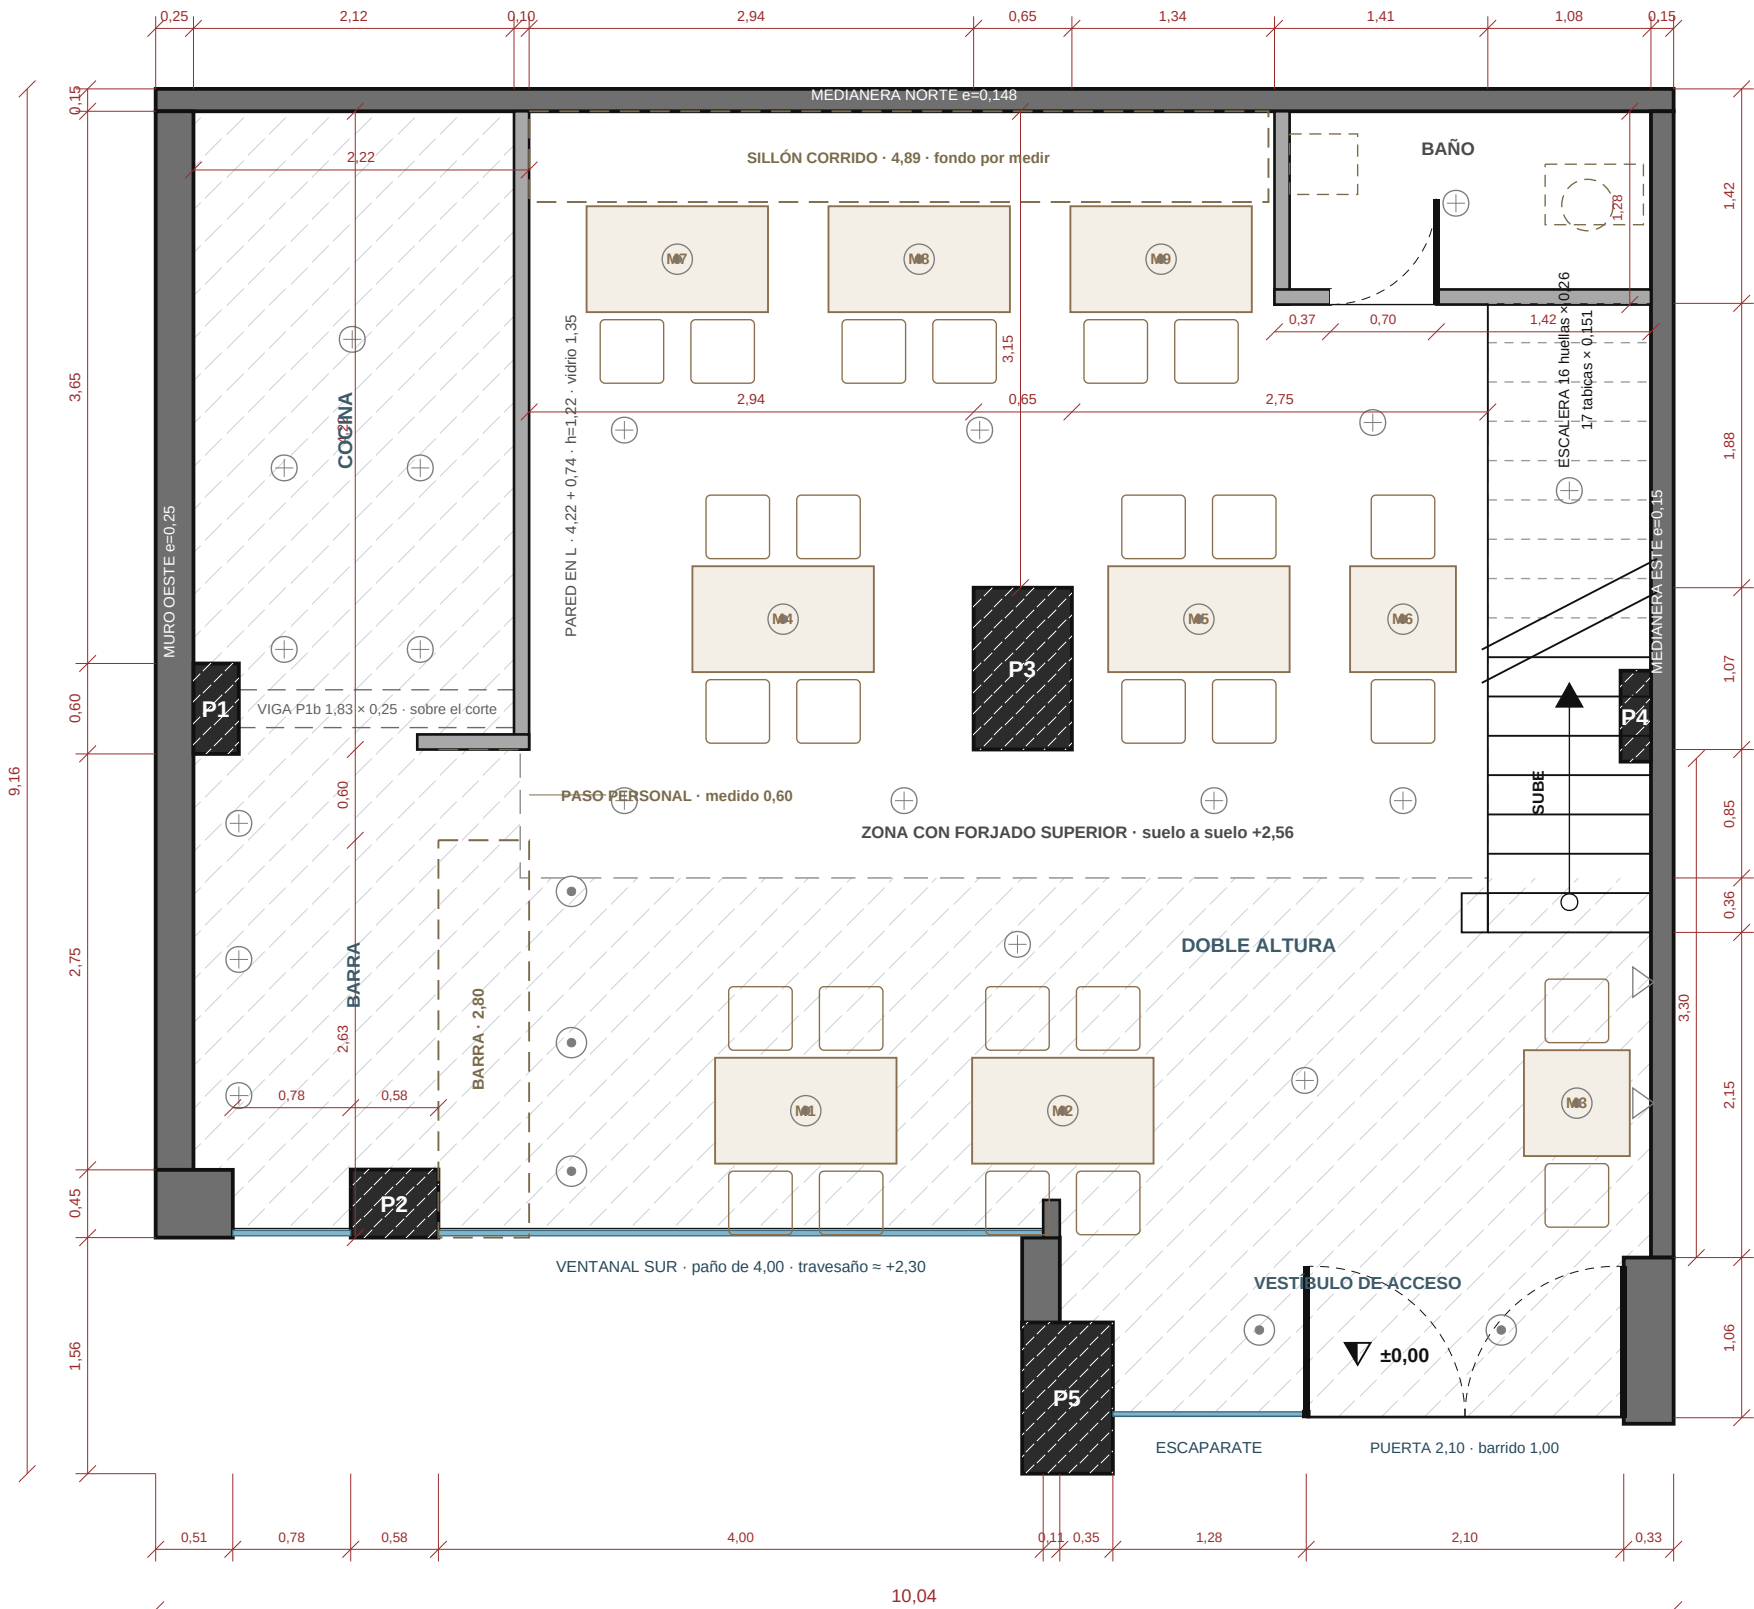

COMPROBAR EN OBRA Puntos en los que los vídeos del local no cuadran con el levantamiento, o que el levantamiento no recoge. Se dibuja el levantamiento por ser la única fuente acotada.

- Barra: medida 2,80 y dibujada 2,63, porque entre la pared en L de 4,22, el paso de 0,60 y el ventanal sólo quedan 2,63. Los 0,17 no cierran.
- Canto del forjado del altílo. Con 2,56 m de suelo a suelo, la altura libre de planta baja es 2,56 menos ese canto, no los 2,70 supuestos.
- P1b se dibuja como viga (1,83 × 0,25) y no como pilar: si fuera macizo hasta el suelo, la cocina no tendría entrada. Medir su intradós.
- Baño nuevo: tabiques de 0,10 y puerta de 0,70 tomados del croquis, sin medir. Comprobar que la puerta abre hacia dentro sin chocar.
- Posición de P3: el 3,15 de planta baja y el 1,90 de planta alta se llevan 0,15; el 2,94 y el 3,20 se llevan 0,26. Se usa la cadena de PB.
- Del P3 a la escalera se midió 2,35 y en el plano salen 2,75. Los 0,40 no cierran contra la medianera Este.
- Pasillo de cocina: 0,77 m en el lavavajillas (0,651 de fondo) y 0,82 en el resto. Por debajo de 0,90 con permiso del cliente.
- Tabica de la escalera: 2,56/17 = 0,151 m. Contar los peldaños en obra.
- Máquinas: medidas de las fichas de makro.es tal y como las indexa su buscador; la web bloquea el acceso directo. Confirmar en la ficha.

GRUPO SUMA

Reformas y proyectos · Málaga

PROYECTO

Reforma integral de local de hostelería

EMPLAZAMIENTO

Local en planta baja y altillo
Málaga

PLANO

PLANTA ALTA

Altillo +2,56 · estructura

LEYENDA

- Muro de carga / medianera
- Pilar o machón de hormigón
- Tabiquería
- Barandilla de vidrio
- Mesas y sillas (medidas promedio)
- Punto de luz
- Vacío sobre planta baja

SUPERFICIES Y ALTURAS

Forjado de planta alta	33,74 m²
Altillo diáfano	26,17 m²
Aseo (lavabo + inodoro)	3,92 m²
Almacén	2,59 m²
Nivel del forjado, medido	+2,56 m
Puestos de cowork	14

PILARES Y MACHONES (secciones en m)

P1 Machón del muro Oeste	0,30 × 0,60
P2 Pilastra del muro Sur	0,58 × 0,45
P3 Pilar central	0,65 × 1,07
P4 Machón de la medianera Este	0,20 × 0,60
P5 Pilar de fachada	0,60 × 1,00

NOTAS


Cotas en metros, tomadas sobre el levantamiento.

Nivel del forjado +2,56, medido en obra.

El forjado del altillo no cubre todo el local: la franja sur y oeste es un vacío a doble altura.

Mesa de cowork 2,40 × 1,00 para 8 puestos y dos redondas de Ø 0,80 con 3 sillas. Medidas promedio.

Un colgante por mesa y empotrados en el resto.

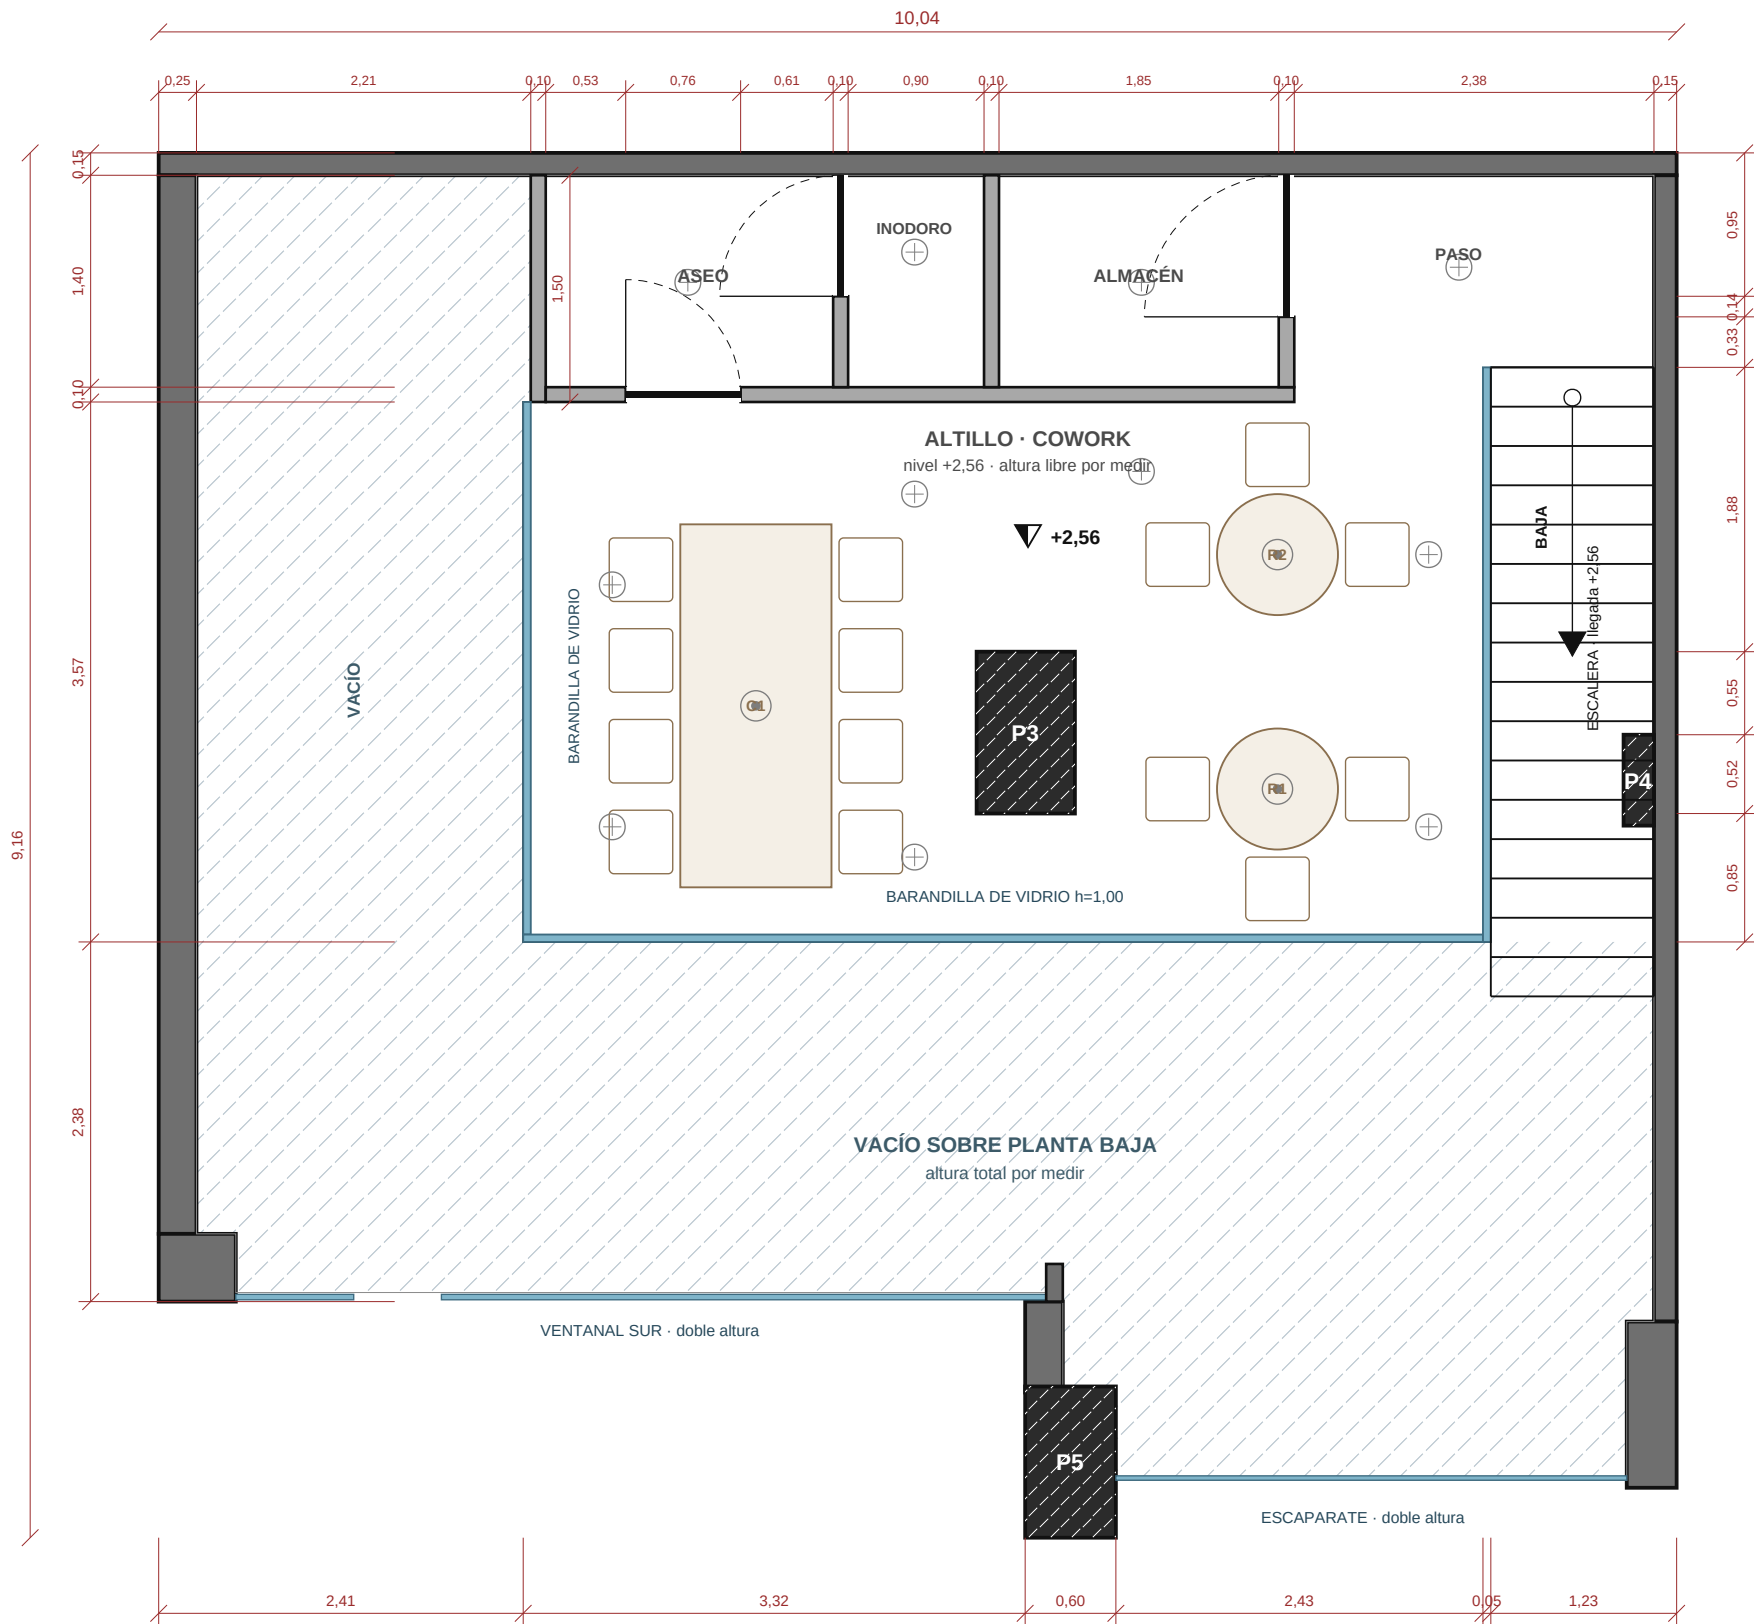

COMPROBAR EN OBRA Puntos en los que los vídeos del local no cuadran con el levantamiento, o que el levantamiento no recoge. Se dibuja el levantamiento por ser la única fuente acotada.

- Barra: medida 2,80 y dibujada 2,63, porque entre la pared en L de 4,22, el paso de 0,60 y el ventanal sólo quedan 2,63. Los 0,17 no cierran.
- Canto del forjado del altillo. Con 2,56 m de suelo a suelo, la altura libre de planta baja es 2,56 menos ese canto, no los 2,70 supuestos.
- P1b se dibuja como viga (1,83 × 0,25) y no como pilar: si fuera macizo hasta el suelo, la cocina no tendría entrada. Medir su intradós.
- Baño nuevo: tabiques de 0,10 y puerta de 0,70 tomados del croquis, sin medir. Comprobar que la puerta abre hacia dentro sin chocar.
- Posición de P3: el 3,15 de planta baja y el 1,90 de planta alta se llevan 0,15; el 2,94 y el 3,20 se llevan 0,26. Se usa la cadena de PB.
- Del P3 a la escalera se midió 2,35 y en el plano salen 2,75. Los 0,40 no cierran contra la medianera Este.
- Pasillo de cocina: 0,77 m en el lavavajillas (0,651 de fondo) y 0,82 en el resto. Por debajo de 0,90 con permiso del cliente.
- Tabica de la escalera: 2,56/17 = 0,151 m. Contar los peldaños en obra.
- Máquinas: medidas de las fichas de makro.es tal y como las indexa su buscador; la web bloquea el acceso directo. Confirmar en la ficha.

ESCALA

1:50 (A3)

FECHA

15 set. 2026

PLANO

02 / 03

GRUPO SUMA

Reformas y proyectos · Málaga

PROYECTO
Reforma integral de local de hostelería

EMPLAZAMIENTO
Local en planta baja y altílo
Málaga

PLANO
EQUIPAMIENTO

Barra y cocina · productos Makro

LEYENDA

- Bancada o mueble bajo
- Equipo refrigerado
- Encimera o tabla corrida
- Aparato (trazos: bajo encimera)
- Tabla de madera
- Muro de carga / medianera

HOLGURAS Y ALTURAS


Pasillo de cocina, mínimo	0,77 m
Paso de servicio en barra	1,02 m
Entrada a la cocina, bajo la viga	1,18 m
Altura de encimera	0,90 m
Borde inferior de la campana	2,00 m

NOTAS



Cada máquina es un producto real de makro.es con sus medidas de ficha; la web bloquea el acceso directo, así que las medidas vienen de su buscador. Confirmar en la ficha antes de comprar.

Cocción corrida en la medianera Norte bajo campana de 2,00; con la pared en L de 4,22 la cocina gana 0,62 m y la barra los pierde.

Pasillo de cocina de 0,77 a 0,82: por debajo de 0,90 con permiso del cliente. El frigorífico K9 topa con P1 (ajuste de 4 mm).

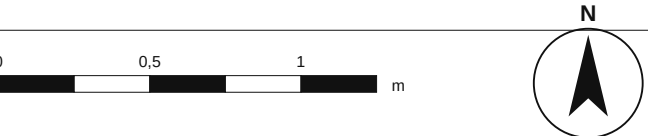

ESCALA	FECHA	PLANO
1:25 (A3)	15 set. 2026	03 / 03

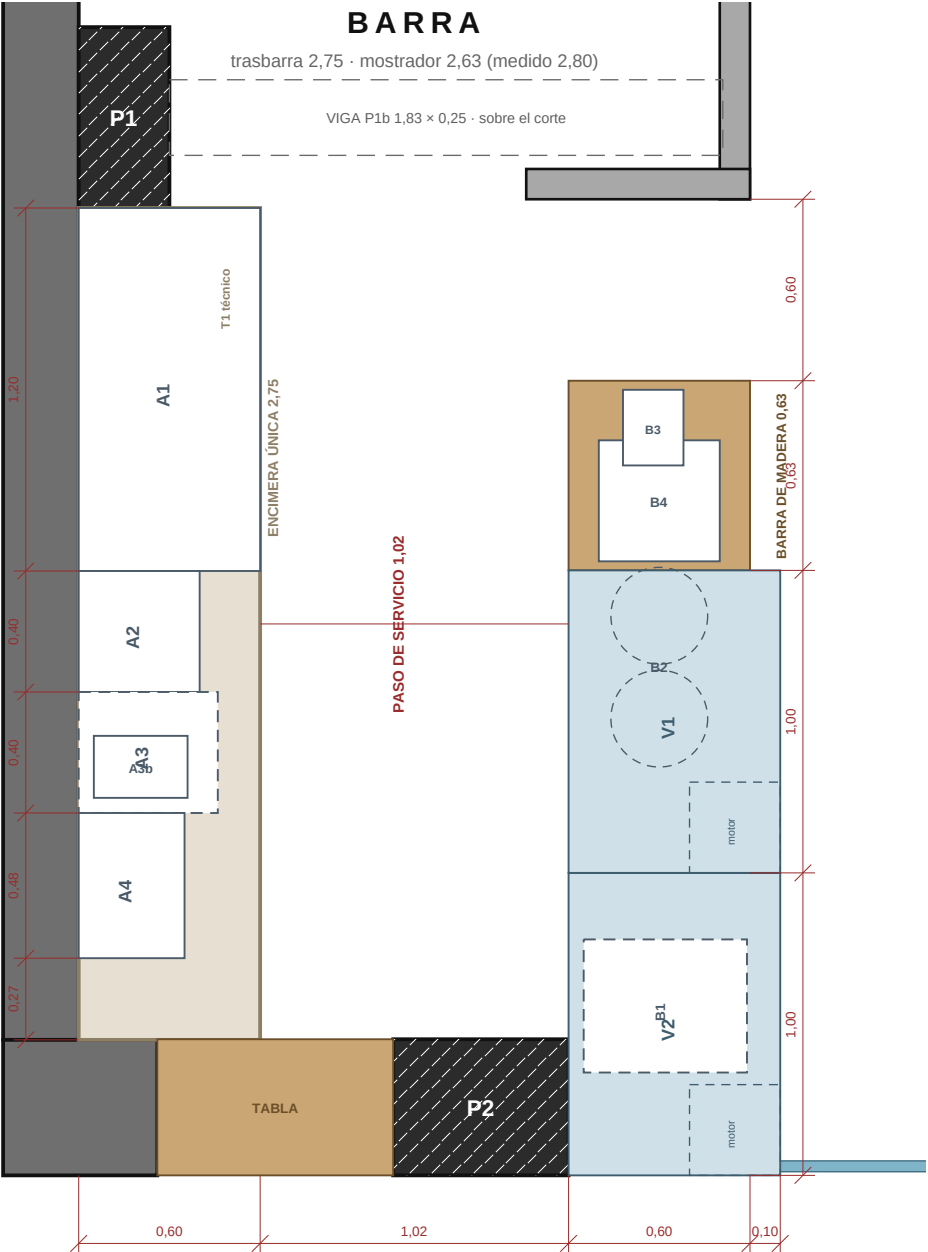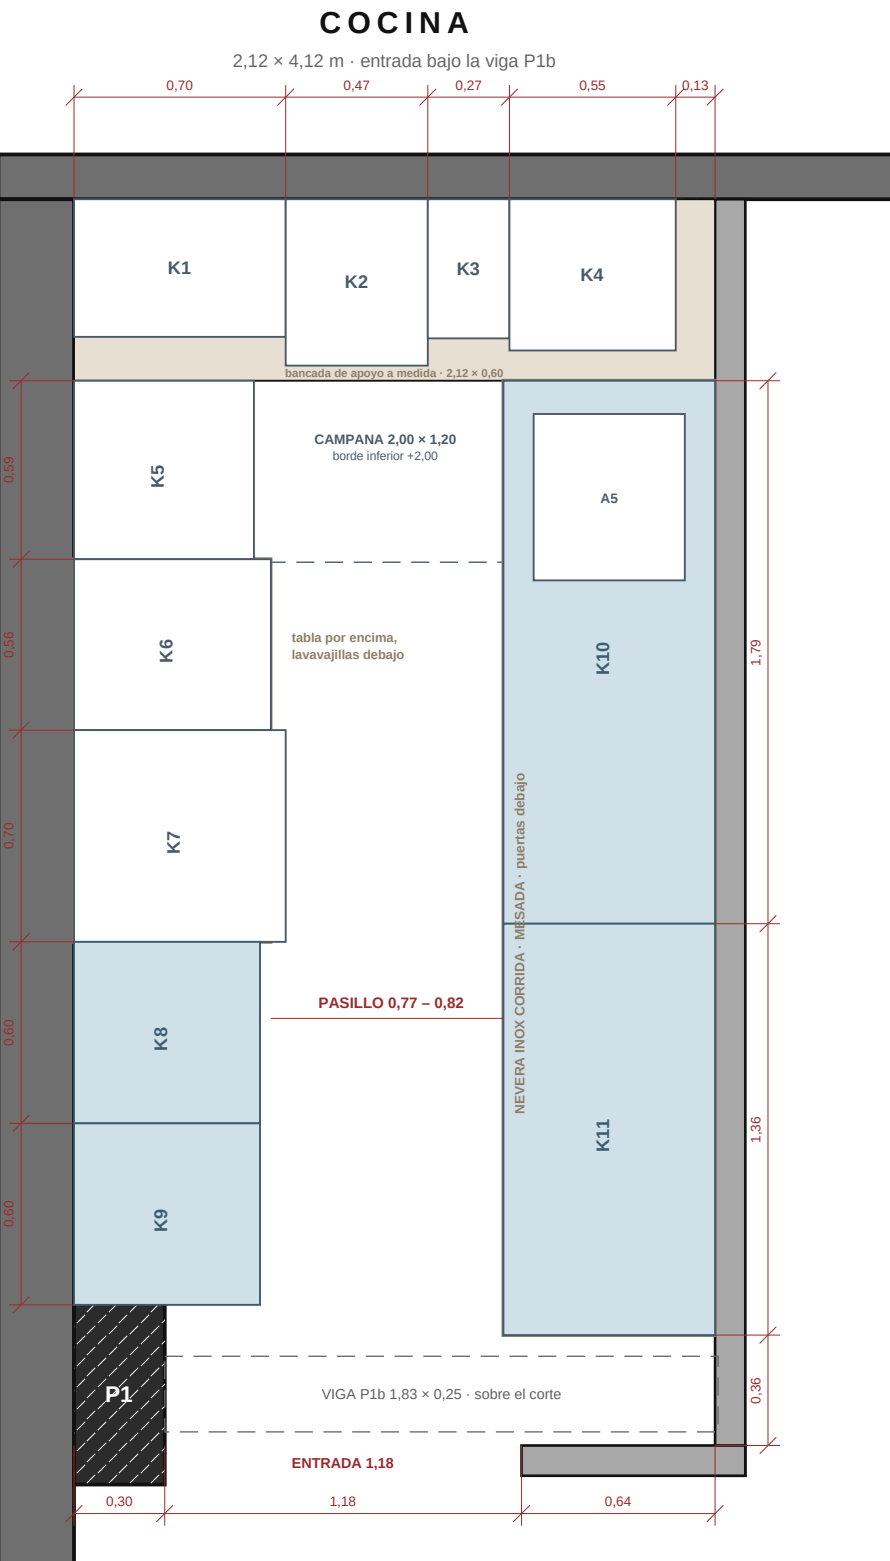

EQUIPAMIENTO · MAKRO Ancho × fondo × alto en metros, de la ficha de makro.es. Vitrinas y cafetera ya compradas. Cortadora, tablet y barriles con medida promedio.

K1	Placa de inducción Bartscher, 2 zonas Ø230, 6 kW, 400 V	0,70 × 0,46 × 0,12	A5	Cortadora de fiambre (medida promedio)	0,55 × 0,50 × 0,45
K2	Cocedor de pasta eléctrico METRO Professional GNC1008, 8 L, 4 cestos	0,47 × 0,55 × 0,38	A1	Cafetera (comprada), 2 grupos	1,20 × 0,60 × 0,50
K3	Freidora profesional 1 cuba de 7 L, eléctrica	0,27 × 0,46 × 0,37	A2	Lavamanos inox con grifo y pulsador de pedal, cuba Ø340	0,40 × 0,40 × 0,85
K4	Plancha eléctrica Cleiton 50 cm, placa de 8 mm, sobremesa	0,55 × 0,50 × 0,33	A3	Fabricador de hielo Gastro M CT694, 28 kg/24 h (bajo encimera)	0,40 × 0,46 × 0,67
KC	Campana extractora industrial recta, sin turbina, AISI-304 satinado, 2000 × 12	2,00 × 1,20 × 0,50	A4	Exprimidor de naranjas Mizumo Next Gen	0,48 × 0,35 × 0,73
K5	Horno de convección eléctrico industrial, 4 bandejas 45 × 33	0,59 × 0,59 × 0,57	A3b	Licuada industrial Sammic Li-240	0,20 × 0,31 × 0,36
K6	Lavavajillas industrial ST500, cesta 50 × 50, bajo la tabla	0,56 × 0,65 × 0,83	V2	Vitrina refrigerada (comprada), 1,00 × 0,70; debajo, lavavasos	1,00 × 0,70 × 1,25
K7	Fregadero industrial Royal Catering, 1 cubeta 50 × 50, 70 × 70	0,70 × 0,70 × 0,85	V1	Vitrina refrigerada (comprada), 1,00 × 0,70; debajo, barriles	1,00 × 0,70 × 1,25
K8	Armario refrigerado vertical AR400L Clima Hostelería, inox, 360 L	0,60 × 0,61 × 1,87	B1	Lavavasos Elettrobar FAST 40, cesta 40 × 40 (bajo la vitrina V2)	0,44 × 0,54 × 0,67
K9	Armario refrigerado vertical AR400L Clima Hostelería, inox, 360 L	0,60 × 0,61 × 1,87	B2	Barriles de cerveza de 30 L, Ø 0,32 (bajo la vitrina V1)	0,32 × 0,32 × 0,60
K10	Mesa refrigerada METRO Professional GCC3100, inox, 3 puertas, 334 L	1,79 × 0,70 × 0,85	B3	Caja: tablet sobre soporte	0,25 × 0,20 × 0,25
K11	Mesa refrigerada bajo mostrador, 2 puertas, ventilada, mural	1,36 × 0,70 × 0,85	B4	Columna de cerveza de 2 grifos (Makro sólo lista la de 3, bandeja 40 × 40)	0,40 × 0,40 × 0,55