

GRUPO SUMA

Reformas y proyectos · Málaga

PROYECTO

Reforma integral de local de hostelería

EMPLAZAMIENTO

Local en planta baja y altillo
Málaga

PLANO

PLANTA ALTA

Altillo +2,56 · estructura

LEYENDA

- Muro de carga / medianera
- Pilar o machón de hormigón
- Tabiquería
- Barandilla de vidrio
- Vacío sobre planta baja

SUPERFICIES Y ALTURAS

Forjado de planta alta	33,74 m²
Altillo diáfano	26,17 m²
Aseo (lavabo + inodoro)	3,92 m²
Almacén	2,59 m²
Nivel del forjado, medido	+2,56 m
Altura libre de planta alta	2,50 m (por medir)

PILARES Y MACHONES (secciones en m)

P1 Machón del muro Oeste	0,30 × 0,60
P1b Machón sobre P1, al forjado	1,83 × 0,25
P2 Pilastra del muro Sur	0,58 × 0,45
P3 Pilar central	0,65 × 1,07
P4 Machón de la medianera Este	0,20 × 0,60
P5 Pilar de fachada	0,60 × 1,00

NOTAS

Cotas en metros, tomadas sobre el levantamiento.
Plano de estructura: no se representa mobiliario ni equipamiento.
El forjado del altillo no cubre todo el local: la franja sur y oeste es un vacío a doble altura.
Nivel del forjado +2,56, medido en obra.
Sección horizontal a 1,20 m sobre el forjado.



ESCALA


1:50 (A3)

FECHA

14 set. 2026

PLANO

02 / 02

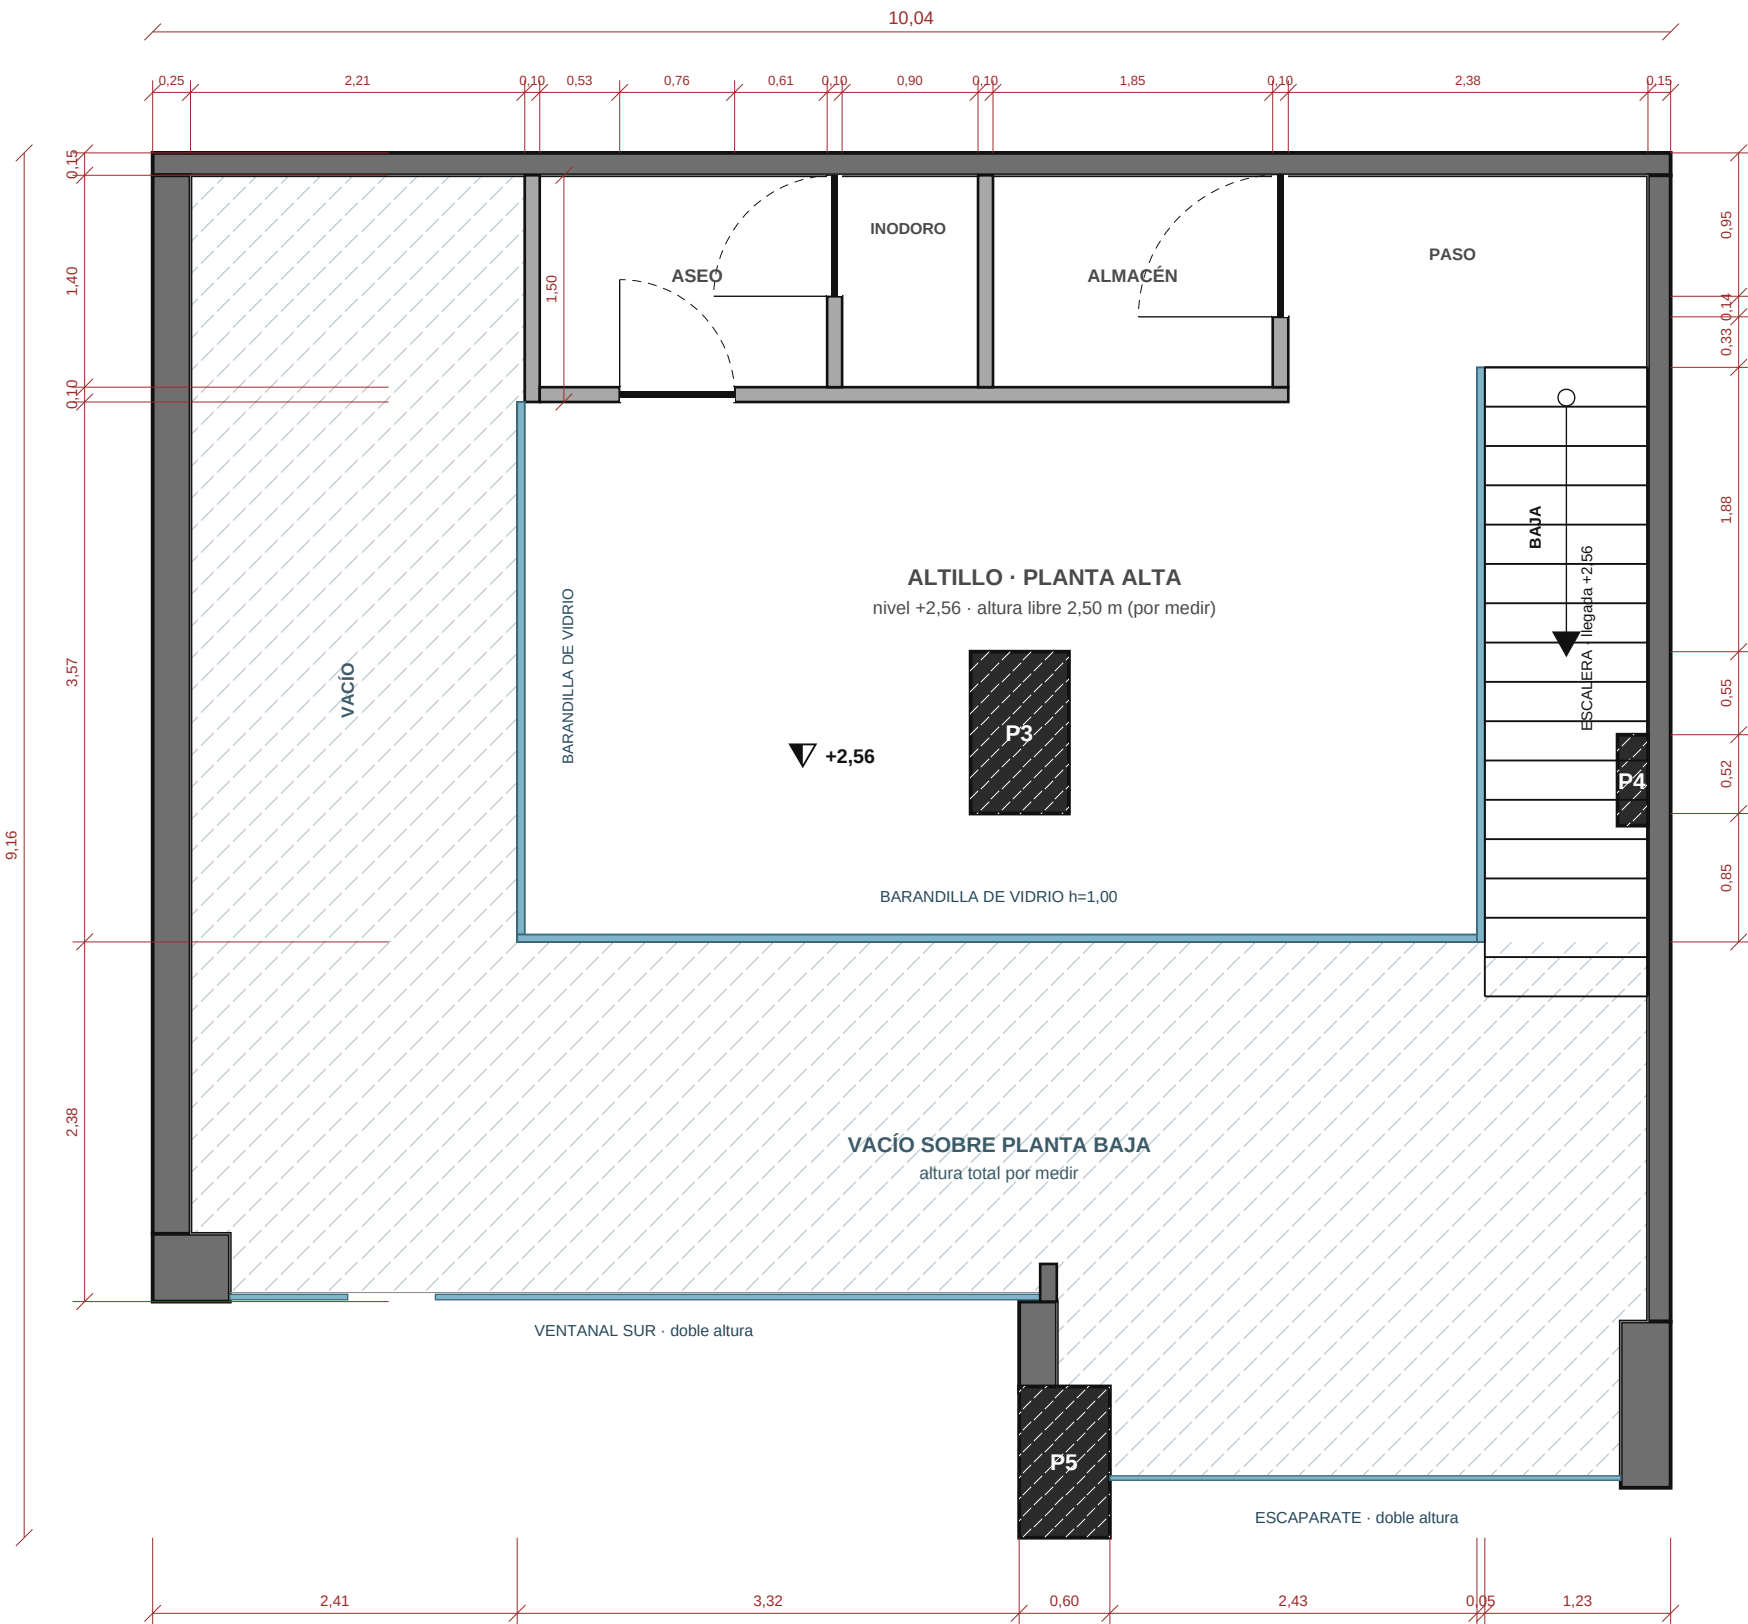

COMPROBAR EN OBRA Puntos en los que los vídeos del local no cuadran con el levantamiento, o que el levantamiento no recoge. Se dibuja el levantamiento por ser la única fuente acotada.

- La cota de 2,70 anotada contra la medianera norte no cuadra: mide la misma distancia que el 2,22 aplicado (muro Oeste a pared en L). Aclarar qué mide ese 2,70.
- Canto del forjado del altillo. Con 2,56 m de suelo a suelo, la altura libre de planta baja es 2,56 menos ese canto, no los 2,70 supuestos.
- Espesor de la pared en L y del panel de vidrio de 1,35 m que sostiene.
- Posición de P3: el 3,15 de la planta baja y el 1,90 de la planta alta se llevan 0,15; el 2,94 y el 3,20 se llevan 0,26. Se dibuja con la cadena de planta baja.
- Del P3 a la escalera se midió 2,35 y en el plano salen 2,75. Los 0,40 de diferencia no cierran contra la medianera Este.
- P5: se dibuja 0,60 x 1,00 con la cara Oeste a plomo con el muro del cuello. El resalto de 0,20 al Este anotado da 0,35 en esa posición.
- Escaparate: bajo él aparece un 2,70 sin aclarar. Se dibuja el hueco completo con la puerta de 2,10 pegada a P5.
- Tabica de la escalera: $2,56/17 = 0,151$ m. Contar los peldaños en obra para confirmar que son 17.
- Machones trasdosados con placa de yeso nueva: la sección de hormigón no es verificable a la vista.