

# GRUPO SUMA

Reformas y proyectos · Málaga

## PROYECTO

Reforma integral de local de hostelería

## EMPLAZAMIENTO

Local en planta baja y altillo  
Málaga

## PLANO

PLANTA ALTA

Altillo +2,56 · estructura

## LEYENDA

- Muro de carga / medianera
- Pilar o machón de hormigón
- Tabiquería
- Barandilla de vidrio
- Mesas y sillas (medidas promedio)
- Paso libre entre mobiliario (m)
- Vacío sobre planta baja

## SUPERFICIES Y ALTURAS


|                           |          |
|---------------------------|----------|
| Forjado de planta alta    | 33,74 m² |
| Altillo diáfano           | 26,17 m² |
| Aseo (lavabo + inodoro)   | 3,92 m²  |
| Almacén                   | 2,59 m²  |
| Nivel del forjado, medido | +2,56 m  |
| Puestos de cowork         | 14       |

## PILARES Y MACHONES (secciones en m)

|                                |             |
|--------------------------------|-------------|
| P1 Machón del muro Oeste       | 0,30 × 0,60 |
| P2 Pilastra del muro Sur       | 0,58 × 0,45 |
| P3 Pilar central               | 0,65 × 1,07 |
| P4 Machón de la medianera Este | 0,20 × 0,60 |
| P5 Pilar de fachada            | 0,60 × 1,00 |

## NOTAS

Cotas en metros, tomadas sobre el levantamiento.  
Nivel del forjado +2,56, medido en obra.  
El forjado del altillo no cubre todo el local: la franja sur y oeste es un vacío a doble altura.  
Mesa de cowork 2,40 × 1,00 para 8 puestos y una redonda de Ø 1,20 con 6 sillas. Medidas promedio.  
Pasos libres entre mobiliario acotados en azul:  
1,01 hacia el aseo y el almacén; 1,30 en el desembarco; 0,26 a 0,85 en los accesos a las sillas.

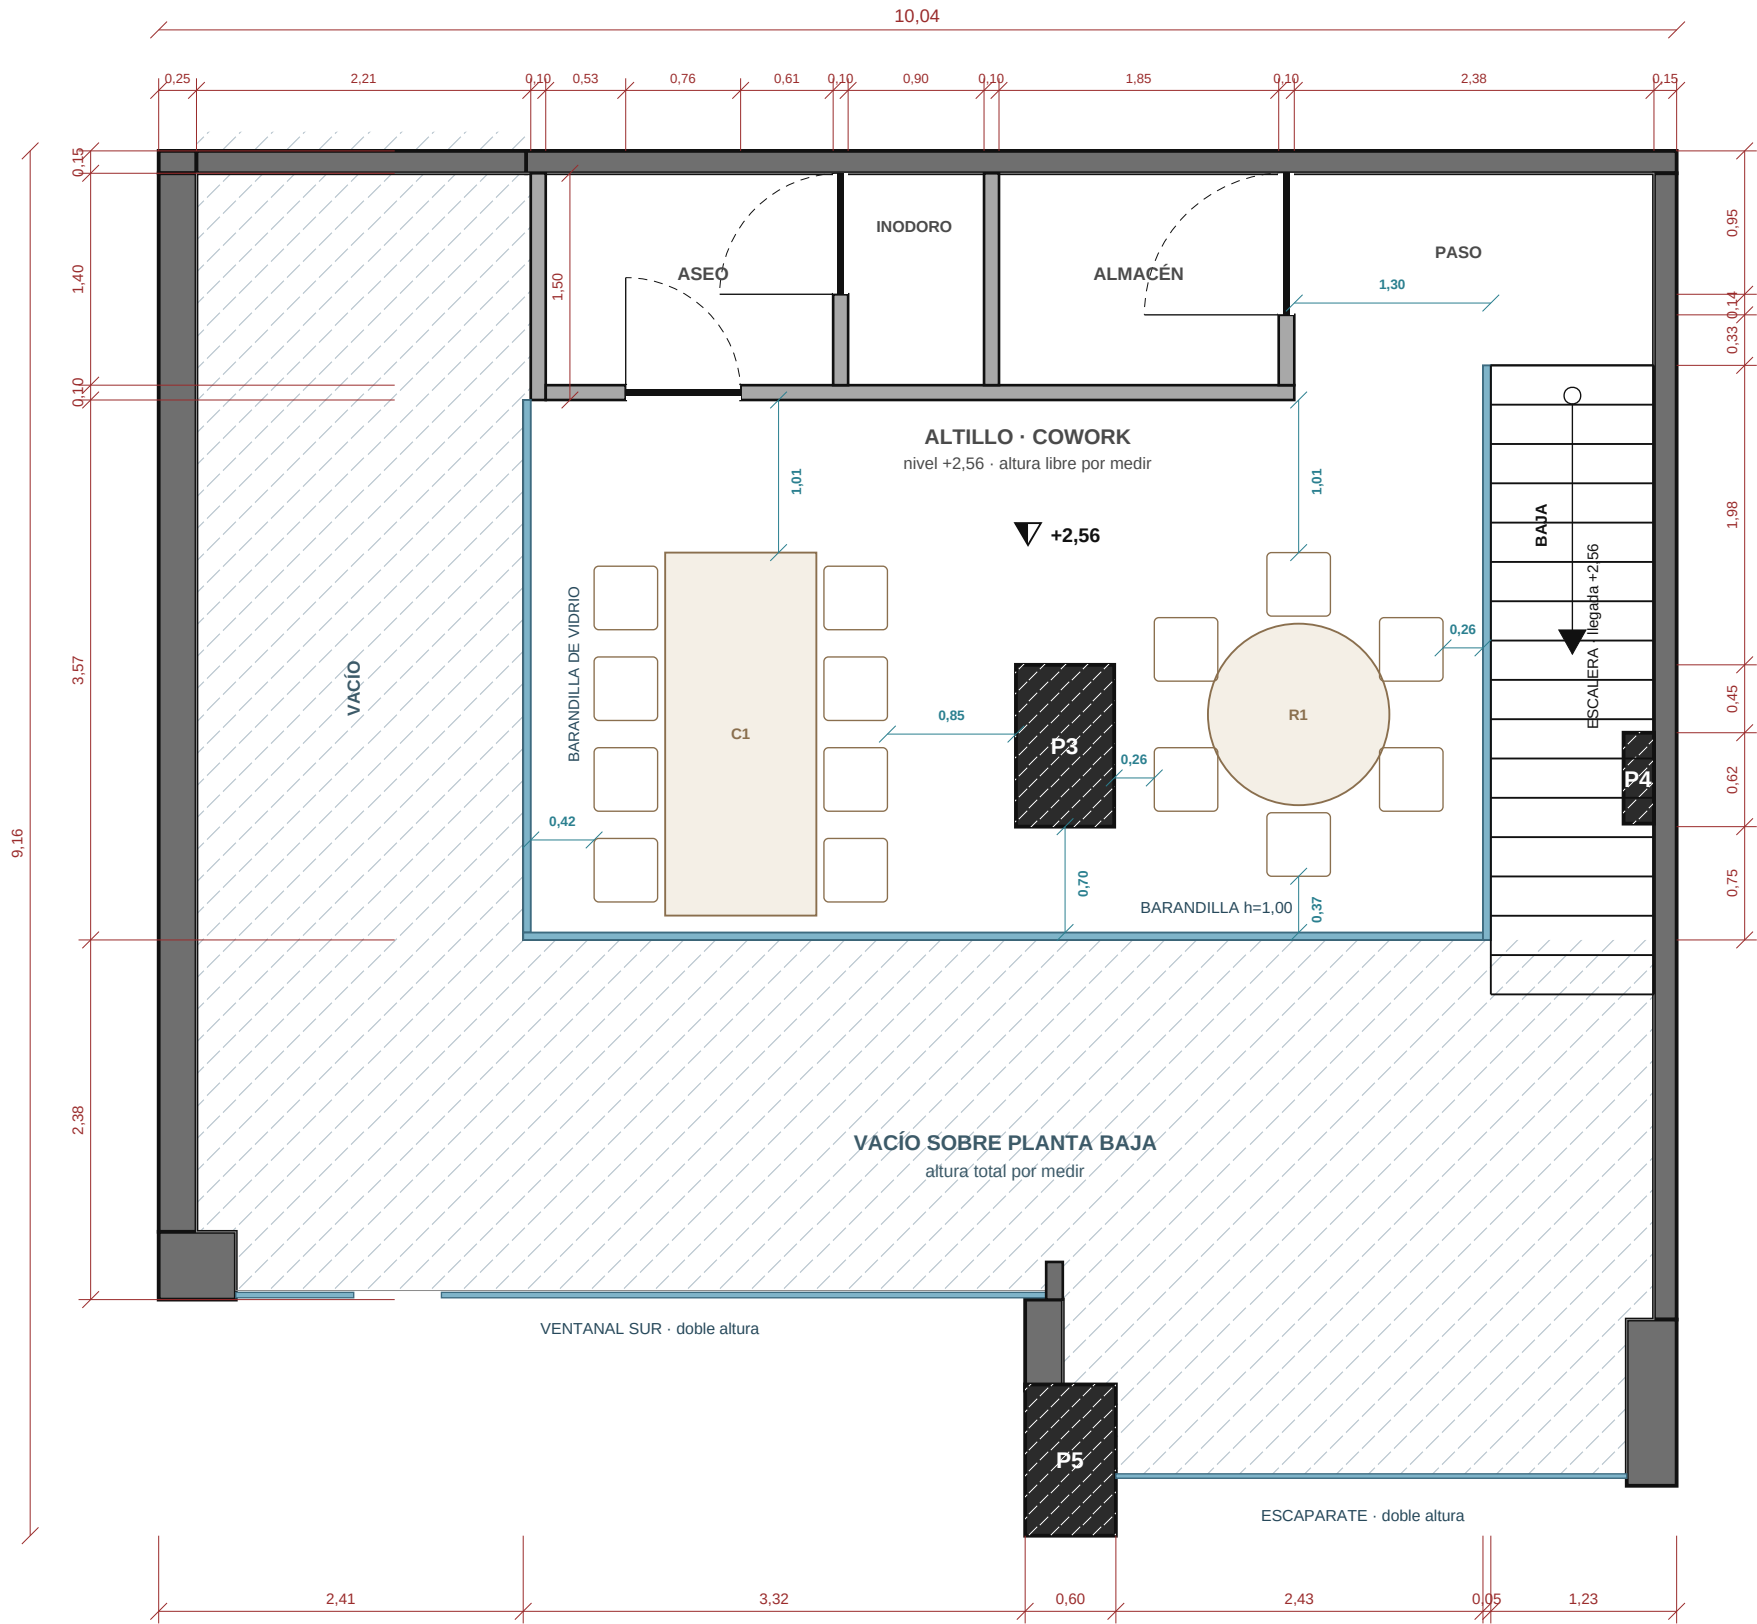

## COMPROBAR EN OBRA

Puntos en los que los vídeos del local no cuadran con el levantamiento, o que el levantamiento no recoge. Se dibuja el levantamiento por ser la única fuente acotada.

- Hundimiento de la medianera Norte: 0,275 de fondo en los 2,18 de la cocina. Supera el espesor dibujado (0,148): medir ese cerramiento y lo que hay detrás.
- Canto del forjado del altillo. Con 2,56 m de suelo a suelo, la altura libre de planta baja es 2,56 menos ese canto, no los 2,70 supuestos.
- P1b se dibuja como viga (1,83 × 0,25) y no como pilar: si fuera macizo hasta el suelo, la cocina no tendría entrada. Medir su intradós.
- Zócalo del ventanal: 0,347 desde el vidrio, deducido de los 2,72 de P3 a su cara interior; sobresale 0,16 del muro del ventanal (0,25). Medirlo directamente.
- Cadena Este-Oeste del cliente (2,18 + 3,01 + 0,65 + 2,33): cierra contra la escalera con 0,13 de pared entre el hundimiento y la L y 0,16 de cerramiento.
- La pared en L queda 0,10 al Este del borde del forjado del levantamiento: el vidrio de 1,35 sobre ella (2,57 en total) no pasa bajo el altillo. Medir ese borde.
- Pasillo de cocina: 0,97 m frente a los frigoríficos (0,74 de fondo) y 1,11 frente al fregadero. Antes eran 0,78.
- P5: los 3,65 medidos de P3 a su cara Norte la sitúan en 1,058 y el levantamiento en 1,000. Se dibuja el levantamiento (6 cm). Medir también el resalto de P5.
- Aire acondicionado: dos cassettes situados con las fotos del cliente, con panel estándar de 0,95 y rejilla de 0,90 × 0,50. Medir posición y tamaño reales.

## ESCALA

1:50 (A3)

## FECHA

15 set. 2026

## PLANO

02 / 04