

PROYECTO

Reforma integral de local de hostelería

EMPLAZAMIENTO

Local en planta baja y altillo
Málaga

PLANO

PLANTA BAJA

Estado actual · estructura

LEYENDA

- Muro de carga / medianera
- Pilar o machón de hormigón
- Pared en L nueva (apoyo del vidrio)
- Carpintería acristalada
- Espacio de doble altura
- Forjado sobre el corte
- Reserva de espacio del cliente
- Mesas dobles de 0,70 × 0,70 y sillas
- Itinerario accesible ≥ 1,20 · giro Ø 1,50
- Punto de luz s/ proyecto original
- Aire acondicionado (cassette de techo)

SUPERFICIES Y ALTURAS

Planta baja, dentro de muros	76,23 m²
Zona de doble altura	38,40 m²
Suelo a suelo, medido en obra	2,56 m
Altura libre bajo forjado	2,56 – canto
Pared en L, altura	1,22 m
Mesas dobles / plazas sentadas	11 / 22
Acristalamiento de fachada	≈ 4,70 m

PILARES Y MACHONES (secciones en m)

P1 Machón del muro Oeste	0,30 × 0,60
P2 Pilastra del muro Sur	0,58 × 0,45
P3 Pilar central	0,65 × 1,07
P4 Machón de la medianera Este	0,20 × 0,60
P5 Pilar de fachada	0,60 × 1,00

NOTAS

Cotas en metros. Hundimiento, pared en L, P3, barra, zócalo y puerta con las medidas del 19 set.; el resto, del levantamiento. ±0,00 en el pavimento, sección a 1,20 m. Equipamiento en la lámina 03. Mesas dobles de 0,70 × 0,70 que el personal junta para formar mesas de cuatro. M4 pegada a P3. Luces: las del proyecto original; los dos cassettes de aire, situados con las fotos del cliente. Itinerario accesible de 1,20 de la puerta a la barra, al baño y a la plaza PMR de M1, con giros de Ø 1,50 en la entrada y ante el baño; el baño no es accesible.



ESCALA


1:50 (A3)

FECHA

15 set. 2026

PLANO

01 / 04

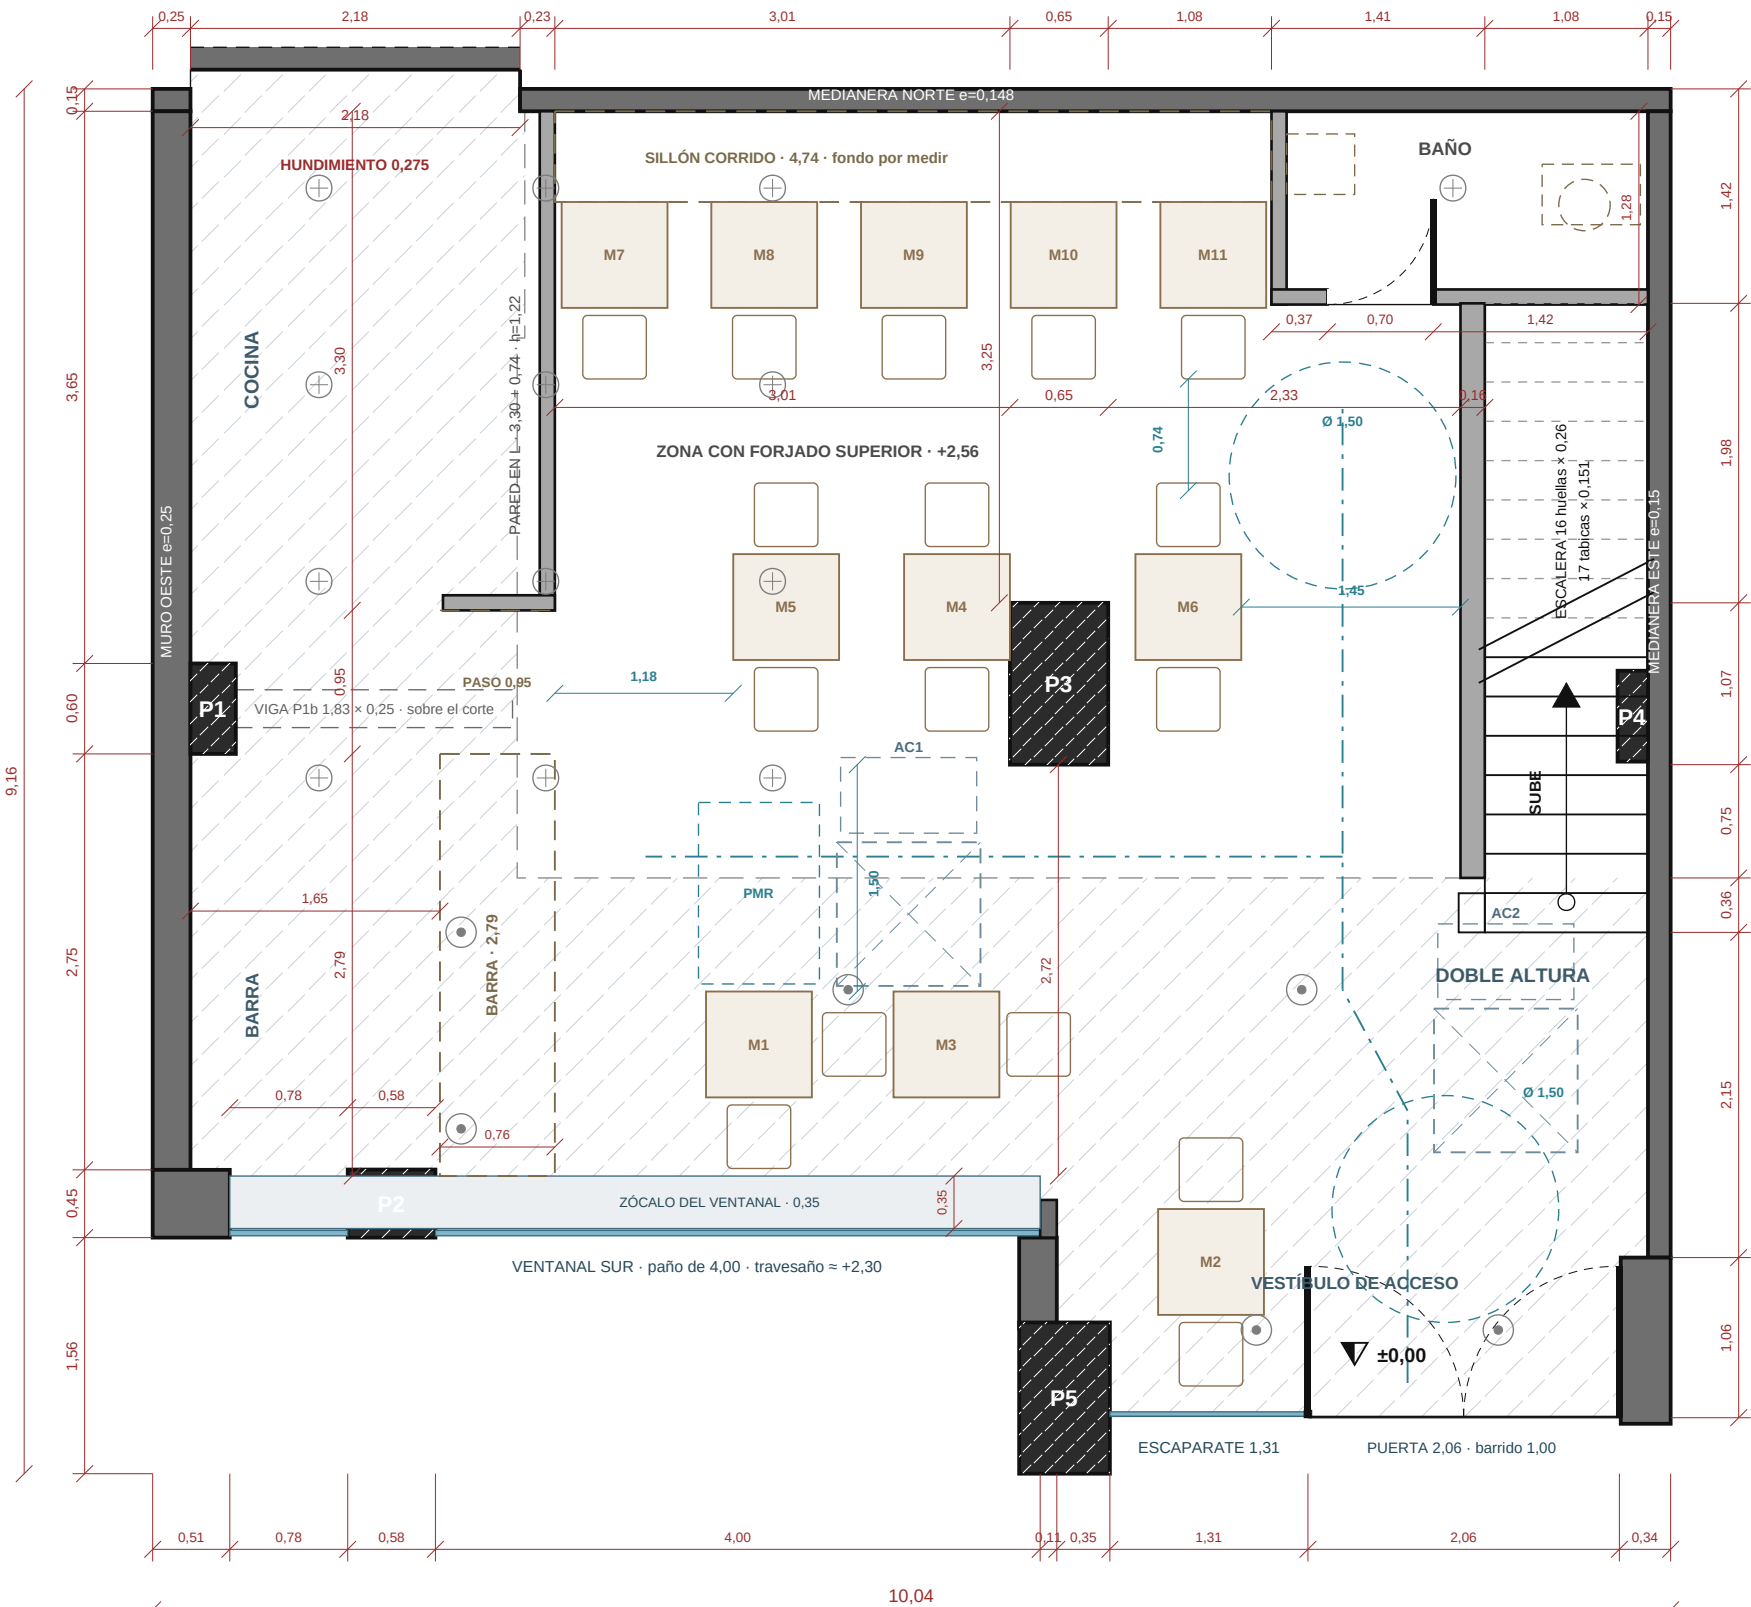

COMPROBAR EN OBRA

Puntos en los que los vídeos del local no cuadran con el levantamiento, o que el levantamiento no recoge. Se dibuja el levantamiento por ser la única fuente acotada.

- Hundimiento de la medianera Norte: 0,275 de fondo en los 2,18 de la cocina. Supera el espesor dibujado (0,148): medir ese cerramiento y lo que hay detrás.
- Canto del forjado del altillo. Con 2,56 m de suelo a suelo, la altura libre de planta baja es 2,56 menos ese canto, no los 2,70 supuestos.
- P1b se dibuja como viga (1,83 × 0,25) y no como pilar: si fuera macizo hasta el suelo, la cocina no tendría entrada. Medir su intradós.
- Zócalo del ventanal: 0,347 desde el vidrio, deducido de los 2,72 de P3 a su cara interior; sobresale 0,16 del muro del ventanal (0,25). Medirlo directamente.
- Cadena Este-Oeste del cliente (2,18 + 3,01 + 0,65 + 2,33): cierra contra la escalera con 0,13 de pared entre el hundimiento y la L y 0,16 de cerramiento.
- La pared en L queda 0,10 al Este del borde del forjado del levantamiento: el vidrio de 1,35 sobre ella (2,57 en total) no pasa bajo el altillo. Medir ese borde.
- Pasillo de cocina: 0,97 m frente a los frigoríficos (0,74 de fondo) y 1,11 frente al fregadero. Antes eran 0,78.
- P5: los 3,65 medidos de P3 a su cara Norte la sitúan en 1,058 y el levantamiento en 1,000. Se dibuja el levantamiento (6 cm). Medir también el resalto de P5.
- Aire acondicionado: dos cassettes situados con las fotos del cliente, con panel estándar de 0,95 y rejilla de 0,90 × 0,50. Medir posición y tamaño reales.

GRUPO SUMA

Reformas y proyectos · Málaga

PROYECTO

Reforma integral de local de hostelería

EMPLAZAMIENTO

Local en planta baja y altílo
Málaga

PLANO

PLANTA ALTA

Altílo +2,56 · estructura

LEYENDA

- Muro de carga / medianera
- Pilar o machón de hormigón
- Tabiquería
- Barandilla de vidrio
- Mesas y sillas (medidas promedio)
- Paso libre entre mobiliario (m)
- Vacío sobre planta baja

SUPERFICIES Y ALTURAS

Forjado de planta alta	33,74 m²
Altílo diáfano	26,17 m²
Aseo (lavabo + inodoro)	3,92 m²
Almacén	2,59 m²
Nivel del forjado, medido	+2,56 m
Puestos de cowork	14

PILARES Y MACHONES (secciones en m)

P1 Machón del muro Oeste	0,30 × 0,60
P2 Pilastra del muro Sur	0,58 × 0,45
P3 Pilar central	0,65 × 1,07
P4 Machón de la medianera Este	0,20 × 0,60
P5 Pilar de fachada	0,60 × 1,00

NOTAS

Cotas en metros, tomadas sobre el levantamiento.


Nivel del forjado +2,56, medido en obra.

El forjado del altílo no cubre todo el local: la franja sur y oeste es un vacío a doble altura.

Mesa de cowork 2,40 × 1,00 para 8 puestos y una redonda de Ø 1,20 con 6 sillas. Medidas promedio.

Pasos libres entre mobiliario acotados en azul:


1,01 hacia el aseo y el almacén; 1,30 en el desembarco; 0,26 a 0,85 en los accesos a las sillas.

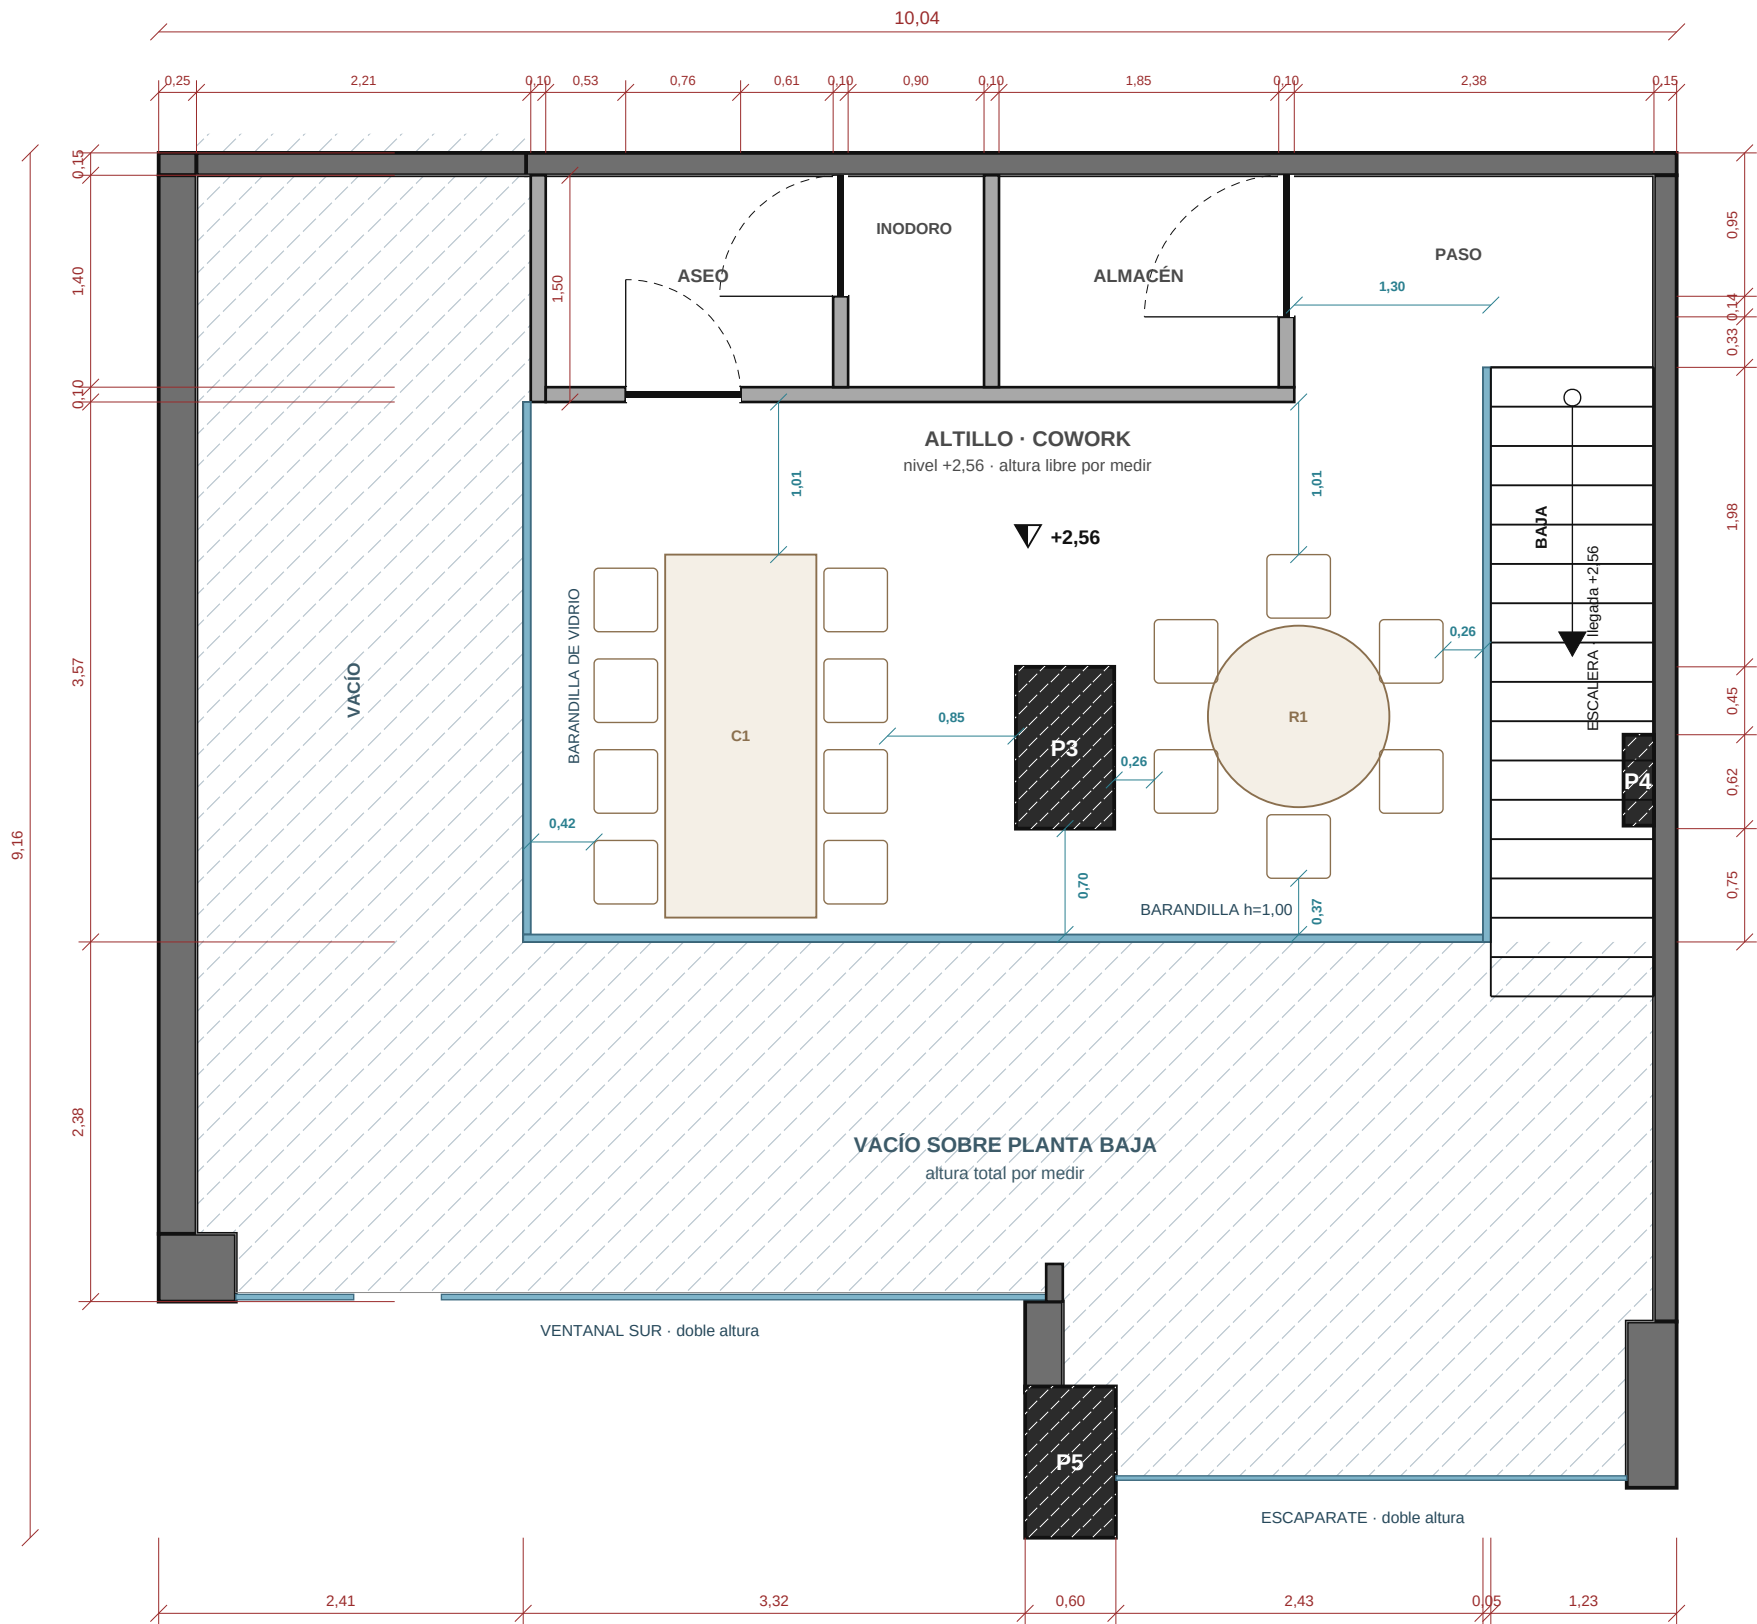

COMPROBAR EN OBRA

Puntos en los que los vídeos del local no cuadran con el levantamiento, o que el levantamiento no recoge. Se dibuja el levantamiento por ser la única fuente acotada.

- Hundimiento de la medianera Norte: 0,275 de fondo en los 2,18 de la cocina. Supera el espesor dibujado (0,148): medir ese cerramiento y lo que hay detrás.
- Canto del forjado del altílo. Con 2,56 m de suelo a suelo, la altura libre de planta baja es 2,56 menos ese canto, no los 2,70 supuestos.
- P1b se dibuja como viga (1,83 × 0,25) y no como pilar: si fuera macizo hasta el suelo, la cocina no tendría entrada. Medir su intradós.
- Zócalo del ventanal: 0,347 desde el vidrio, deducido de los 2,72 de P3 a su cara interior; sobresale 0,16 del muro del ventanal (0,25). Medirlo directamente.
- Cadena Este-Oeste del cliente (2,18 + 3,01 + 0,65 + 2,33): cierra contra la escalera con 0,13 de pared entre el hundimiento y la L y 0,16 de cerramiento.
- La pared en L queda 0,10 al Este del borde del forjado del levantamiento: el vidrio de 1,35 sobre ella (2,57 en total) no pasa bajo el altílo. Medir ese borde.
- Pasillo de cocina: 0,97 m frente a los frigoríficos (0,74 de fondo) y 1,11 frente al fregadero. Antes eran 0,78.
- P5: los 3,65 medidos de P3 a su cara Norte la sitúan en 1,058 y el levantamiento en 1,000. Se dibuja el levantamiento (6 cm). Medir también el resalto de P5.
- Aire acondicionado: dos cassettes situados con las fotos del cliente, con panel estándar de 0,95 y rejilla de 0,90 × 0,50. Medir posición y tamaño reales.

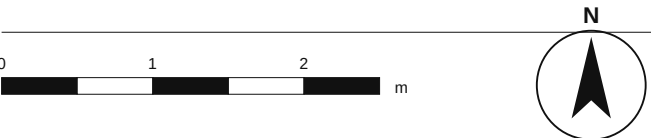

ESCALA	FECHA	PLANO
1:50 (A3)	15 set. 2026	02 / 04