

PROYECTO

Reforma integral de local de hostelería

EMPLAZAMIENTO

Local en planta baja y altillo
Málaga

PLANO

PLANTA BAJA

Estado actual · estructura

LEYENDA

- Muro de carga / medianera
- Pilar o machón de hormigón
- Pared en L nueva (apoyo del vidrio)
- Carpintería acristalada
- Espacio de doble altura
- Forjado sobre el corte
- Reserva de espacio del cliente
- Mesas y sillas (medidas promedio)
- Punto de luz: colgante / empotrado

SUPERFICIES Y ALTURAS


Planta baja, dentro de muros	75,63 m²
Zona de doble altura	37,80 m²
Suelo a suelo, medido en obra	2,56 m
Altura libre bajo forjado	2,56 – canto
Pared en L, altura	1,22 m
Plazas sentadas en planta baja	32
Acristalamiento de fachada	≈ 4,70 m

PILARES Y MACHONES (secciones en m)


P1 Machón del muro Oeste	0,30 × 0,60
P2 Pilastra del muro Sur	0,58 × 0,45
P3 Pilar central	0,65 × 1,07
P4 Machón de la medianera Este	0,20 × 0,60
P5 Pilar de fachada	0,60 × 1,00

NOTAS

Cotas en metros. Las de los pilares, la pared en L, el ventanal y la puerta están medidas en obra (revisión del 14 set. 2026); el resto procede del levantamiento previo.
Cota de referencia ±0,00 en el pavimento de planta baja. Sección horizontal a 1,20 m.
Mesas con medidas promedio (doble 0,70 × 0,70; cuádruple 1,20 × 0,70). Puntos de luz replanteados sobre el mobiliario: un colgante por mesa, tres sobre la barra y empotrados en pasillos y cocina.
Equipamiento de barra y cocina en la lámina 03; lista de compra con enlaces en la lámina 04.

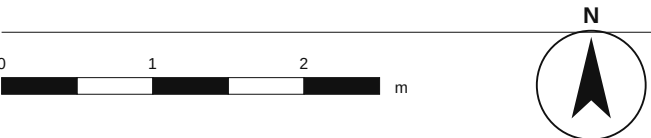

ESCALA	FECHA	PLANO
1:50 (A3)	15 set. 2026	01 / 04

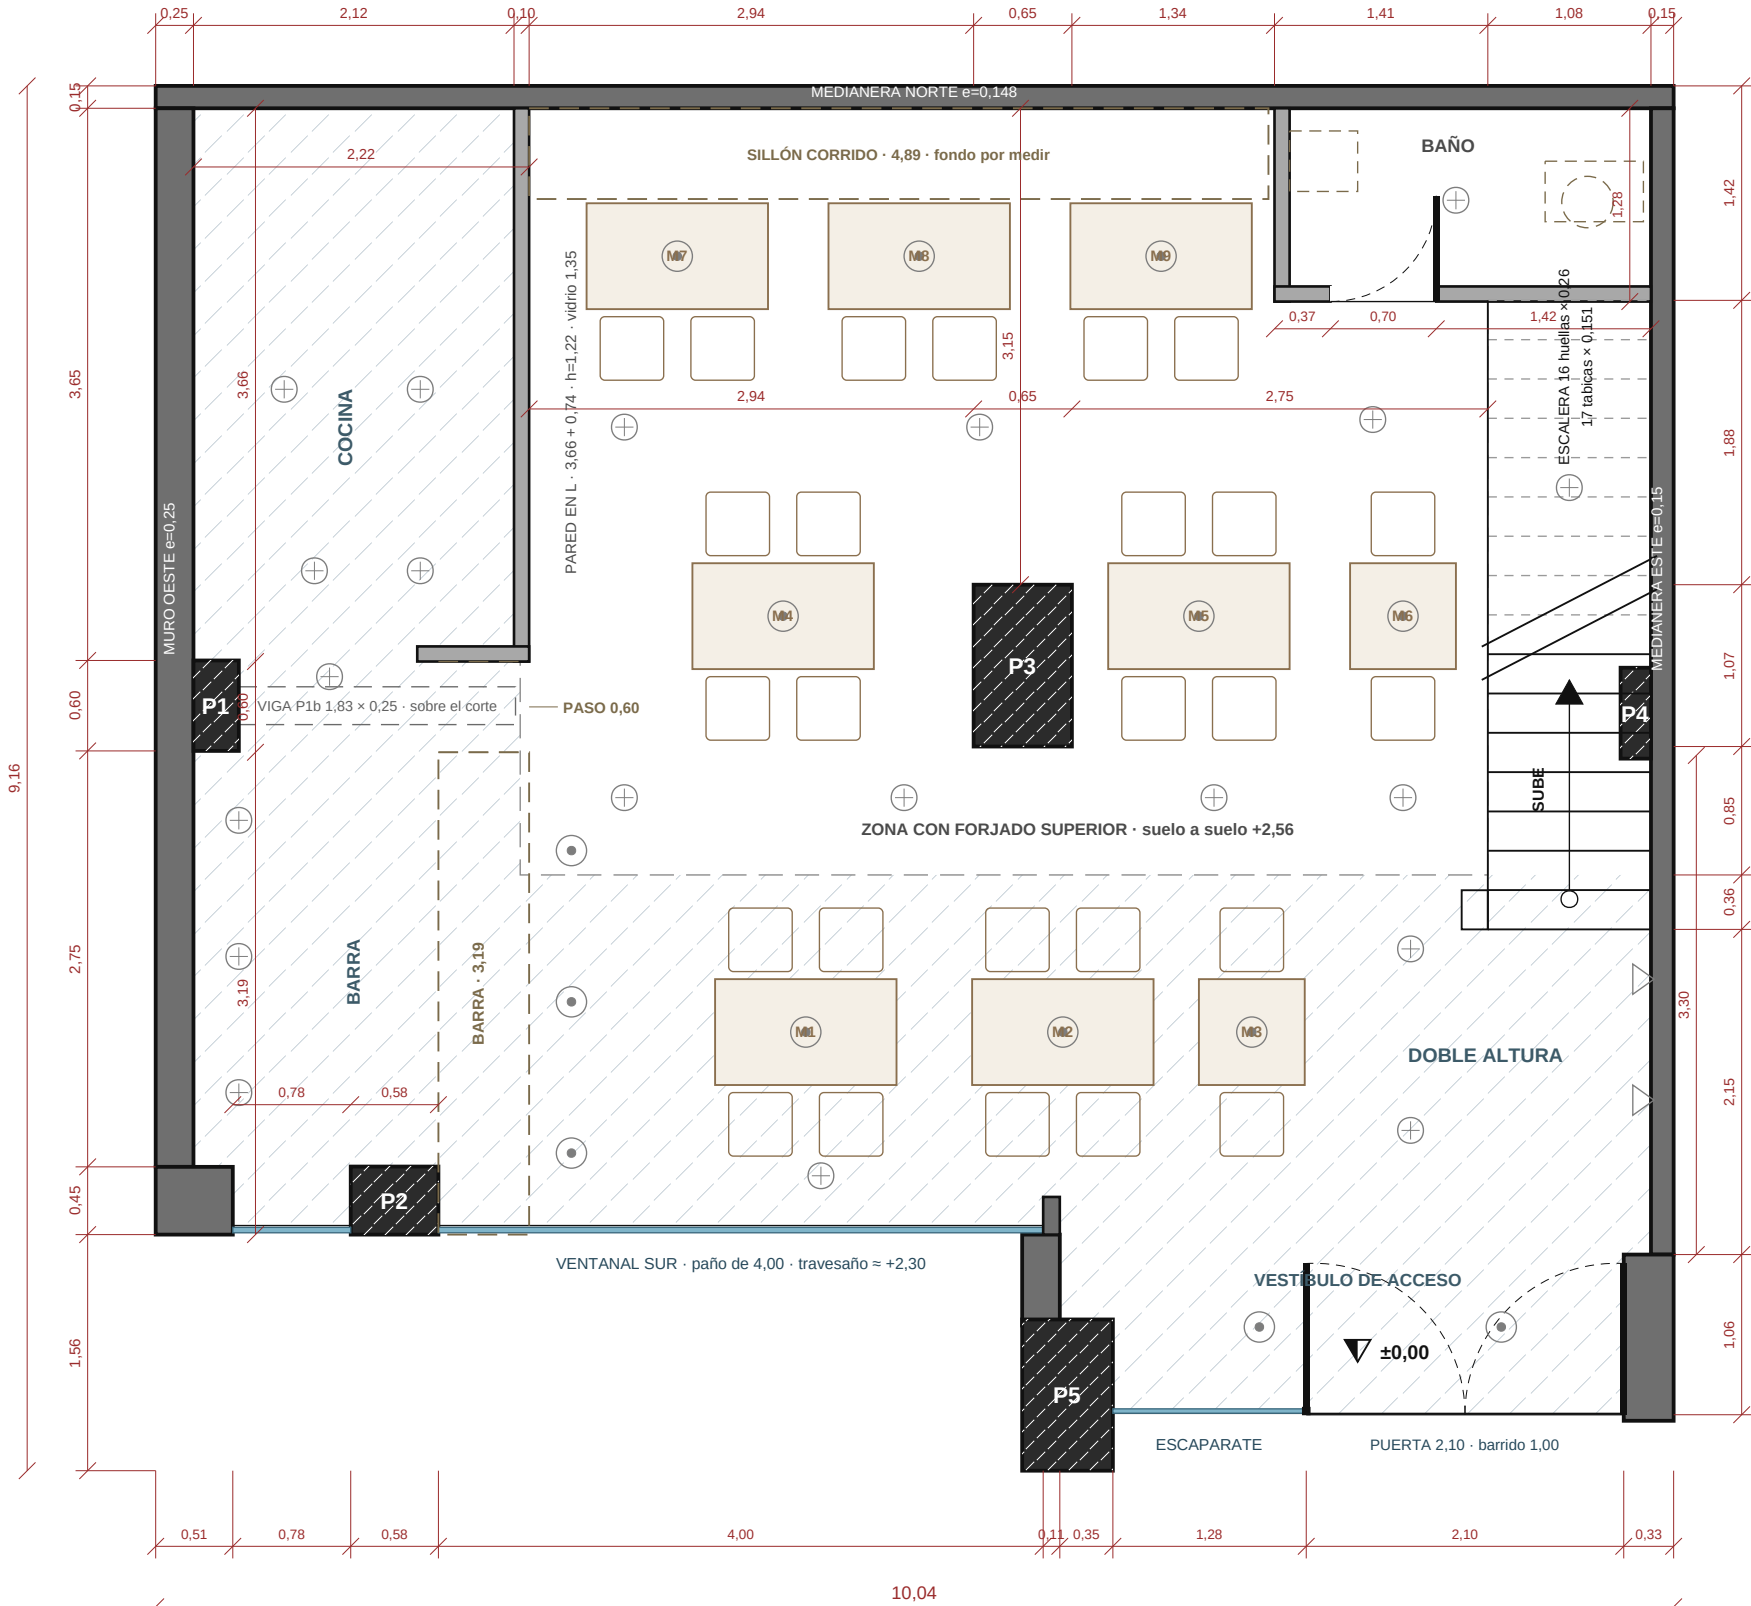

COMPROBAR EN OBRA Puntos en los que los vídeos del local no cuadran con el levantamiento, o que el levantamiento no recoge. Se dibuja el levantamiento por ser la única fuente acotada.

- Pared en L: en el segundo croquis termina en y=5,35 (3,66 m) y la barra sube hasta 4,75 con el paso de 0,60 entre ambas. Antes se midió 4,22.
- Canto del forjado del altillo. Con 2,56 m de suelo a suelo, la altura libre de planta baja es 2,56 menos ese canto, no los 2,70 supuestos.
- P1b se dibuja como viga (1,83 × 0,25) y no como pilar: si fuera macizo hasta el suelo, la cocina no tendría entrada. Medir su intradós.
- Baño nuevo: tabiques de 0,10 y puerta de 0,70 tomados del croquis, sin medir. Comprobar que la puerta abre hacia dentro sin chocar.
- Posición de P3: el 3,15 de planta baja y el 1,90 de planta alta se llevan 0,15; el 2,94 y el 3,20 se llevan 0,26. Se usa la cadena de PB.
- Del P3 a la escalera se midió 2,35 y en el plano salen 2,75. Los 0,40 no cierran contra la medianera Este.
- Pasillo de cocina: 0,78 m frente a los frigoríficos (0,74 de fondo) y hasta 0,92 en el resto. Por debajo de 0,90 con permiso del cliente.
- Tabica de la escalera: 2,56/17 = 0,151 m. Contar los peldaños en obra.
- Máquinas: medidas de las fichas de makro.es según su buscador (la web bloquea el acceso directo). Sin dato: alto de la columna B4, 0,55 estimado.

GRUPO SUMA

Reformas y proyectos · Málaga

PROYECTO

Reforma integral de local de hostelería

EMPLAZAMIENTO

Local en planta baja y altillo
Málaga

PLANO

PLANTA ALTA

Altillo +2,56 · estructura

LEYENDA

- Muro de carga / medianera
- Pilar o machón de hormigón
- Tabiquería
- Barandilla de vidrio
- Mesas y sillas (medidas promedio)
- Punto de luz
- Vacío sobre planta baja

SUPERFICIES Y ALTURAS

Forjado de planta alta	33,74 m²
Altillo diáfano	26,17 m²
Aseo (lavabo + inodoro)	3,92 m²
Almacén	2,59 m²
Nivel del forjado, medido	+2,56 m
Puestos de cowork	14

PILARES Y MACHONES (secciones en m)

P1 Machón del muro Oeste	0,30 × 0,60
P2 Pilastra del muro Sur	0,58 × 0,45
P3 Pilar central	0,65 × 1,07
P4 Machón de la medianera Este	0,20 × 0,60
P5 Pilar de fachada	0,60 × 1,00

NOTAS

Cotas en metros, tomadas sobre el levantamiento.


Nivel del forjado +2,56, medido en obra.

El forjado del altillo no cubre todo el local: la franja sur y oeste es un vacío a doble altura.

Mesa de cowork 2,40 × 1,00 para 8 puestos y dos


redondas de Ø 0,80 con 3 sillas. Medidas promedio.

Un colgante por mesa y empotrados en el resto.

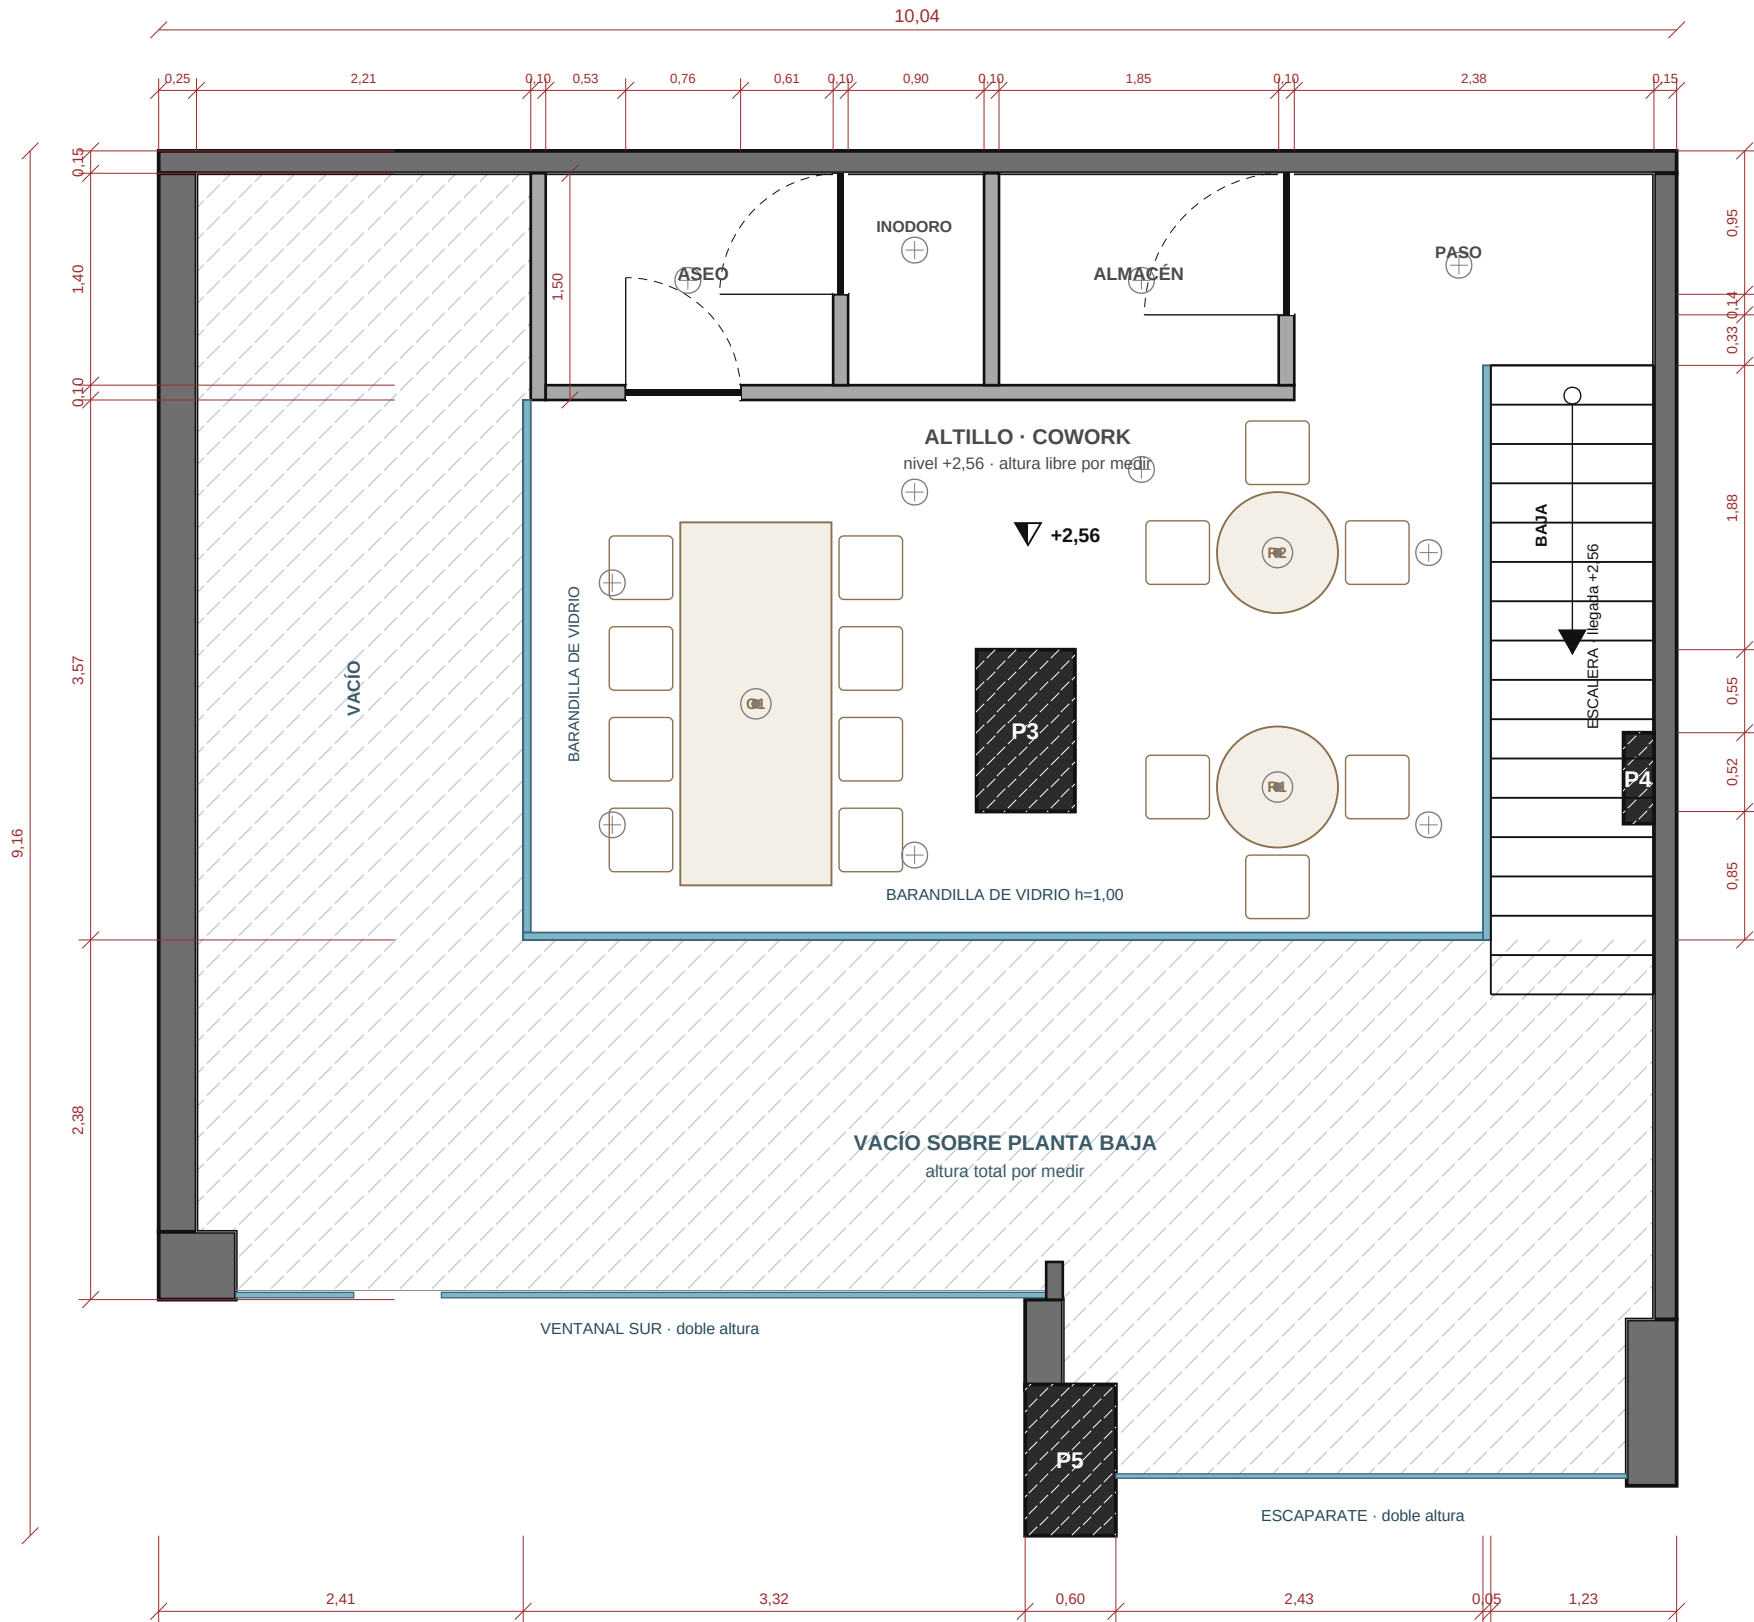

COMPROBAR EN OBRA Puntos en los que los vídeos del local no cuadran con el levantamiento, o que el levantamiento no recoge. Se dibuja el levantamiento por ser la única fuente acotada.

- Pared en L: en el segundo croquis termina en y=5,35 (3,66 m) y la barra sube hasta 4,75 con el paso de 0,60 entre ambas. Antes se midió 4,22.
- Canto del forjado del altillo. Con 2,56 m de suelo a suelo, la altura libre de planta baja es 2,56 menos ese canto, no los 2,70 supuestos.
- P1b se dibuja como viga (1,83 × 0,25) y no como pilar: si fuera macizo hasta el suelo, la cocina no tendría entrada. Medir su intradós.
- Baño nuevo: tabiques de 0,10 y puerta de 0,70 tomados del croquis, sin medir. Comprobar que la puerta abre hacia dentro sin chocar.
- Posición de P3: el 3,15 de planta baja y el 1,90 de planta alta se llevan 0,15; el 2,94 y el 3,20 se llevan 0,26. Se usa la cadena de PB.
- Del P3 a la escalera se midió 2,35 y en el plano salen 2,75. Los 0,40 no cierran contra la medianera Este.
- Pasillo de cocina: 0,78 m frente a los frigoríficos (0,74 de fondo) y hasta 0,92 en el resto. Por debajo de 0,90 con permiso del cliente.
- Tabica de la escalera: 2,56/17 = 0,151 m. Contar los peldaños en obra.
- Máquinas: medidas de las fichas de makro.es según su buscador (la web bloquea el acceso directo). Sin dato: alto de la columna B4, 0,55 estimado.

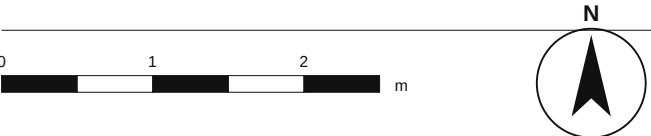

ESCALA	FECHA	PLANO
1:50 (A3)	15 set. 2026	02 / 04

GRUPO SUMA

Reformas y proyectos · Málaga

PROYECTO
Reforma integral de local de hostelería

EMPLAZAMIENTO
Local en planta baja y altílo
Málaga

PLANO
EQUIPAMIENTO

Barra y cocina · productos Makro

LEYENDA

- Bancada o mueble bajo
- Equipo refrigerado
- Encimera o tabla corrida
- Aparato (trazos: bajo encimera)
- Tabla de madera
- Muro de carga / medianera

HOLGURAS Y ALTURAS



Pasillo de cocina, mínimo	0,78 m
Paso de servicio en barra	1,02 m
Entrada a la cocina, bajo la viga	1,18 m
Altura de encimera	0,90 m
Borde inferior de la campana	2,00 m

NOTAS

Cada máquina es un producto real de makro.es con sus medidas de ficha; la web bloquea el acceso directo, así que las medidas vienen de su buscador. Confirmar en la ficha antes de comprar.

Cocción corrida en la medianera Norte bajo campana de 2,00 sobre K1 a K4. Mesada refrigerada de una sola pieza (2,54, la más larga de Makro) en la pared en L; quedan 0,42 libres. La tabla cubre K6.

Pasillo de cocina de 0,78 a 0,92: por debajo de 0,90 con permiso del cliente. Muro Oeste: 3,01 de aparatos en los 3,05 que hay hasta P1.

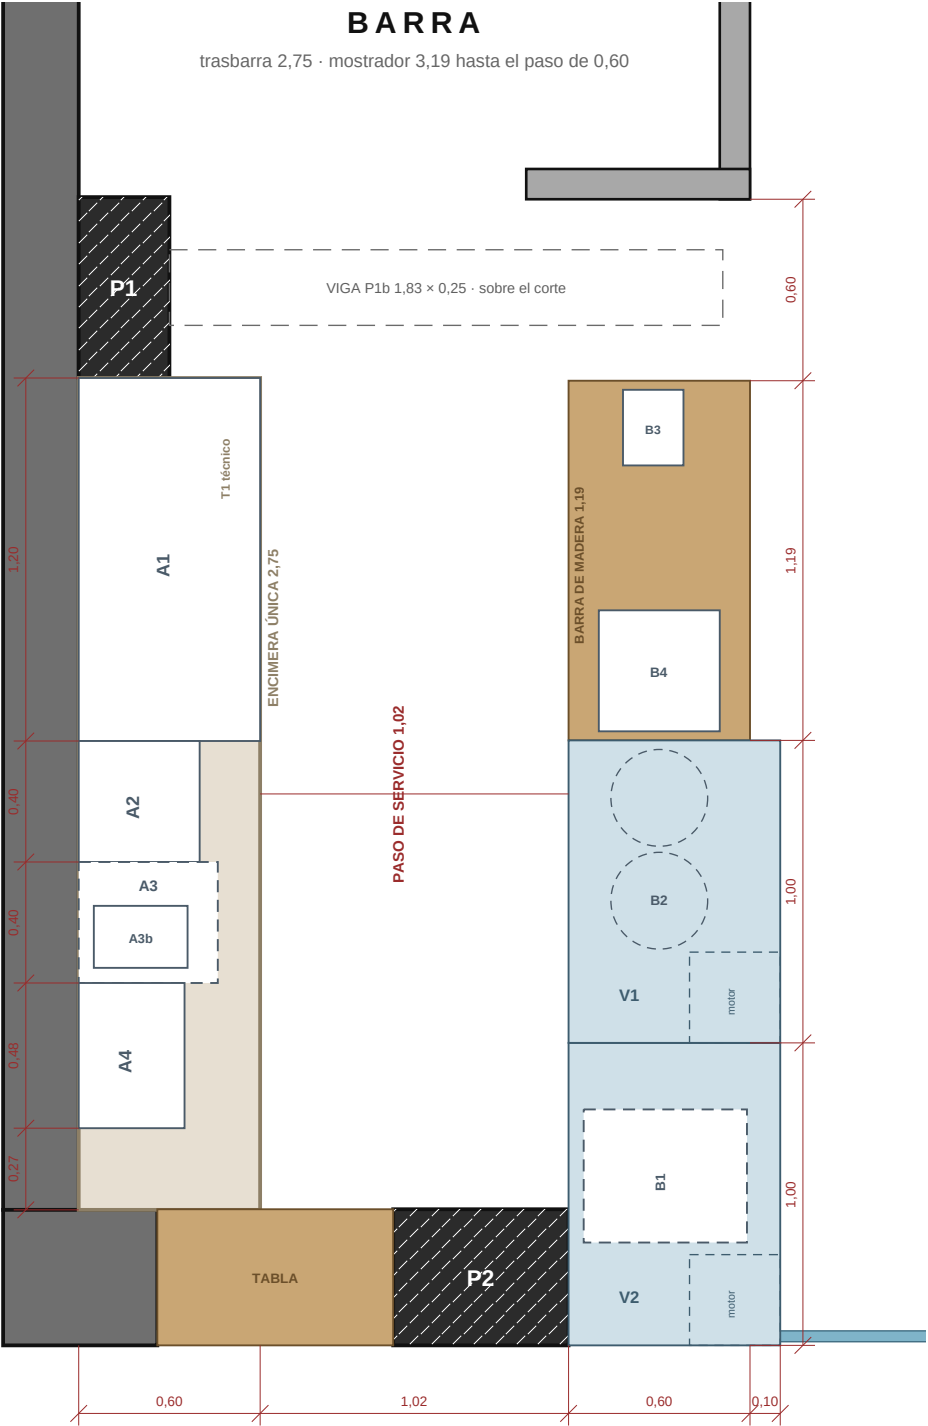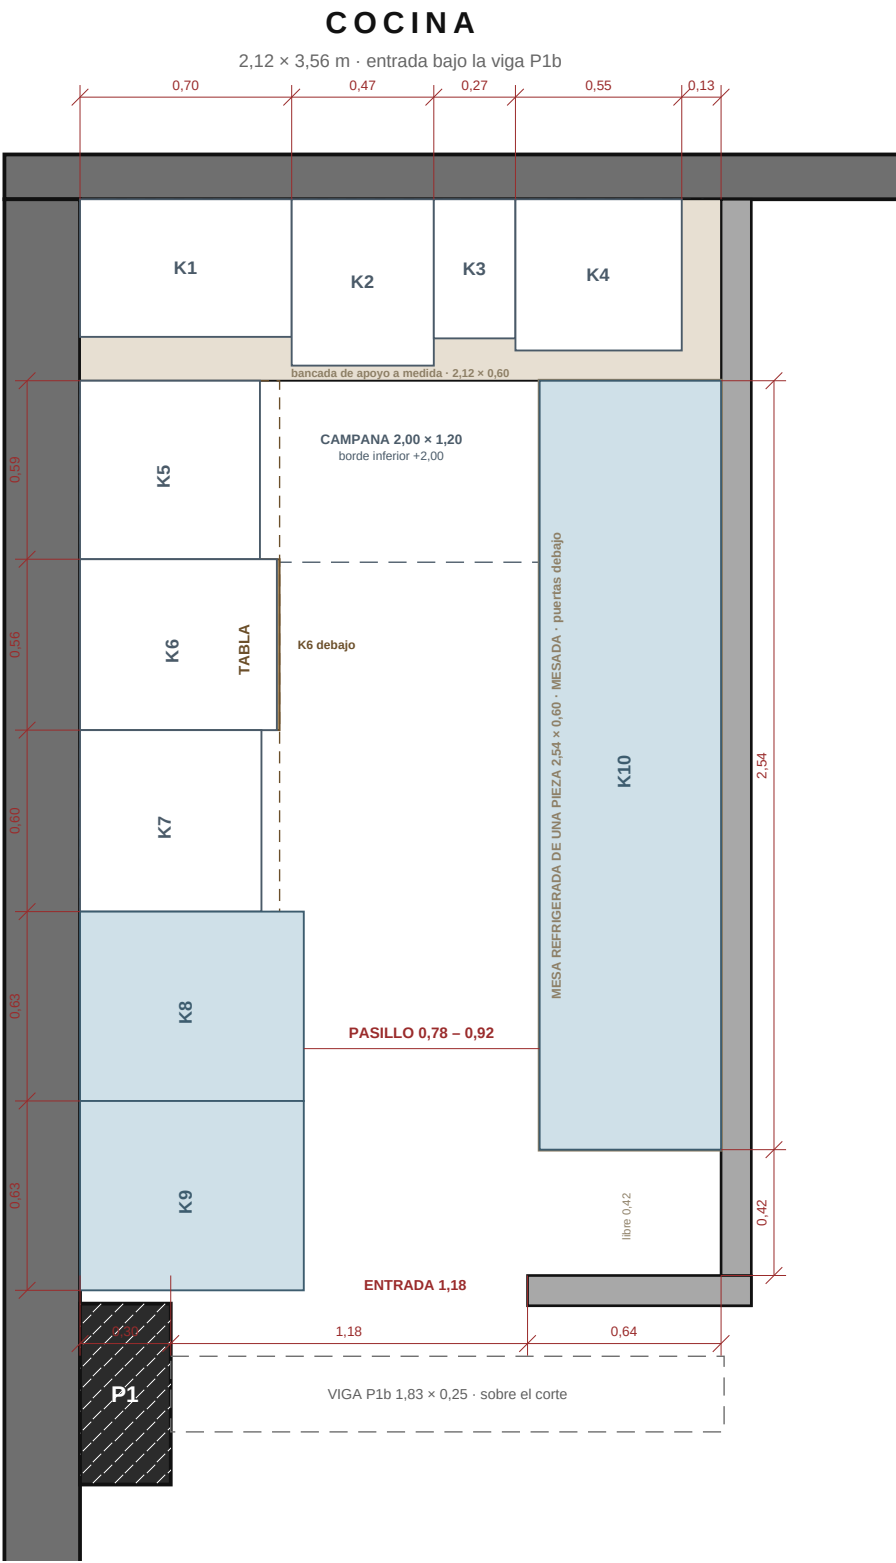

EQUIPAMIENTO · MAKRO

Ancho × fondo × alto en metros, de la ficha de makro.es. Vitrinas y cafetera ya compradas. Tablet y barriles con medida promedio. Enlaces en la lámina 04.

K1	Placa de inducción Bartscher, 2 zonas Ø230, 6 kW, 400 V	0,70 × 0,46 × 0,12	A1	Cafetera (comprada), 2 grupos	1,20 × 0,60 × 0,50
K2	Cocedor de pasta eléctrico METRO Professional GNC1008, 8 L, 4 cestos	0,47 × 0,55 × 0,38	A2	Lavamanos inox con grifo y pulsador de pedal, cuba Ø340	0,40 × 0,40 × 0,85
K3	Freidora profesional 1 cuba de 7 L, eléctrica	0,27 × 0,46 × 0,37	A3	Fabricador de hielo Gastro M CT694, 28 kg/24 h (bajo encimera)	0,40 × 0,46 × 0,67
K4	Plancha eléctrica Cleiton 50 cm, placa de 8 mm, sobremesa	0,55 × 0,50 × 0,33	A4	Exprimidor de naranjas Mizumo Next Gen	0,48 × 0,35 × 0,73
KC	Campana extractora industrial recta, sin turbina, AISI-304 satinado, 2 × 1,2 m	2,00 × 1,20 × 0,50	A3b	Licuada industrial Sammic Li-240	0,20 × 0,31 × 0,36
K5	Horno de convección eléctrico industrial, 4 bandejas 45 × 33	0,59 × 0,59 × 0,57	V2	Vitrina refrigerada (comprada), 1,00 × 0,70; debajo, lavavasos	1,00 × 0,70 × 1,25
K6	Lavavajillas industrial ST500, cesta 50 × 50, bajo la tabla	0,56 × 0,65 × 0,86	V1	Vitrina refrigerada (comprada), 1,00 × 0,70; debajo, barriles	1,00 × 0,70 × 1,25
K7	Fregadero industrial Distform gama 600, 1 cubeta 50 × 40, con puerta, peto 105	0,60 × 0,60 × 0,85	B1	Lavavasos Elettrobar FAST 40, cesta 40 × 40 (bajo la vitrina V2)	0,44 × 0,54 × 0,67
K8	Armario refrigerado vertical Edenox APS-451 I, inox, 1 puerta, 395 L	0,63 × 0,74 × 1,86	B2	Barriles de cerveza de 30 L, Ø 0,32 (bajo la vitrina V1)	0,32 × 0,32 × 0,60
K9	Armario refrigerado vertical Edenox APS-451 I, inox, 1 puerta, 395 L	0,63 × 0,74 × 1,86	B3	Caja: tablet sobre soporte	0,25 × 0,20 × 0,25
K10	Mesa refrigerada Infrico 4 puertas, AISI-304, peto 100 mm, -2/+8 °C, 530 L	2,54 × 0,60 × 0,85	B4	Columna de cerveza en T de 3 grifos, bandeja 40 × 40 (no la hay de 2 en Makro)	0,40 × 0,40 × 0,55

ESCALA

1:25 (A3)

FECHA

15 set. 2026

PLANO

03 / 04

LISTA DE EQUIPAMIENTO · MAKRO

Todo lo que hay que comprar para la barra y la cocina, con la ficha de makro.es de cada producto. Medidas en metros, ancho × fondo × alto. Los enlaces de la última columna son clicables en el PDF.

EQUIPOS DIBUJADOS EN LAS LÁMINAS 01 Y 03

RÓTULO	PRODUCTO	MEDIDAS	DÓNDE VA	FICHA EN MAKRO.ES
K1	Placa de inducción Bartscher, 2 zonas Ø230, 6 kW, 400 V	0,70 × 0,46 × 0,12	Cocina · cocción, medianera Norte, bajo la campana, 1º desde el Oeste	https://www.makro.es/marketplace/product/623ef78b-af50-4e27-a2c5-b3a45089ba59
K2	Cocedor de pasta eléctrico METRO Professional GNC1008, 8 L, 4 cestos	0,47 × 0,55 × 0,38	Cocina · cocción, bajo la campana, 2º	https://www.makro.es/marketplace/product/85f3fb44-3f09-463c-ab29-53822c8c1ce7
K3	Freidora profesional 1 cuba de 7 L, eléctrica	0,27 × 0,46 × 0,37	Cocina · cocción, bajo la campana, 3º	https://www.makro.es/marketplace/product/57e9d9ed-d483-4f88-a049-5597b3a7ad18
K4	Plancha eléctrica Cleiton 50 cm, placa de 8 mm, sobremesa	0,55 × 0,50 × 0,33	Cocina · cocción, bajo la campana, 4º, contra la pared en L	https://www.makro.es/marketplace/product/acd212b2-73a4-42bc-bea7-329d5ab4771d
KC	Campana extractora industrial recta, sin turbina, AISI-304 satinado, 2 × 1,2 m	2,00 × 1,20 × 0,50	Cocina · campana mural corrida sobre K1 a K4, borde inferior a +2,00	https://www.makro.es/marketplace/product/a8240770-cb5f-491b-926d-83b1e1e00a22
K5	Horno de convección eléctrico industrial, 4 bandejas 45 × 33	0,59 × 0,59 × 0,57	Cocina · muro Oeste, esquina Norte, sobre soporte	https://www.makro.es/marketplace/product/e3c35b3b-14d3-4e2b-a109-373a863ddff9
K6	Lavavajillas industrial ST500, cesta 50 × 50, bajo la tabla	0,56 × 0,65 × 0,86	Cocina · muro Oeste, bajo la tabla que enlaza fregadero y horno	https://www.makro.es/marketplace/product/b6893f6e-6c55-499e-8e8b-4e246d107961
K7	Fregadero industrial Distform gama 600, 1 cubeta 50 × 40, con puerta, peto 105	0,60 × 0,60 × 0,85	Cocina · muro Oeste, al Sur de la tabla (0,60 para que entren K8 y K9)	https://www.makro.es/marketplace/product/3efac5b4-e702-4af6-9dd9-533709488190
K8	Armario refrigerado vertical Edenox APS-451 I, inox, 1 puerta, 395 L	0,63 × 0,74 × 1,86	Cocina · muro Oeste, vertical, al Sur del fregadero	https://www.makro.es/marketplace/product/2e636462-1801-45f6-a3d8-15413909cb8c
K9	Armario refrigerado vertical Edenox APS-451 I, inox, 1 puerta, 395 L	0,63 × 0,74 × 1,86	Cocina · muro Oeste, vertical, contra P1	https://www.makro.es/marketplace/product/2e636462-1801-45f6-a3d8-15413909cb8c
K10	Mesa refrigerada Infrico 4 puertas, AISI-304, peto 100 mm, -2/+8 °C, 530 L	2,54 × 0,60 × 0,85	Cocina · pared en L, de una pieza, como mesada; 0,42 libras junto al doblez	https://www.makro.es/marketplace/product/764bc52f-1287-4e08-89dc-c2e453dfea49
A1	Cafetera (comprada), 2 grupos	1,20 × 0,60 × 0,50	Barra · trasbarra, extremo Norte, sobre el módulo técnico T1	ya comprado / medida promedio, sin ficha
A2	Lavamanos inox con grifo y pulsador de pedal, cuba Ø340	0,40 × 0,40 × 0,85	Barra · trasbarra, al Sur de la cafetera	https://www.makro.es/marketplace/product/6105678f-3159-4172-a17a-f400760f0b35
A3	Fabricador de hielo Gastro M CT694, 28 kg/24 h (bajo encimera)	0,40 × 0,46 × 0,67	Barra · trasbarra, bajo la encimera, al Sur del lavamanos	https://www.makro.es/marketplace/product/e3db53e1-8f64-4495-bb2c-59fe355a32e2
A4	Exprimidor de naranjas Mizumo Next Gen	0,48 × 0,35 × 0,73	Barra · trasbarra, extremo Sur	https://www.makro.es/marketplace/product/a7c3e878-0cdd-4f7e-b013-897ae4f6120d
A3b	Licuadaora industrial Sammic Li-240	0,20 × 0,31 × 0,36	Barra · trasbarra, sobre la encimera, encima de la hielera	https://www.makro.es/marketplace/product/2b8d9850-b422-4738-b716-c30da9857300
V2	Vitrina refrigerada (comprada), 1,00 × 0,70; debajo, lavavasos	1,00 × 0,70 × 1,25	Barra · mostrador delantero, junto a P2 (Sur); lavavasos debajo	ya comprado / medida promedio, sin ficha
V1	Vitrina refrigerada (comprada), 1,00 × 0,70; debajo, barriles	1,00 × 0,70 × 1,25	Barra · mostrador delantero, al Norte de V2; barriles debajo	ya comprado / medida promedio, sin ficha
B1	Lavavasos Elettrobar FAST 40, cesta 40 × 40 (bajo la vitrina V2)	0,44 × 0,54 × 0,67	Barra · bajo la vitrina V2	https://www.makro.es/marketplace/product/e858e346-8373-4e64-aa03-6f9a559e168e
B2	Barriles de cerveza de 30 L, Ø 0,32 (bajo la vitrina V1)	0,32 × 0,32 × 0,60	Barra · bajo la vitrina V1	ya comprado / medida promedio, sin ficha
B3	Caja: tablet sobre soporte	0,25 × 0,20 × 0,25	Barra · barra de madera, extremo Norte, junto a la viga P1b	ya comprado / medida promedio, sin ficha
B4	Columna de cerveza en T de 3 grifos, bandeja 40 × 40 (no la hay de 2 en Makro)	0,40 × 0,40 × 0,55	Barra · barra de madera, extremo Sur	https://www.makro.es/marketplace/product/f2d9d7ba-6f4f-4feb-b032-641cc4d828fe

ALTERNATIVAS CON LA MISMA FUNCIÓN · no dibujadas

SUSTITUYE	PRODUCTO	MEDIDAS	DÓNDE VA	FICHA EN MAKRO.ES
K10	Mesa refrigerada Vaiotec EASYLINE, inox, 4 puertas, GN 1/1, 553 L	2,23 × 0,70 × 0,85	Cocina · pared en L, en lugar de K10; fondo 0,70 como la foto; 0,73 libras	https://www.makro.es/marketplace/product/230e627d-7291-43e0-a2b4-ebb6fe783f27
K10	METRO Professional GCC3100, inox, 3 puertas, 334 L (la de la foto, refrigerada)	1,79 × 0,70 × 0,85	Cocina · pared en L, en lugar de K10; deja 1,16 libras	https://www.makro.es/marketplace/product/176b30f1-81b0-4a52-916e-80722d9a9240
K8/K9	Armario frigorífico ventilado 400 L, acero inoxidable (Diamond)	0,63 × 0,74 × 1,93	Cocina · muro Oeste, en lugar de K8 y K9; misma huella que el Edenox	https://www.makro.es/marketplace/product/8969b667-b5cb-4e83-b599-3dd45c112547
K8/K9	Armario refrigerado AR400L Clima Hostelería, lacado blanco (no inox), 360 L	0,60 × 0,61 × 1,87	Cocina · muro Oeste, en lugar de K8 y K9; con éste cabe el fregadero de 0,70	https://www.makro.es/marketplace/product/d48c3c0c-7975-4c22-89c7-64676c23681f
K7	Fregadero Royal Catering, 1 cubeta 50 × 50, 70 × 70 (alto sin dato en ficha)	0,70 × 0,70 × 0,85	Cocina · muro Oeste, en lugar de K7; sólo con los frigoríficos AR400L	https://www.makro.es/marketplace/product/987fd316-3c44-48e2-a628-d88809ed245c

A MEDIDA · no se compran en Makro

- Bancada de apoyo de la línea de cocción: 2,12 × 0,60, acero inoxidable.
- Tabla de madera sobre el lavavajillas K6, del fregadero al horno: 0,57 × 0,66.
- Encimera única de la trasbarra: 2,75 × 0,60.
- Barra de madera del mostrador delantero: 1,19 × 0,60.
- Tabla de P2 al muro: 0,78 × 0,45.
- Módulo técnico T1 bajo la cafetera: 0,60 de ancho.

VERIFICACIÓN DE LOS ENLACES

makro.es responde 403 a cualquier acceso desde un servidor (curl, Playwright o un navegador en la nube), así que las fichas no se pueden abrir desde el entorno de trabajo. Cada enlace se verificó buscando su identificador con el buscador restringido a makro.es: los 21 devuelven exactamente su URL con el título del producto (LISTA_MAKRO.md). Precios y stock no se han podido leer con fiabilidad: confirmar en la ficha antes de comprar. Si un enlace dejara de funcionar, buscar el título literal de la ficha en makro.es.

GRUPO SUMA

Reformas y proyectos · Málaga

PROYECTO

Reforma integral de local de hostelería

EMPLAZAMIENTO

Local en planta baja y altillo Málaga

PLANO

EQUIPAMIENTO

Lista de compra · enlaces a makro.es

RESUMEN

Fichas distintas de Makro	16
Unidades a comprar en Makro	17
Ya comprado	cafetera y 2 vitrinas
Medida promedio	barriles y tablet
A medida	6 elementos

NOTAS

Medidas ancho × fondo × alto en metros, tomadas de la ficha de makro.es. Los enlaces de la última columna son clicables en el PDF; en papel, copiar la dirección o buscar el título en makro.es. Vitrinas y cafetera ya compradas, con las medidas del cliente. Barriles y tablet con medida promedio. Confirmar precio y stock antes de comprar.

ESCALA	FECHA	PLANO
sin escala	15 set. 2026	04 / 04