

GRUPO SUMA

Reformas y proyectos · Málaga

PROYECTO
Reforma integral de local de hostelería

EMPLAZAMIENTO
Local en planta baja y altílo
Málaga

PLANO
EQUIPAMIENTO
Barra y cocina · productos Makro

- LEYENDA
- Bancada o mueble bajo
 - Equipo refrigerado
 - Encimera o tabla corrida
 - Aparato (trazos: bajo encimera)
 - Tabla de madera
 - Muro de carga / medianera

HOLGURAS Y ALTURAS

Pasillo de cocina, mínimo	0,78 m
Paso de servicio en barra	1,02 m
Entrada a la cocina, bajo la viga	1,18 m
Altura de encimera	0,90 m
Borde inferior de la campana	2,00 m




NOTAS

Cada máquina es un producto real de makro.es con sus medidas de ficha; la web bloquea el acceso directo, así que las medidas vienen de su buscador. Confirmar en la ficha antes de comprar.

Cocción corrida en la medianera Norte bajo campana de 2,00 sobre K1 a K4. Mesada refrigerada de una sola pieza (2,54, la más larga de Makro) pegada al doblez de la L; 0,42 libres junto a la cocción.

K6 va bajo el escurridor del fregadero K7.

Pasillo de cocina de 0,78 a 0,92: por debajo de 0,90 con permiso del cliente. Muro Oeste: 3,01 de aparatos en los 3,05 que hay hasta P1.

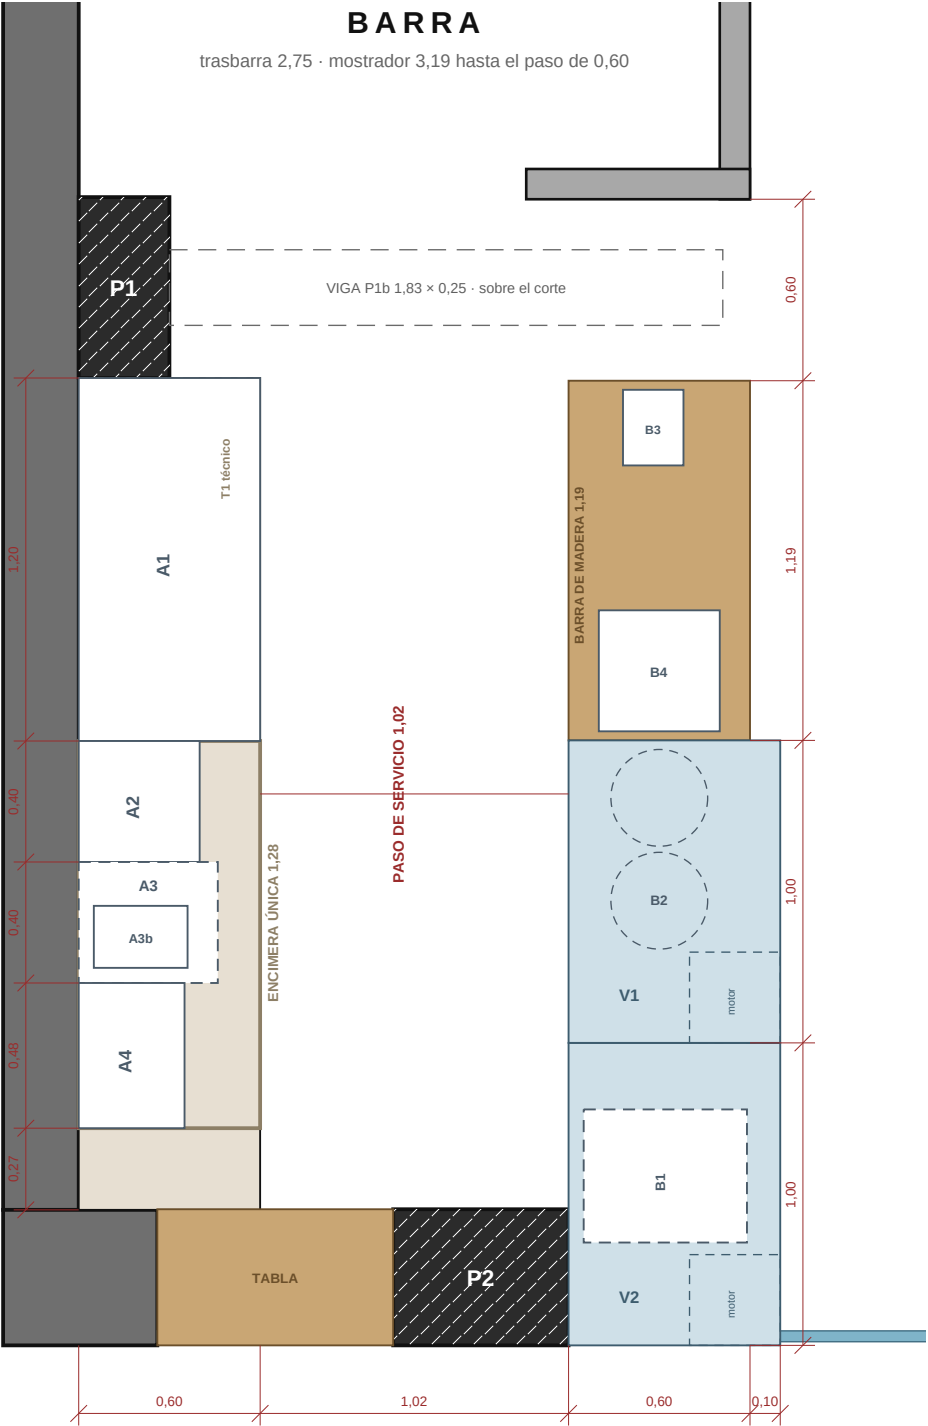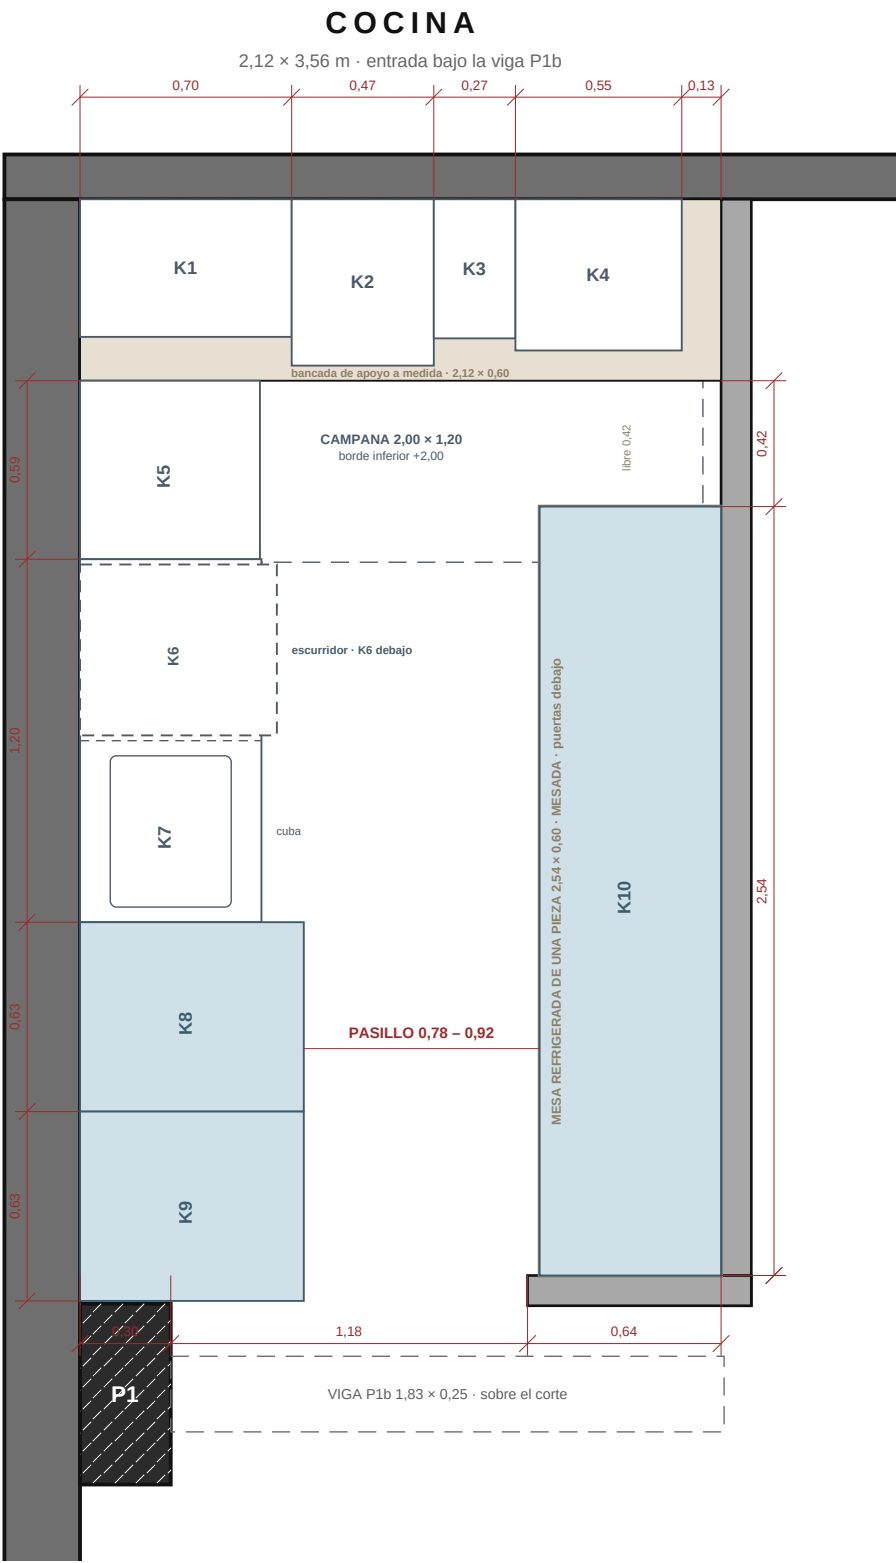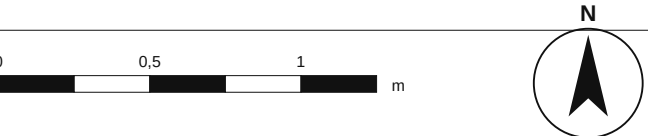

EQUIPAMIENTO · MAKRO Ancho × fondo × alto en metros, de la ficha de makro.es. Vitrinas y cafetera ya compradas. Tablet y barriles con medida promedio. Enlaces en la lámina 04.

K1	Placa de inducción Bartscher, 2 zonas Ø230, 6 kW, 400 V	0,70 × 0,46 × 0,12	A1	Cafetera (comprada), 2 grupos	1,20 × 0,60 × 0,50
K2	Cocedor de pasta eléctrico METRO Professional GNC1008, 8 L, 4 cestos	0,47 × 0,55 × 0,38	A2	Lavamanos inox con grifo y pulsador de pedal, cuba Ø340	0,40 × 0,40 × 0,85
K3	Freidora profesional 1 cuba de 7 L, eléctrica	0,27 × 0,46 × 0,37	A3	Fabricador de hielo Gastro M CT694, 28 kg/24 h (bajo encimera)	0,40 × 0,46 × 0,67
K4	Plancha eléctrica Cleiton 50 cm, placa de 8 mm, sobremesa	0,55 × 0,50 × 0,33	A4	Exprimidor de naranjas Mizumo Next Gen	0,48 × 0,35 × 0,73
KC	Campana extractora industrial recta, sin turbina, AISI-304 satinado, 2 × 1,2 m	2,00 × 1,20 × 0,50	A3b	Licuada industrial Sammic Li-240	0,20 × 0,31 × 0,36
K5	Horno de convección eléctrico industrial, 4 bandejas 45 × 33	0,59 × 0,59 × 0,57	V2	Vitrina refrigerada (comprada), 1,00 × 0,70; debajo, lavavasos	1,00 × 0,70 × 1,25
K7	Fregadero con hueco de lavavajillas, cuba izquierda (Ref. AAA0045913963)	1,20 × 0,60 × 0,85	V1	Vitrina refrigerada (comprada), 1,00 × 0,70; debajo, barriles	1,00 × 0,70 × 1,25
K6	Lavavajillas industrial ST500, cesta 50 × 50, bajo el escurridor de K7	0,56 × 0,65 × 0,86	B1	Lavavasos Elettrobar FAST 40, cesta 40 × 40 (bajo la vitrina V2)	0,44 × 0,54 × 0,67
K8	Armario refrigerado vertical Edenox APS-451 I, inox, 1 puerta, 395 L	0,63 × 0,74 × 1,86	B2	Barriles de cerveza de 30 L, Ø 0,32 (bajo la vitrina V1)	0,32 × 0,32 × 0,60
K9	Armario refrigerado vertical Edenox APS-451 I, inox, 1 puerta, 395 L	0,63 × 0,74 × 1,86	B3	Caja: tablet sobre soporte	0,25 × 0,20 × 0,25
K10	Mesa refrigerada Infrico 4 puertas, AISI-304, peto 100 mm, -2/+8 °C, 530 L	2,54 × 0,60 × 0,85	B4	Columna de cerveza en T de 3 grifos, bandeja 40 × 40 (no la hay de 2 en Makro)	0,40 × 0,40 × 0,55