

GRUPO SUMA

Reformas y proyectos · Málaga

PROYECTO

Reforma integral de local de hostelería

EMPLAZAMIENTO

Local en planta baja y altílo
Málaga

PLANO

PLANTA BAJA

Estado actual · estructura

LEYENDA

- Muro de carga / medianera
- Pilar o machón de hormigón
- Pared en L nueva (apoyo del vidrio)
- Carpintería acristalada
- Espacio de doble altura
- Forjado sobre el corte
- Reserva de espacio del cliente
- Mesas y sillas (medidas promedio)
- Itinerario accesible $\geq 1,20$ · giro $\varnothing 1,50$
- Punto de luz: colgante / empotrado

SUPERFICIES Y ALTURAS

Planta baja, dentro de muros	75,63 m ²
Zona de doble altura	37,80 m ²
Suelo a suelo, medido en obra	2,56 m
Altura libre bajo forjado	2,56 – canto
Pared en L, altura	1,22 m
Plazas sentadas en planta baja	28
Acristalamiento de fachada	≈ 4,70 m

PILARES Y MACHONES (secciones en m)

P1 Machón del muro Oeste	0,30 × 0,60
P2 Pilastra del muro Sur	0,58 × 0,45
P3 Pilar central	0,65 × 1,07
P4 Machón de la medianera Este	0,20 × 0,60
P5 Pilar de fachada	0,60 × 1,00

NOTAS

Cotas en metros; pilares, pared en L, ventanal y puerta medidos en obra (14 set. 2026), el resto del levantamiento previo. $\pm 0,00$ en el pavimento de planta baja; sección horizontal a 1,20 m. Mesas cuádruples de $1,20 \times 0,70$ (medida promedio); un colgante por mesa y empotrados en los pasos. Itinerario accesible de 1,20 desde la puerta a la barra, al baño y a la plaza PMR de M2, con giros de $\varnothing 1,50$ en la entrada y ante el baño (DB-SUA). El baño dibujado no es accesible: no cabe el giro. Equipamiento de barra y cocina en la lámina 03; lista de compra con enlaces en la lámina 04.



ESCALA


1:50 (A3)

FECHA

15 set. 2026

PLANO

01 / 04

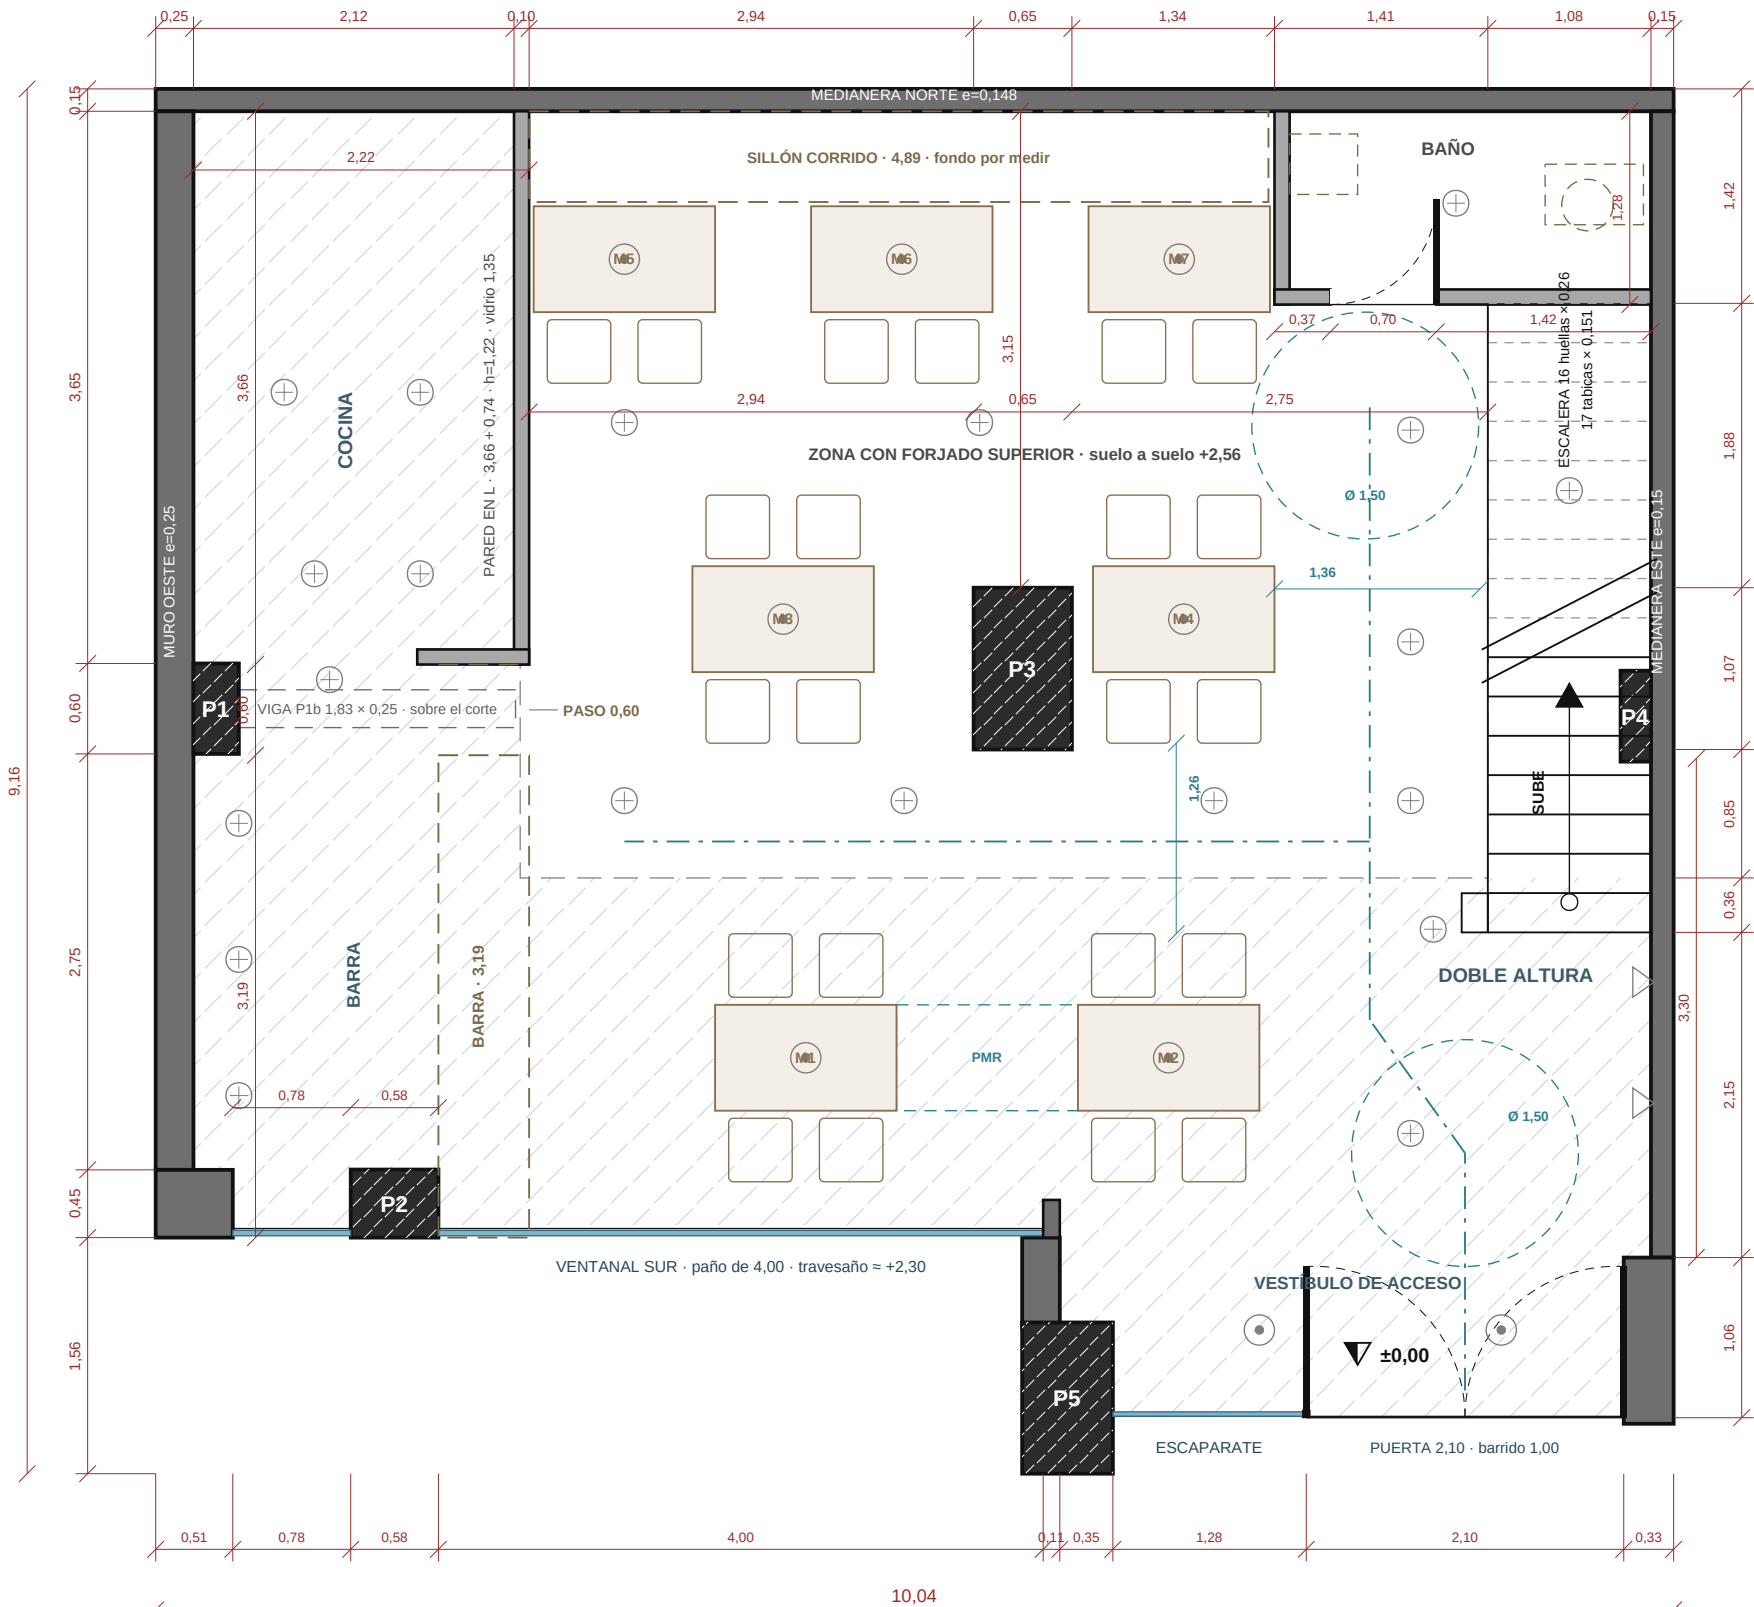

COMPROBAR EN OBRA Puntos en los que los vídeos del local no cuadran con el levantamiento, o que el levantamiento no recoge. Se dibuja el levantamiento por ser la única fuente acotada.

- Pared en L: en el segundo croquis termina en $y=5,35$ (3,66 m) y la barra sube hasta 4,75 con el paso de 0,60 entre ambas. Antes se midió 4,22.
- Canto del forjado del altílo. Con 2,56 m de suelo a suelo, la altura libre de planta baja es 2,56 menos ese canto, no los 2,70 supuestos.
- P1b se dibuja como viga ($1,83 \times 0,25$) y no como pilar: si fuera macizo hasta el suelo, la cocina no tendría entrada. Medir su intradós.
- Baño nuevo: tabiques de 0,10 y puerta de 0,70 tomados del croquis, sin medir. Comprobar que la puerta abre hacia dentro sin chocar.
- Posición de P3: el 3,15 de planta baja y el 1,90 de planta alta se llevan 0,15; el 2,94 y el 3,20 se llevan 0,26. Se usa la cadena de PB.
- Del P3 a la escalera se midió 2,35 y en el plano salen 2,75. Los 0,40 no cierran contra la medianera Este.
- Pasillo de cocina: 0,78 m frente a los frigoríficos (0,74 de fondo) y hasta 0,92 en el resto. Por debajo de 0,90 con permiso del cliente.
- Tabica de la escalera: $2,56/17 = 0,151$ m. Contar los peldaños en obra.
- Máquinas: medidas de las fichas de makro.es según su buscador (la web bloquea el acceso directo). Sin dato: alto de la columna B4, 0,55 estimado.