

PROYECTO

Reforma integral de local de hostelería

EMPLAZAMIENTO

Local en planta baja y altillo Málaga

PLANO

PLANTA BAJA

Estado actual · estructura

LEYENDA

- Muro de carga / medianera
- Pilar, machón o montante
- Pared en L y tabiquería
- Carpintería acristalada
- Espacio de doble altura
- Forjado, viga y pizarra sobre el corte
- Reserva de espacio del cliente
- Mesas dobles de 0,70 × 0,70 y sillas
- Nevera A7 · 0,54 × 0,58 (cara Sur de P3)
- Recorrido de sala · 0,70 por el Norte
- Luz empotrada y colgante
- Aire acondicionado (cassette de techo)
- Toldo desplegado: lona, barra y poste

SUPERFICIES Y ALTURAS



Planta baja, dentro de muros	73,09 m²
Zona de doble altura	26,75 m²
Suelo a suelo, medido en obra	2,56 m
Altura libre bajo forjado	2,56 – canto
Pared en L, altura	1,22 m
Mesas dobles / plazas sentadas	8 / 20
Acristalamiento de fachada	≈ 4,70 m

PILARES Y MACHONES (secciones en m)

P1 Machón del muro Oeste	0,30 × 0,60
P2 Pilastra del muro Sur	0,58 × 0,45
P3 Pilar central	0,65 × 1,07
P4 Machón de la medianera Este	0,20 × 0,60
P5 Pilar de fachada	0,60 × 1,00

NOTAS

Cotas en metros: del cliente (19 set.) y, el resto, del levantamiento. Sección a 1,20 m. Muro Norte macizo: 0,20, y 0,15 en la cocina por el hundimiento de 0,05. La pared en L mide 3,60 y llega al muro. Mesas dobles de 0,70 × 0,70; sillón de 0,60 de fondo sin medir. A7 deja 0,45 hasta M2: a la barra, por el Norte (0,70). Baño no accesible. 29 set.: luces de sala centradas en las mesas; puerta al fondo del vestíbulo; retorno de vidrio junto a P5; montante y cerramiento bajo en la escalera; techo de pladur en la cocina; toldos desplegados.

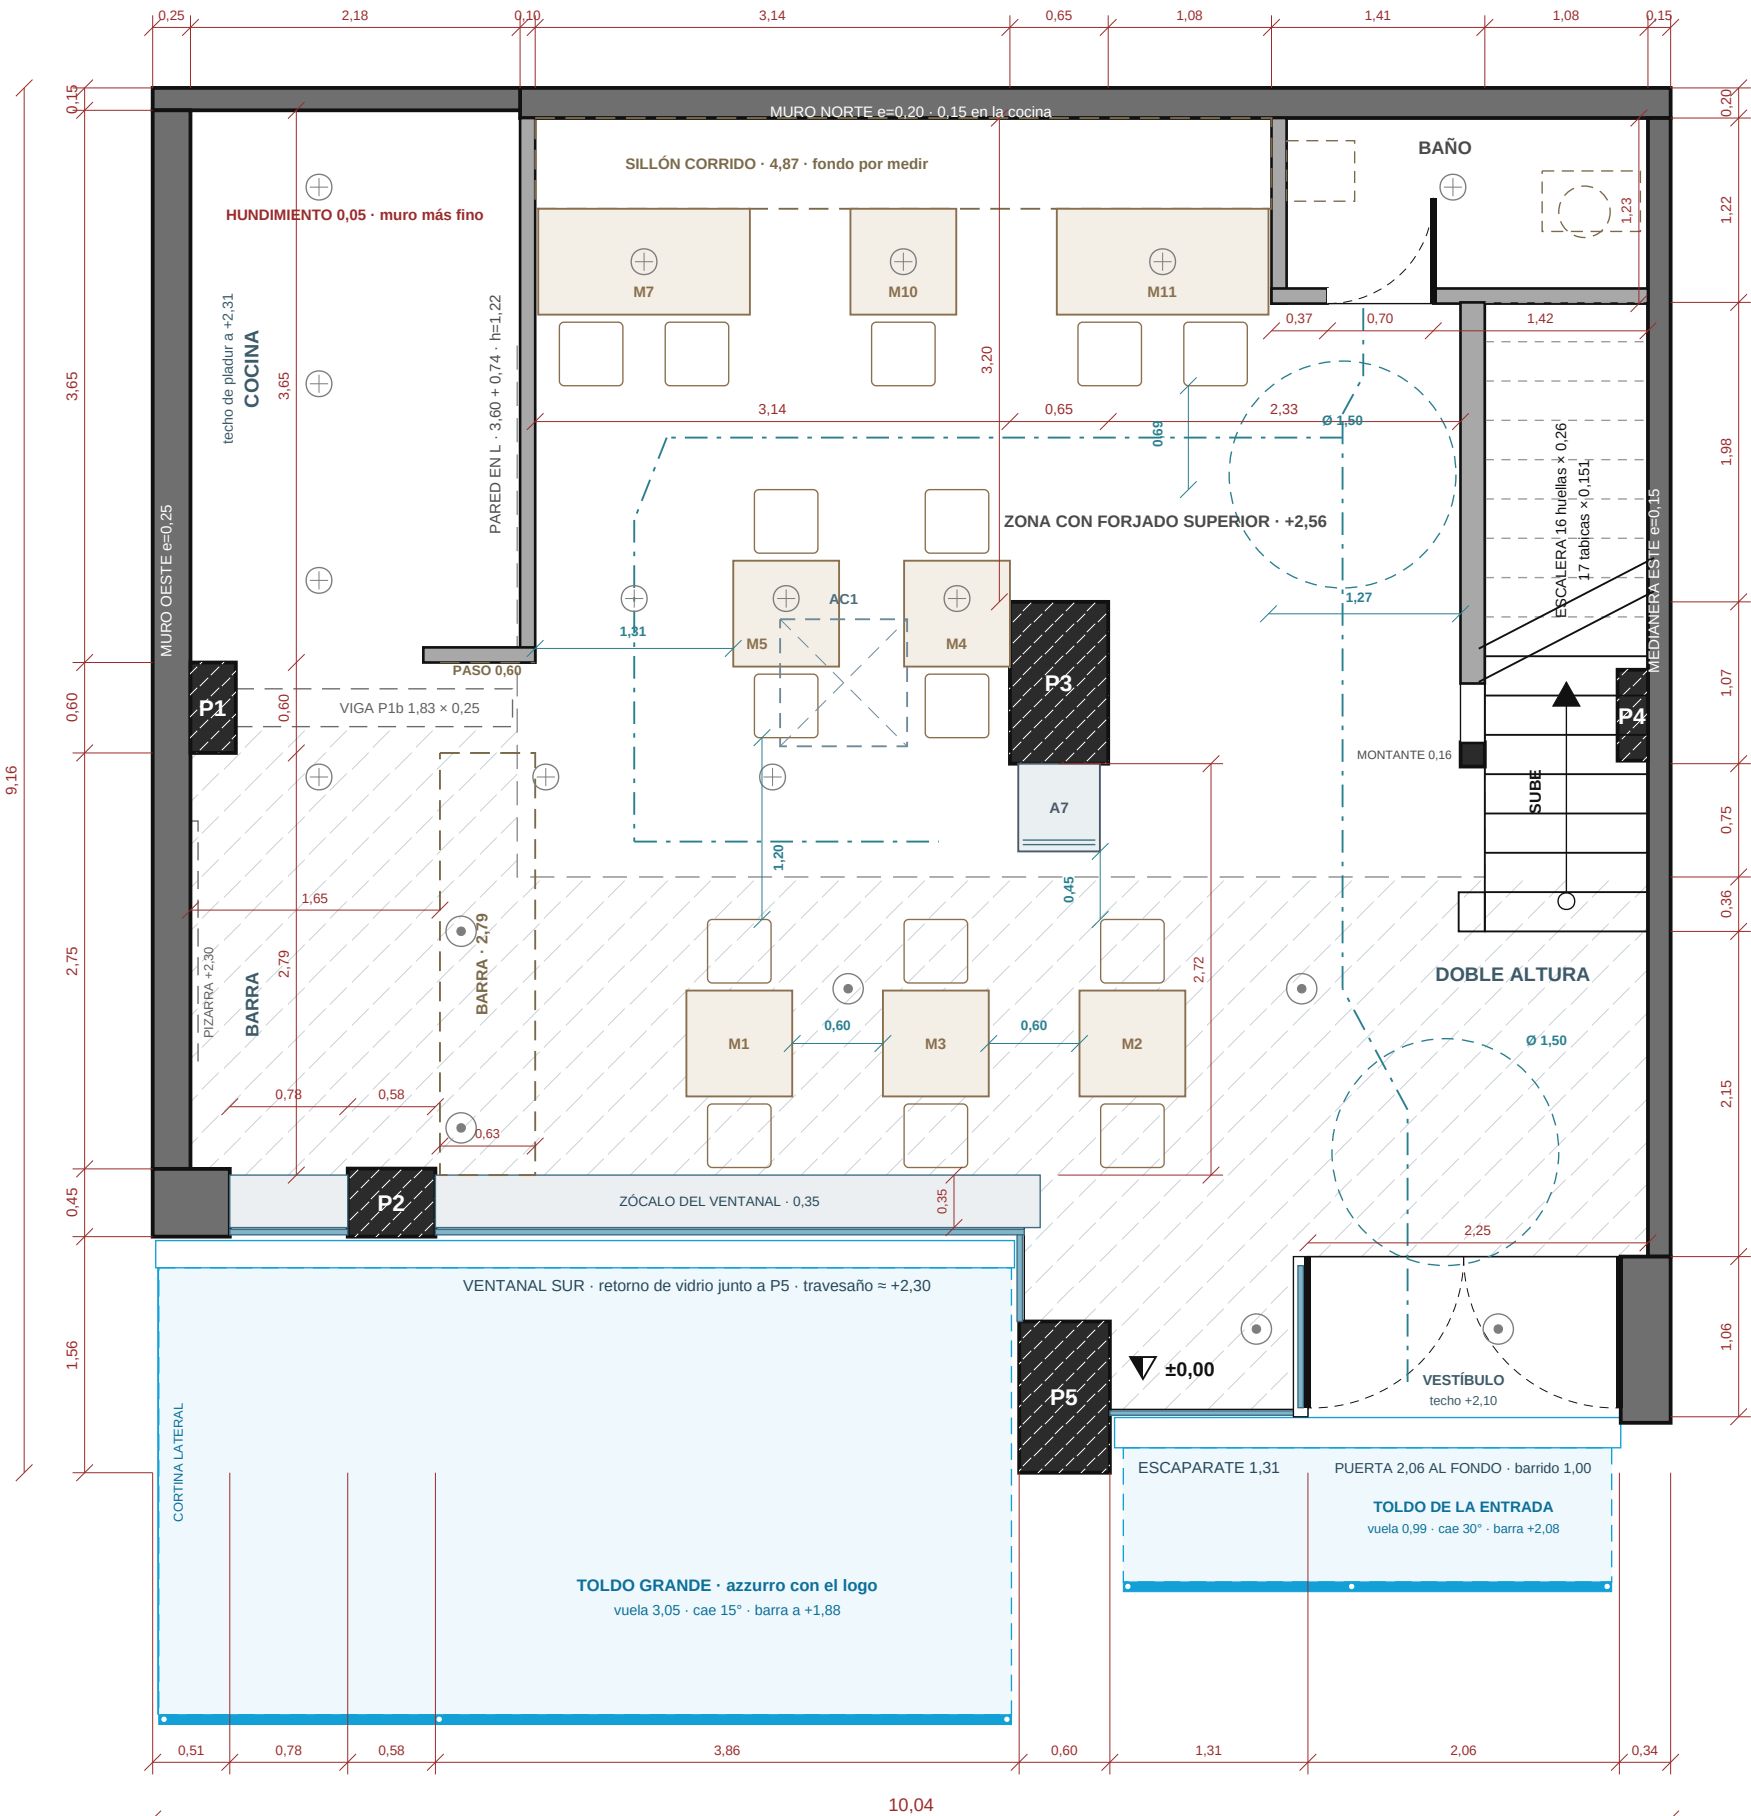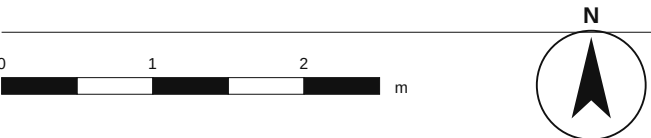

COMPROBAR EN OBRA Puntos en los que los vídeos del local no cuadran con el levantamiento, o que el levantamiento no recoge. Se dibuja el levantamiento por ser la única fuente acotada.

- Muro Norte: macizo hasta el solar, 0,148 en la cocina (el del levantamiento) y 0,199 en el resto. Medir ese espesor y el hundimiento de 0,05 entre los dos.
- Canto del forjado del altillo. Con 2,56 m de suelo a suelo, la altura libre de planta baja es 2,56 menos ese canto, no los 2,70 supuestos.
- P1b se dibuja como viga (1,83 × 0,25) y no como pilar: si fuera macizo hasta el suelo, la cocina no tendría entrada. Medir su intradós.
- Zócalo del ventanal: 0,347 desde el vidrio, deducido de los 2,72 de P3 a su cara interior; sobresale 0,16 del muro del ventanal (0,25). Medirlo directamente.
- Muro Oeste de la cocina: los cuatro aparatos suman 3,04 y entre P1 y la bancada hay 3,05. Entran con 1 cm de holgura: confirmar los anchos reales antes de comprar.
- La pared en L queda 0,10 al Este del borde del forjado del levantamiento: el vidrio de 1,35 sobre ella (2,57 en total) no pasa bajo el altillo. Medir ese borde.
- Vestíbulo: los 1,31 y 2,23 del cliente suman 3,54 y de P5 al muro Este hay 3,559. Se dibuja el 1,31 medido y el resto queda en 2,25, 2 cm más que su medida.
- P3 no se mueve: los 3,23 a la medianera dan 3,25 medidos al muro desnudo (2,98 al trasdosado) y los 3,65 a P5 se dibujan 3,69. Confirmar a qué cara se midió.
- Aire acondicionado: un solo cassette de 4 vías, empotrado en el forjado al Oeste de P3. Posición y panel (0,84) sacados de las fotos: medirlas en obra.