

GRUPO SUMA

Reformas y proyectos · Málaga

PROYECTO

Reforma integral de local de hostelería

EMPLAZAMIENTO

Local en planta baja y altílo Málaga

PLANO

PLANTA ALTA

Altílo +2,56 · estructura

LEYENDA

- Muro de carga / medianera
- Pilar o machón de hormigón
- Tabiquería
- Barandilla de vidrio
- Mesas y sillas (medidas promedio)
- Paso libre entre mobiliario (m)
- Vacío sobre planta baja

SUPERFICIES Y ALTURAS


Forjado de planta alta	32,02 m²
Altílo diáfano	26,17 m²
Aseo (lavabo + inodoro)	3,92 m²
Almacén	2,59 m²
Nivel del forjado, medido	+2,56 m
Puestos de cowork	14

PILARES Y MACHONES (secciones en m)

P1 Machón del muro Oeste	0,30 × 0,60
P2 Pilastra del muro Sur	0,58 × 0,45
P3 Pilar central	0,65 × 1,07
P4 Machón de la medianera Este	0,20 × 0,60
P5 Pilar de fachada	0,60 × 1,00



NOTAS

Cotas en metros, tomadas sobre el levantamiento.
Nivel del forjado +2,56, medido en obra.
El forjado del altílo no cubre todo el local: la franja sur y oeste es un vacío a doble altura.
Mesa de cowork 2,40 × 1,00 para 8 puestos y una redonda de Ø 1,20 con 6 sillas. Medidas promedio.
Pasos libres entre mobiliario acotados en azul:
1,01 hacia el aseo y el almacén; 1,30 en el desembarco; 0,26 a 0,85 en los accesos a las sillas.

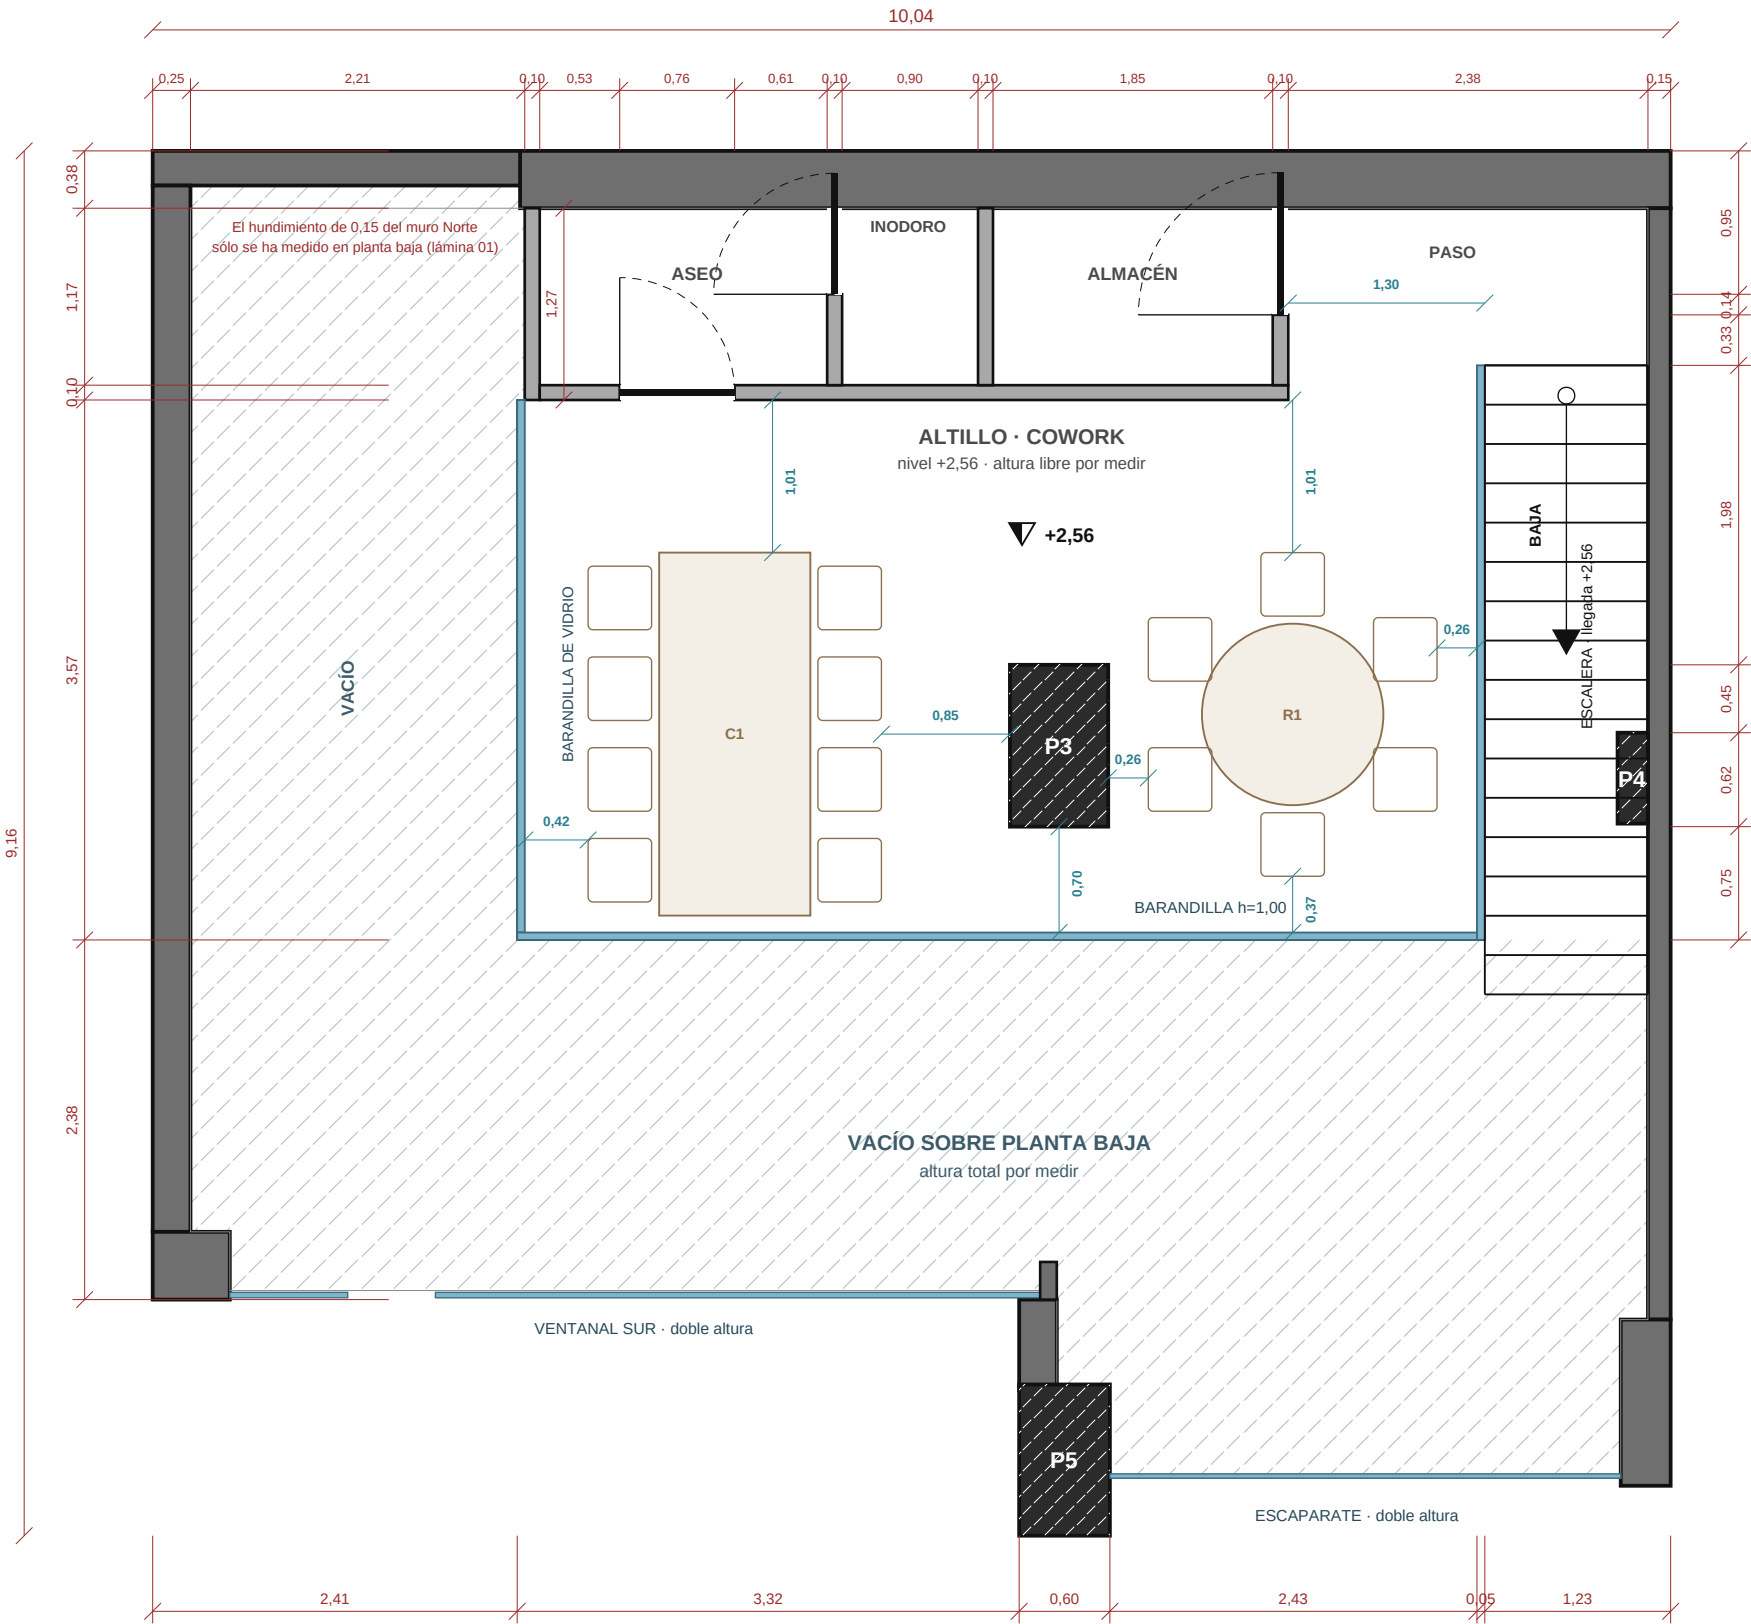

COMPROBAR EN OBRA Puntos en los que los vídeos del local no cuadran con el levantamiento, o que el levantamiento no recoge. Se dibuja el levantamiento por ser la única fuente acotada.

- Muro Norte: macizo hasta el borde del solar, 0,229 en la cocina y 0,379 en el resto; el levantamiento suponía 0,148. Medir el espesor real y el hundimiento de 0,15.
- Canto del forjado del altílo. Con 2,56 m de suelo a suelo, la altura libre de planta baja es 2,56 menos ese canto, no los 2,70 supuestos.
- P1b se dibuja como viga (1,83 × 0,25) y no como pilar: si fuera macizo hasta el suelo, la cocina no tendría entrada. Medir su intradós.
- Zócalo del ventanal: 0,347 desde el vidrio, deducido de los 2,72 de P3 a su cara interior; sobresale 0,16 del muro del ventanal (0,25). Medirlo directamente.
- Muro Oeste de la cocina: caben 2,97 entre P1 y la bancada y los cuatro aparatos suman 3,04. Faltan 7 cm: quitar un armario frigorífico o estrechar el fregadero.
- La pared en L queda 0,10 al Este del borde del forjado del levantamiento: el vidrio de 1,35 sobre ella (2,57 en total) no pasa bajo el altílo. Medir ese borde.
- Vestíbulo: los 1,31 y 2,23 del cliente suman 3,54 y de P5 al muro Este hay 3,559. Se dibuja el 1,31 medido y el resto queda en 2,25, 2 cm más que su medida.
- P3 no se mueve: los 3,23 a la medianera dan 3,25 medidos al muro desnudo (2,98 al trasdosado) y los 3,65 a P5 se dibujan 3,69. Confirmar a qué cara se midió.
- Aire acondicionado: dos cassettes situados con las fotos del cliente, con panel estándar de 0,95 y rejilla de 0,90 × 0,50. Medir posición y tamaño reales.

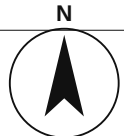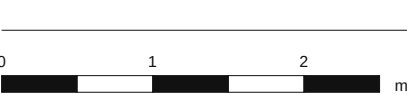

ESCALA

1:50 (A3)

FECHA

19 set. 2026

PLANO

02 / 04