

PROYECTO
Reforma integral de local de hostelería

EMPLAZAMIENTO
Local en planta baja y altílo
Málaga

PLANO
EQUIPAMIENTO

Barra y cocina · productos Makro

LEYENDA




- Bancada o mueble bajo
- Equipo refrigerado
- Encimera o tabla corrida
- Aparato (trazos: bajo encimera)
- Tabla de madera
- Muro de carga / medianera

HOLGURAS Y ALTURAS

Pasillo de cocina, mínimo	0,97 m
Paso de servicio en barra	1,05 m
Entrada a la cocina, bajo la viga	1,37 m
Hueco libre de mesada en barra	0,75 m
Altura de encimera	0,90 m
Borde inferior de la campana	2,00 m

NOTAS

Cada máquina es un producto real de makro.es con sus medidas de ficha; la web bloquea el acceso directo, así que las medidas vienen de su buscador. Confirmar en la ficha antes de comprar. Cocción y campana metidas en el hundimiento de 0,275 de la medianera Norte, como pidió el cliente. Mesada refrigerada de una sola pieza (2,54, la más larga de Makro) pegada al doblez de la L; 0,33 libres junto a la cocción. K6 bajo el escurridor de K7. Pasillo de cocina de 0,97 a 1,11. Muro Oeste: 3,04 de aparatos en los 3,33 que hay hasta P1. Trasbarra nueva del 19 set.: mesada corrida de 0,60 entre P1 y P2, con estante encima; la nevera A5 va bajo el hueco libre y nada bajo el fregadero A4. Alturas por confirmar: A4 y A5 miden 0,85 y la encimera va a 0,90, con 5 cm de desnivel en A4 y 1-2 de holgura sobre A5. La altura libre que pide A3 para llenar la cuba no consta: medirla antes de colgar A6.

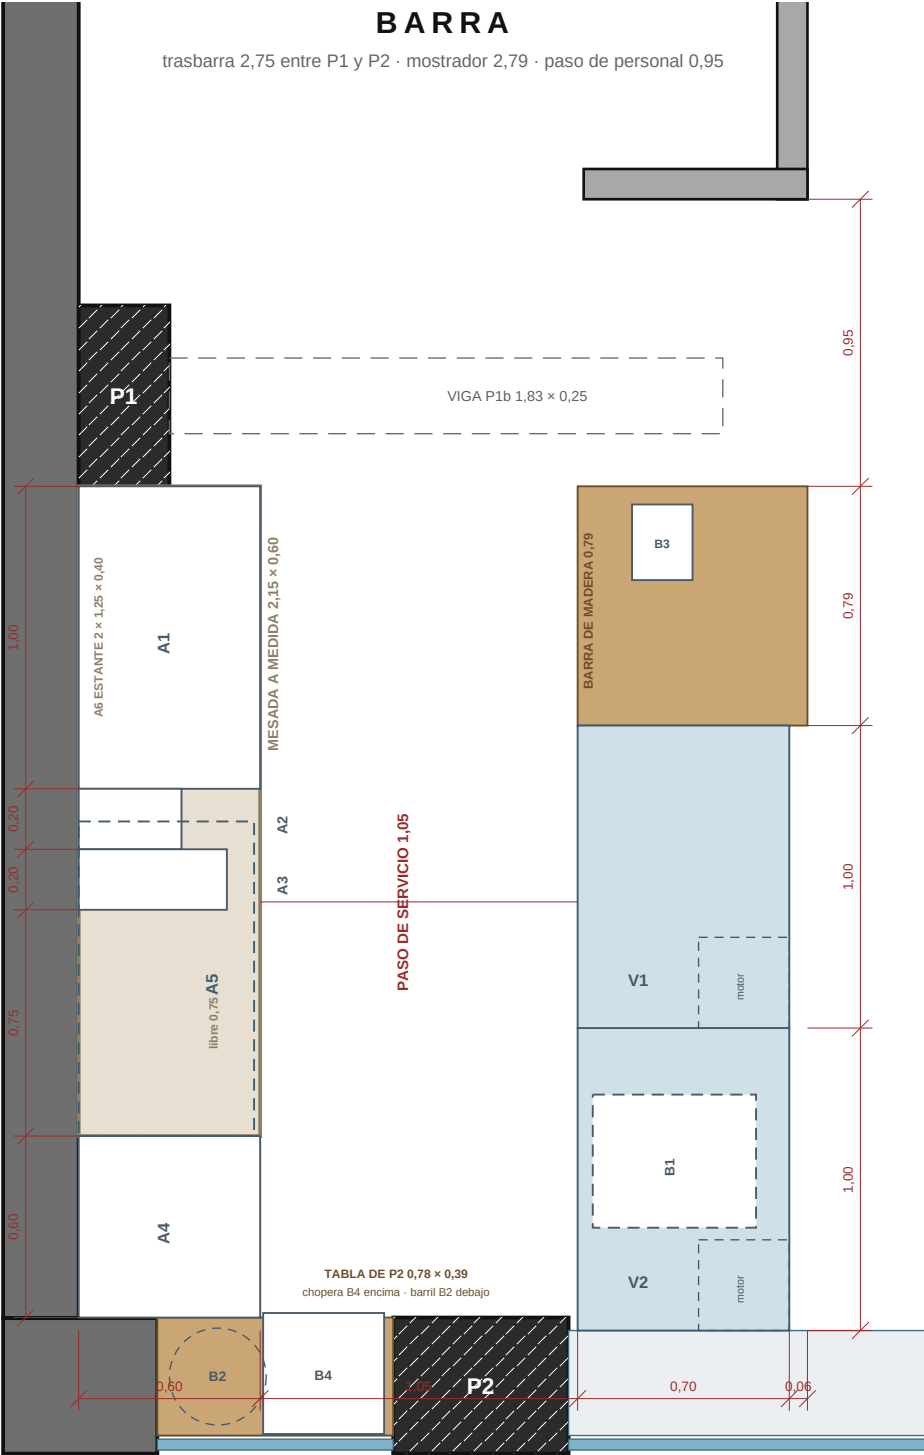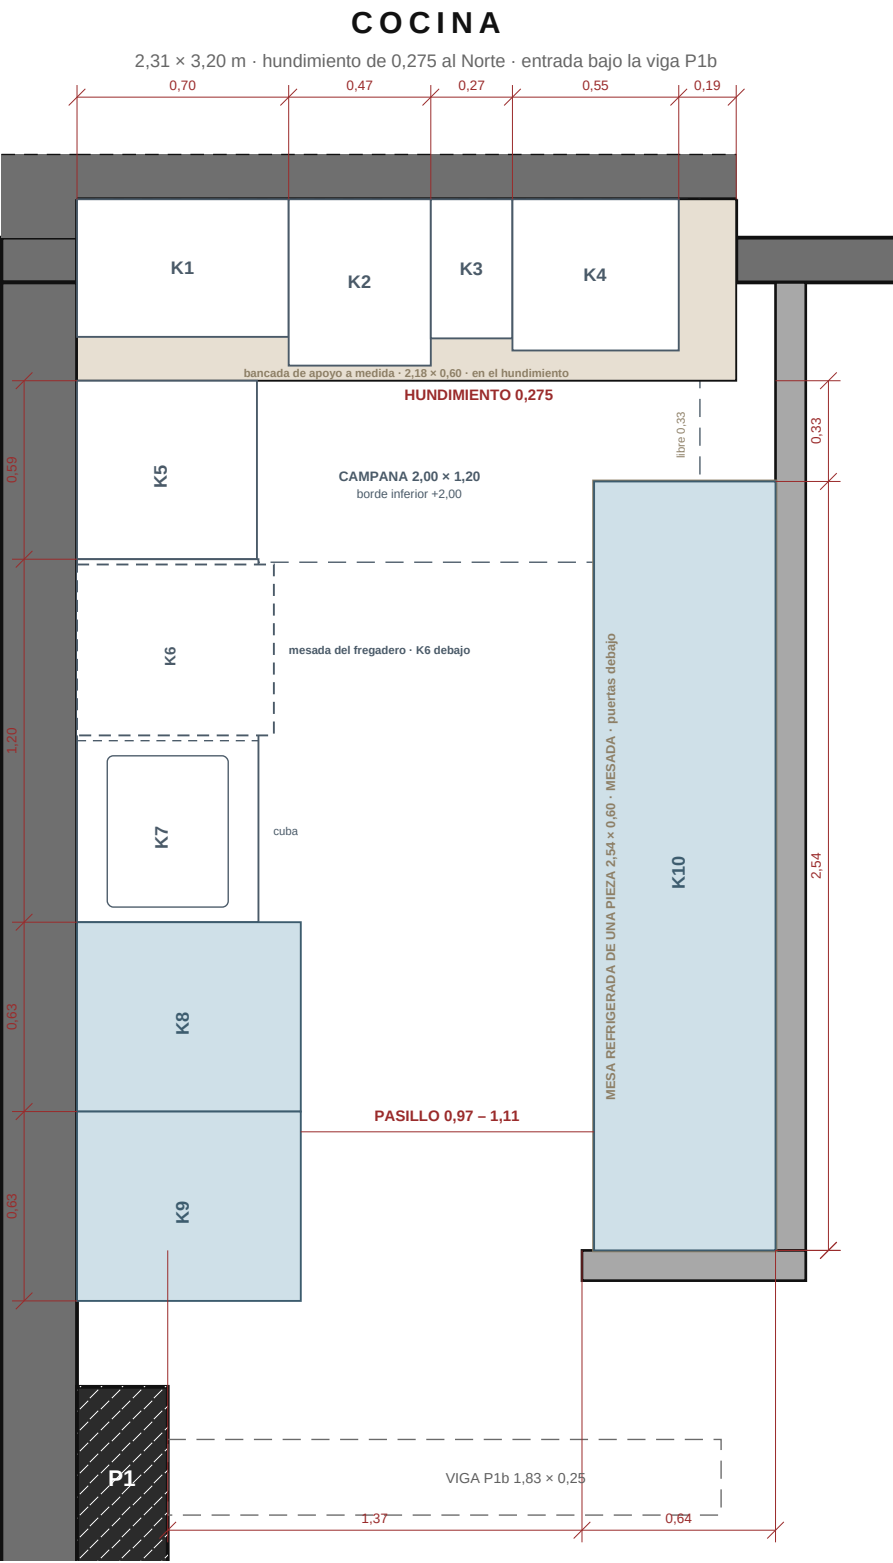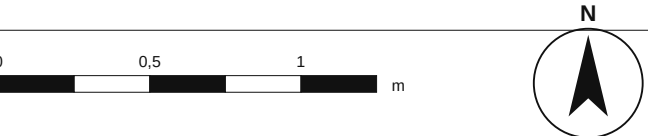

EQUIPAMIENTO · MAKRO

Ancho x fondo x alto en metros, de la ficha de makro.es. Vitrinas y cafetera ya compradas. Tablet y barriles con medida promedio. Enlaces en la lámina 04.

K1	Placa de inducción Bartscher, 2 zonas Ø230, 6 kW, 400 V	0,70 × 0,46 × 0,12	A2	Molinillo de café Cunil TRANQUILO de ABC, 275 W, tolva 0,5 kg	0,17 × 0,34 × 0,41
K2	Cocedor de pasta eléctrico METRO Professional GNC1008, 8 L, 4 cestos	0,47 × 0,55 × 0,38	A3	Máquina de helado y crema fría Bras B-CREAM1HD, 6 L, italiana	0,20 × 0,49 × 0,62
K3	Freidora profesional 1 cuba de 7 L, eléctrica	0,27 × 0,46 × 0,37	A4	Fregadero de pie 1 seno con estante y bastidor, 600 × 600 × 850	0,60 × 0,60 × 0,85
K4	Plancha eléctrica Cleiton 50 cm, placa de 8 mm, sobremesa	0,55 × 0,50 × 0,33	A5	Botellero frigorífico BTL1000, 2 puertas correderas, 240 L	1,04 × 0,58 × 0,85
KC	Campana extractora industrial recta, sin turbina, AISI-304 satinado, 2 × 1,2 m	2,00 × 1,20 × 0,50	A6	Estante mural cartelas compacto Fricosmos 011410, 1250 × 400 × 245	1,25 × 0,40 × 0,24
K5	Horno de convección eléctrico industrial, 4 bandejas 45 × 33	0,59 × 0,59 × 0,57	V2	Vitrina refrigerada (comprada), 1,00 × 0,70; debajo, lavavasos	1,00 × 0,70 × 1,25
K7	Fregadero con bastidor con hueco lavavajillas, cuba izquierda, 1200 × 600	1,20 × 0,60 × 0,85	V1	Vitrina refrigerada (comprada), 1,00 × 0,70; hueco libre debajo	1,00 × 0,70 × 1,25
K6	Lavavajillas industrial ST500, cesta 50 × 50, bajo el escurridor de K7	0,56 × 0,65 × 0,86	B1	Lavavasos Elettrobar FAST 40, cesta 40 × 40 (bajo la vitrina V2)	0,44 × 0,54 × 0,67
K8	Armario refrigerado vertical Edenox APS-451 I, inox, 1 puerta, 395 L	0,63 × 0,74 × 1,86	B2	Barriles de cerveza de 30 L, Ø 0,32 (debajo de la tabla de P2)	0,32 × 0,32 × 0,60
K9	Armario refrigerado vertical Edenox APS-451 I, inox, 1 puerta, 395 L	0,63 × 0,74 × 1,86	B3	Caja: tablet sobre soporte (lo único que queda en el mostrador)	0,25 × 0,20 × 0,25
K10	Mesa refrigerada Infrico 4 puertas, AISI-304, peto 100 mm, -2/+8 °C, 530 L	2,54 × 0,60 × 0,85	B4	Columna de cerveza en T de 3 grifos, bandeja 40 × 40, sobre la tabla de P2	0,40 × 0,40 × 0,55
A1	Cafetera (comprada), 2 grupos	1,00 × 0,60 × 0,50			