

PROYECTO

Reforma integral de local de hostelería

EMPLAZAMIENTO

Local en planta baja y altílo Málaga

PLANO

PLANTA BAJA

Estado actual · estructura

LEYENDA

- Muro de carga / medianera
- Pilar o machón de hormigón
- Pared en L nueva (apoyo del vidrio)
- Carpintería acristalada
- Espacio de doble altura
- Forjado sobre el corte
- Reserva de espacio del cliente
- Mesas dobles de 0,70 × 0,70 y sillas
- Itinerario accesible ≥ 1,20 · giro Ø 1,50
- Punto de luz s/ proyecto original
- Aire acondicionado (cassette de techo)

SUPERFICIES Y ALTURAS



|                                |              |
|--------------------------------|--------------|
| Planta baja, dentro de muros   | 76,23 m²     |
| Zona de doble altura           | 38,40 m²     |
| Suelo a suelo, medido en obra  | 2,56 m       |
| Altura libre bajo forjado      | 2,56 – canto |
| Pared en L, altura             | 1,22 m       |
| Mesas dobles / plazas sentadas | 12 / 24      |
| Acristalamiento de fachada     | ≈ 4,70 m     |

PILARES Y MACHONES (secciones en m)

|                                |             |
|--------------------------------|-------------|
| P1 Machón del muro Oeste       | 0,30 × 0,60 |
| P2 Pilastra del muro Sur       | 0,58 × 0,45 |
| P3 Pilar central               | 0,65 × 1,07 |
| P4 Machón de la medianera Este | 0,20 × 0,60 |
| P5 Pilar de fachada            | 0,60 × 1,00 |

NOTAS

Cotas en metros. Hundimiento, pared en L, P3, barra, zócalo y puerta con las medidas del 19 set.; el resto, del levantamiento. Sección a 1,20 m sobre el pavimento. Mesas dobles de 0,70 × 0,70 que el personal junta para formar mesas de cuatro. M4 pegada a P3. El sillón se dibuja con 0,60 de fondo contra la medianera: falta medirlo y el trasdosado de 0,10. Luces: las del proyecto original; los dos cassettes de aire, situados con las fotos del cliente. Itinerario accesible de 1,20 de la puerta a la barra, al baño y a la plaza PMR de M2, con giro de Ø 1,50 en la entrada. El baño no es accesible: puerta de 0,70.

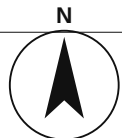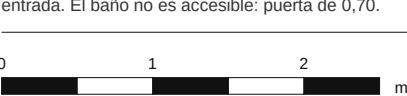

ESCALA


1:50 (A3)

FECHA

19 set. 2026

PLANO

01 / 04

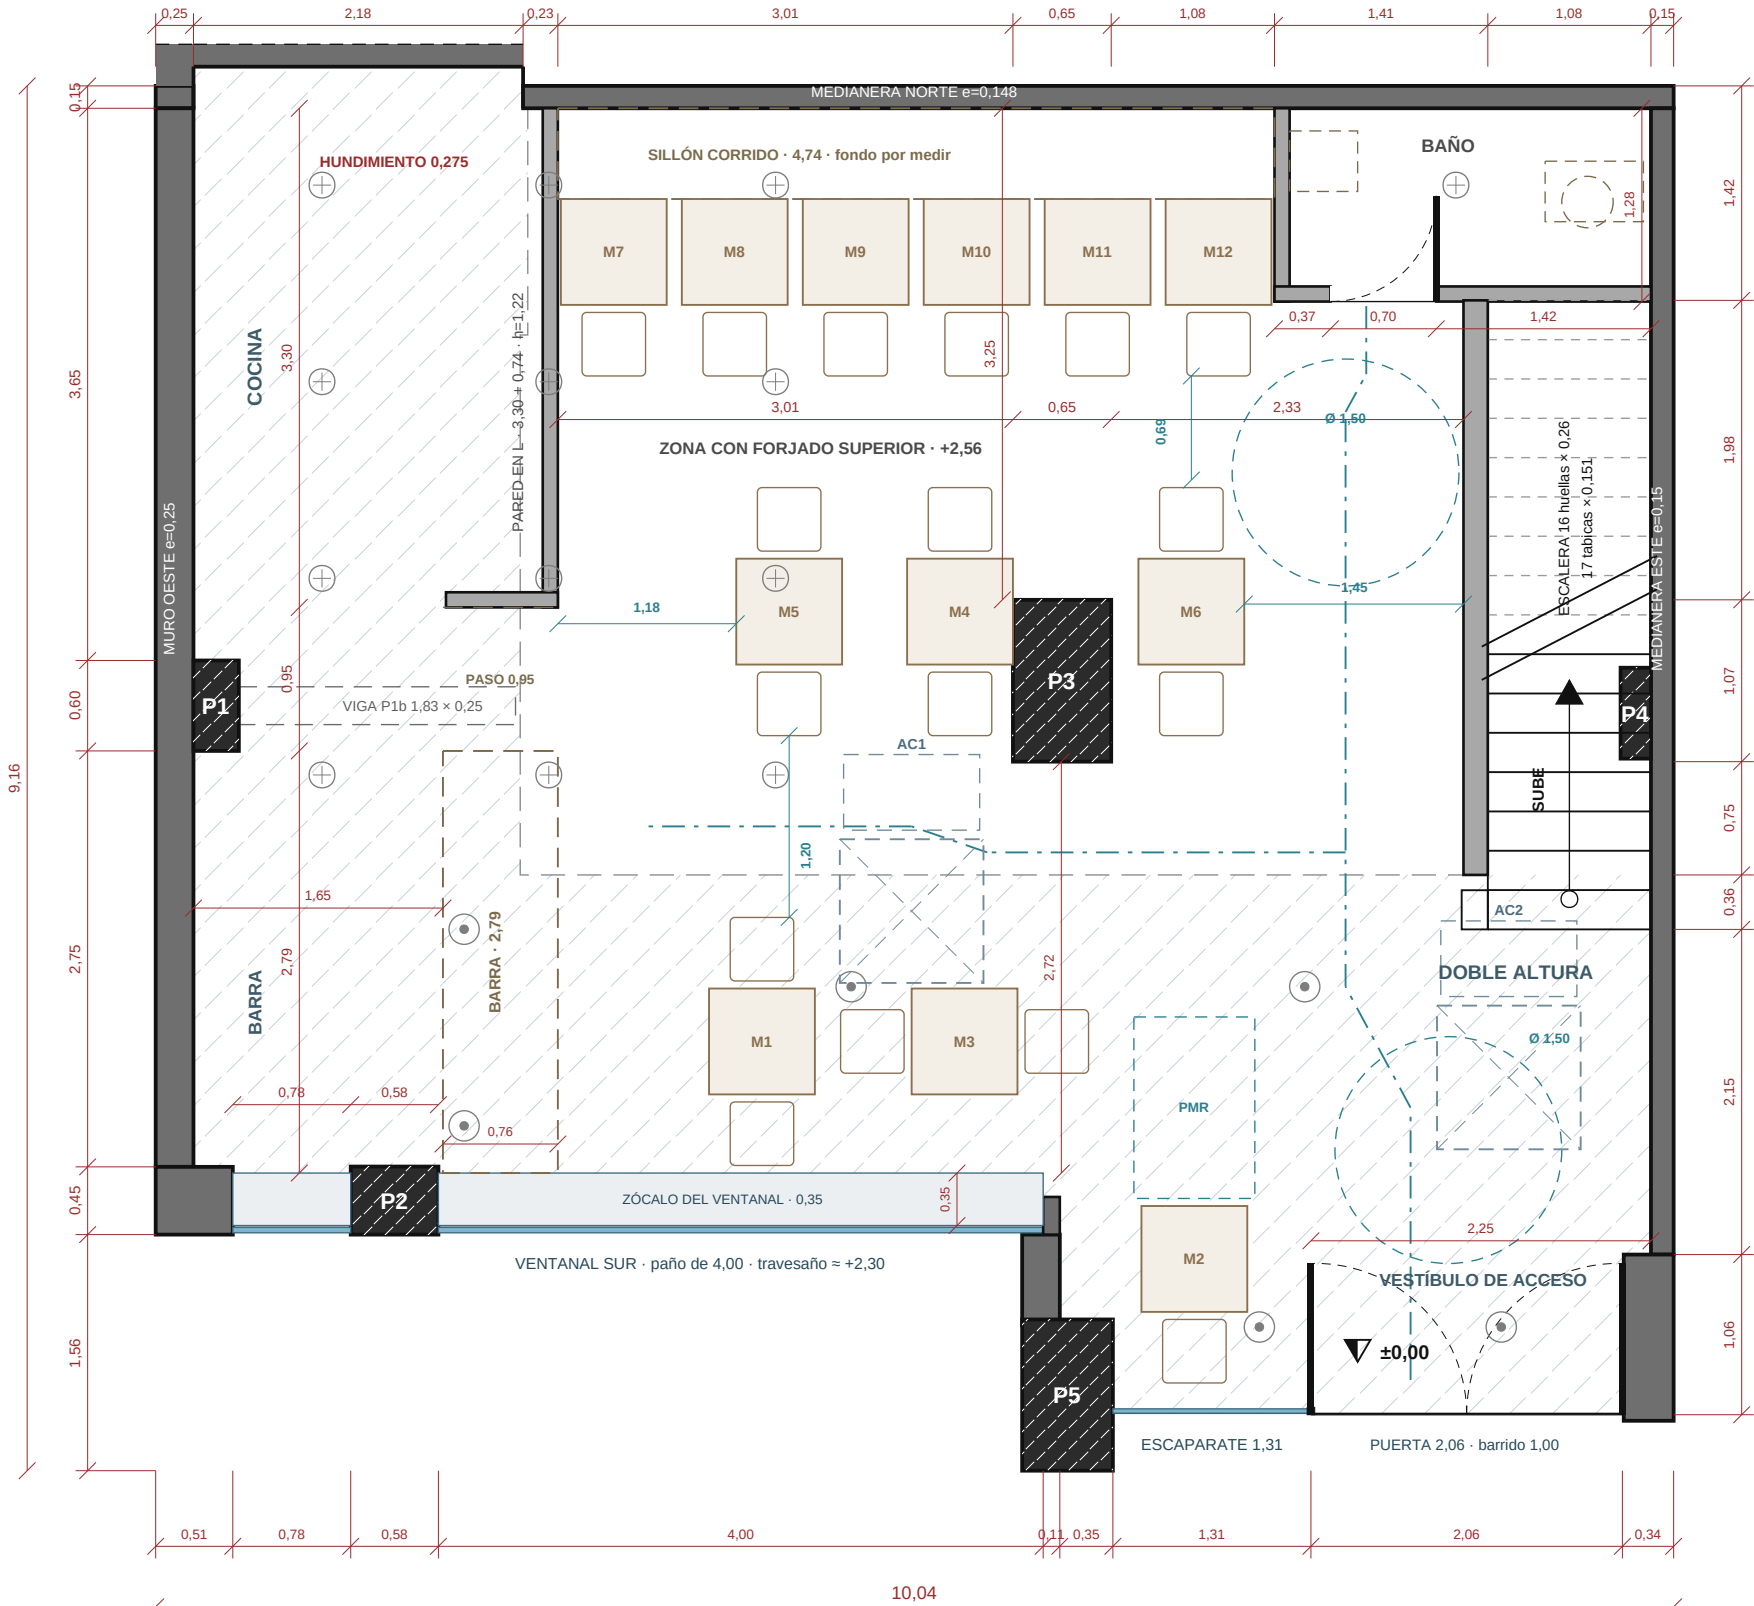

COMPROBAR EN OBRA Puntos en los que los vídeos del local no cuadran con el levantamiento, o que el levantamiento no recoge. Se dibuja el levantamiento por ser la única fuente acotada.

- Hundimiento de la medianera Norte: 0,275 de fondo en los 2,18 de la cocina. Supera el espesor dibujado (0,148): medir ese cerramiento y lo que hay detrás.
- Canto del forjado del altílo. Con 2,56 m de suelo a suelo, la altura libre de planta baja es 2,56 menos ese canto, no los 2,70 supuestos.
- P1b se dibuja como viga (1,83 × 0,25) y no como pilar: si fuera macizo hasta el suelo, la cocina no tendría entrada. Medir su intradós.
- Zócalo del ventanal: 0,347 desde el vidrio, deducido de los 2,72 de P3 a su cara interior; sobresale 0,16 del muro del ventanal (0,25). Medirlo directamente.
- Cadena Este-Oeste del cliente (2,18 + 3,01 + 0,65 + 2,33): cierra contra la escalera con 0,13 de pared entre el hundimiento y la L y 0,16 de cerramiento.
- La pared en L queda 0,10 al Este del borde del forjado del levantamiento: el vidrio de 1,35 sobre ella (2,57 en total) no pasa bajo el altílo. Medir ese borde.
- Vestíbulo: los 1,31 y 2,23 del cliente suman 3,54 y de P5 al muro Este hay 3,559. Se dibuja el 1,31 medido y el resto queda en 2,25, 2 cm más que su medida.
- P3 no se mueve: sus 3,23 a la medianera Norte y 3,65 a la cara Norte de P5 lo llevarían 2 cm al Sur y 4 cm al Norte. Se dibujan 3,25 y 3,69. Medir de nuevo.
- Aire acondicionado: dos cassettes situados con las fotos del cliente, con panel estándar de 0,95 y rejilla de 0,90 × 0,50. Medir posición y tamaño reales.