

GRUPO SUMA

Reformas y proyectos · Málaga

PROYECTO
Reforma integral de local de hostelería

EMPLAZAMIENTO
Local en planta baja y altillo
Málaga

PLANO
EQUIPAMIENTO

Barra y cocina · distribución

LEYENDA



- Mueble bajo encimera
- Equipo refrigerado
- Encimera corrida
- Aparato sobre encimera
- Muro de carga / medianera
- Pilar o machón

HOLGURAS Y ALTURAS

Pasillo de trabajo en cocina	0,92 m
Paso de servicio en barra	1,02 m
Fondo de todos los muebles	0,60 m
Altura de encimera	0,90 m
Borde inferior de la campana	2,00 m

NOTAS

Anchos de serie de hostelería, no medidos sobre aparato. Sustituir por los del equipo que se elija.
La línea de cocción va en serie 600 y no en 700: con 2,12 m libres, un fondo de 700 dejaría el pasillo en 0,82 m, bajo el mínimo recomendado.
La trasbarra es un solo mueble con una sola encimera corrida; el módulo técnico T1 queda bajo la cafetera.
No hace falta cerrar la zona del ventanal: todo entra en los 2,75 m de trasbarra.

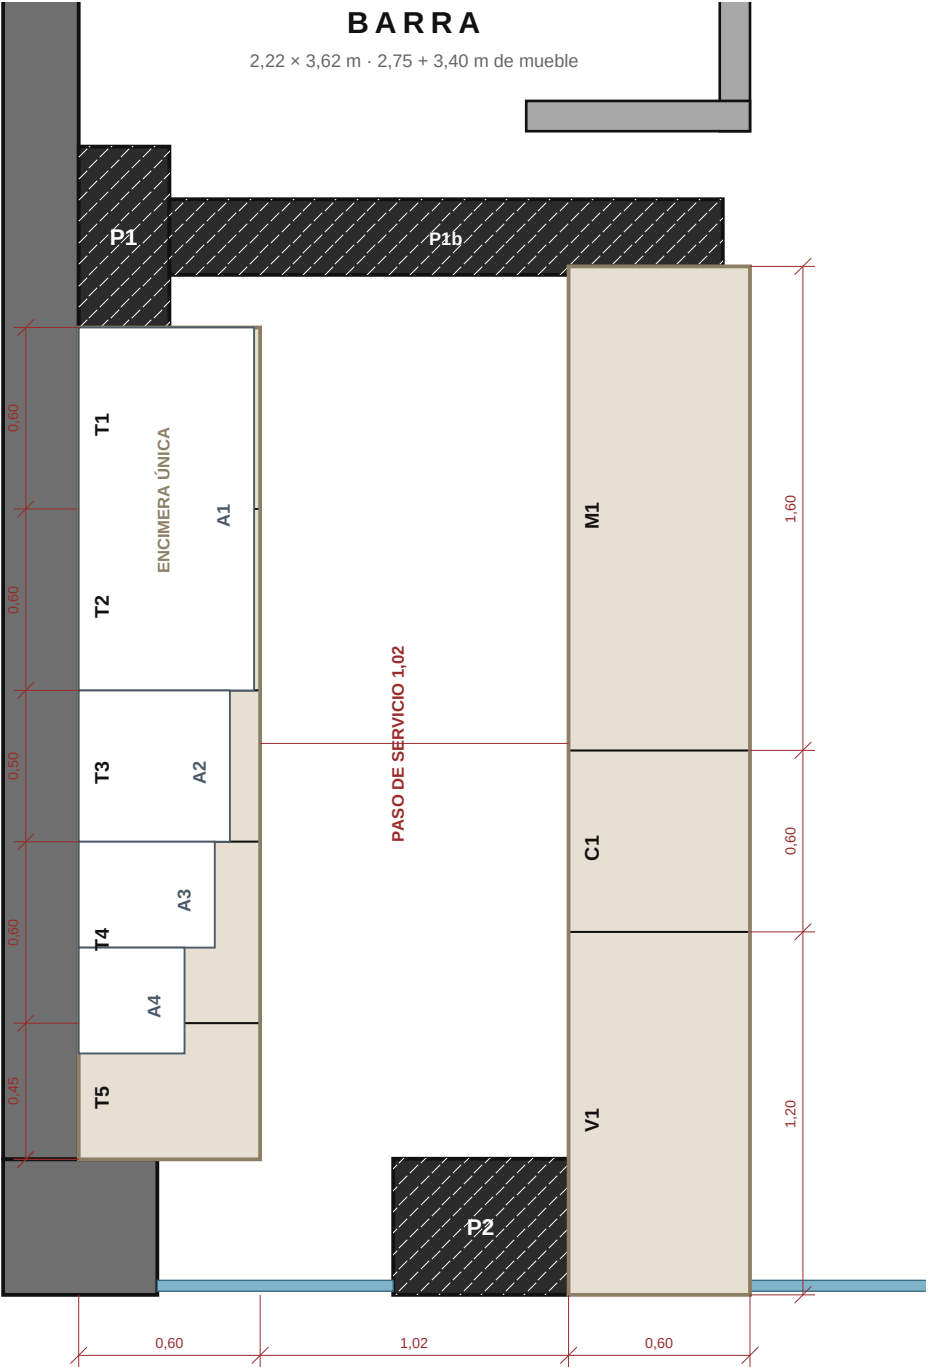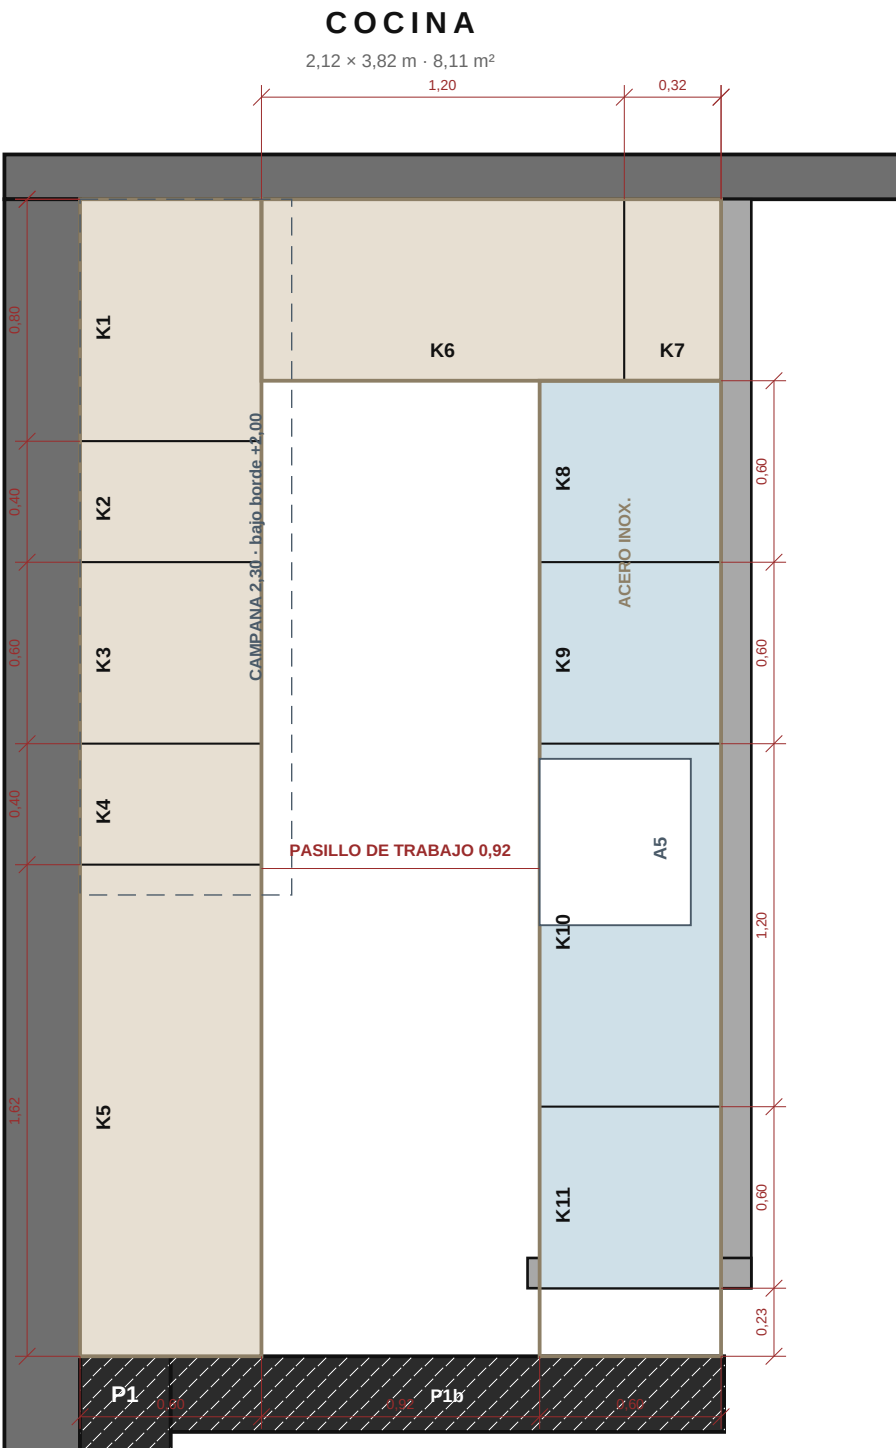

EQUIPAMIENTO

Ancho en metros. Serie de hostelería, pendiente de sustituir por el del equipo que se elija.

K1	Cocina de 4 fuegos	0,80	K9	Horno bajo encimera	0,60	V1	Vitrina expositora refrigerada	1,20
K2	Cocedor de pasta	0,40	K10	Mesa refrigerada de 2 puertas	1,20	C1	Caja y TPV	0,60
K3	Plancha	0,60	K11	Módulo de apoyo con estante	0,60	M1	Mostrador de servicio	1,60
K4	Freidora	0,40	T1	Módulo técnico: descalcificador, conexiones y cajón	0,60	A1	Cafetera de 2 grupos	1,20
K5	Mesa de trabajo	1,62	T2	Lavavajillas de barra, cesta 400 x 400	0,60	A2	Fregadero pequeño	0,50
K6	Fregadero de cocina, 2 cubetas con escurridor	1,20	T3	Mueble del fregadero	0,50	A3	Exprimidor de naranjas	0,35
K7	Módulo de apoyo	0,32	T4	Frigorífico bajo mostrador	0,60	A4	Tirador de cerveza	0,35
K8	Lavavajillas de cocina	0,60	T5	Cajonera	0,45	A5	Cortadora de fiambre	0,55

ESCALA

1:25 (A3)

FECHA

14 set. 2026

PLANO

03 / 03