

PROYECTO

Reforma integral de local de hostelería

EMPLAZAMIENTO

Local en planta baja y altílo
Málaga

PLANO

PLANTA BAJA

Estado actual · estructura

LEYENDA

- Muro de carga / medianera
- Pilar o machón de hormigón
- Pared en L nueva (apoyo del vidrio)
- Carpintería acristalada
- Espacio de doble altura
- Forjado sobre el corte
- Reserva de espacio del cliente
- Punto de luz s/ proyecto

SUPERFICIES Y ALTURAS

Planta baja, dentro de muros	75,63 m²
Zona de doble altura	37,80 m²
Suelo a suelo, medido en obra	2,56 m
Altura libre bajo forjado	2,56 – canto
Panel de vidrio de la pared en L	1,35 m
Acristalamiento de fachada	≈ 4,70 m

PILARES Y MACHONES (secciones en m)

P1 Machón del muro Oeste	0,30 × 0,60
P1b Machón sobre P1, al forjado	1,83 × 0,25
P2 Pilastra del muro Sur	0,58 × 0,45
P3 Pilar central	0,65 × 1,07
P4 Machón de la medianera Este	0,20 × 0,60
P5 Pilar de fachada	0,60 × 1,00



NOTAS

Cotas en metros. Las de los pilares, la pared en L, el ventanal y la puerta están medidas en obra (revisión del 14 set. 2026); el resto procede del levantamiento previo.

Cota de referencia ±0,00 en el pavimento de planta baja. Sección horizontal a 1,20 m.

Las reservas de espacio en trazos no son estructura: sólo marcan dónde van la barra, el paso de personal y el sillón corrido.

Los puntos de luz proceden del proyecto de reforma, no están replanteados en obra.

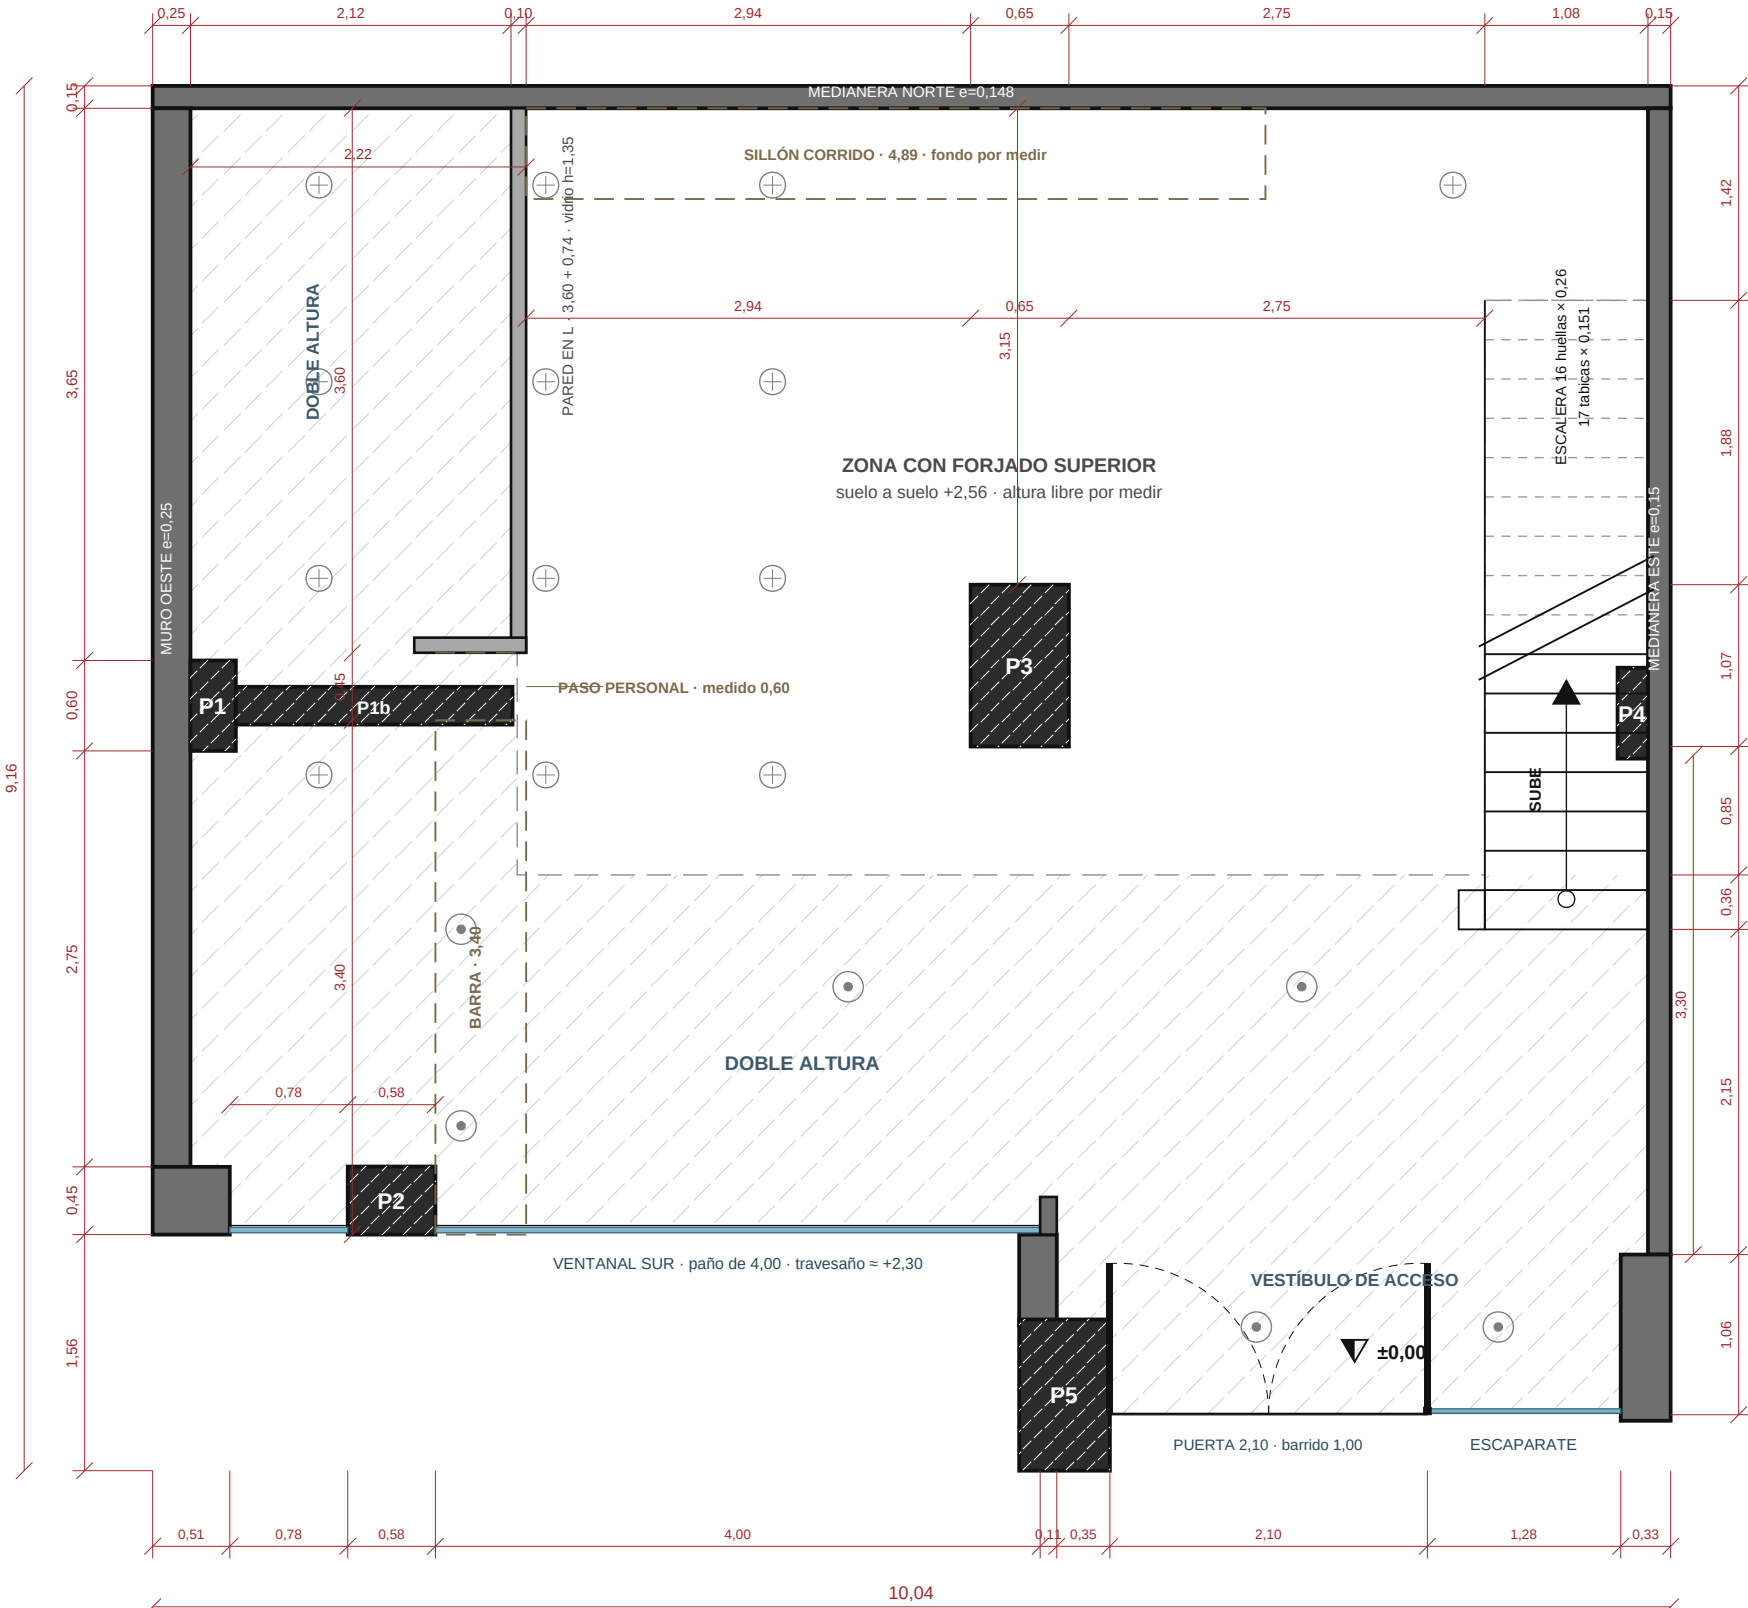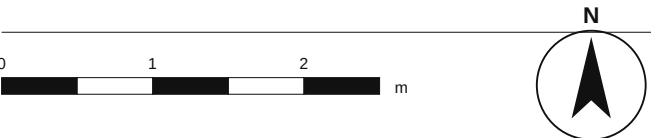

COMPROBAR EN OBRA Puntos en los que los vídeos del local no cuadran con el levantamiento, o que el levantamiento no recoge. Se dibuja el levantamiento por ser la única fuente acotada.

- La cota de 2,70 anotada contra la medianera norte no cuadra: mide la misma distancia que el 2,22 aplicado (muro Oeste a pared en L). Aclarar qué mide ese 2,70.
- Canto del forjado del altílo. Con 2,56 m de suelo a suelo, la altura libre de planta baja es 2,56 menos ese canto, no los 2,70 supuestos.
- Espesor de la pared en L y del panel de vidrio de 1,35 m que sostiene.
- Posición de P3: el 3,15 de la planta baja y el 1,90 de la planta alta se llevan 0,15; el 2,94 y el 3,20 se llevan 0,26. Se dibuja con la cadena de planta baja.
- Del P3 a la escalera se midió 2,35 y en el plano salen 2,75. Los 0,40 de diferencia no cierran contra la medianera Este.
- P5: se dibuja 0,60 x 1,00 con la cara Oeste a plomo con el muro del cuello. El resalto de 0,20 al Este anotado da 0,35 en esa posición.
- Escaparate: bajo él aparece un 2,70 sin aclarar. Se dibuja el hueco completo con la puerta de 2,10 pegada a P5.
- Tabica de la escalera: 2,56/17 = 0,151 m. Contar los peldaños en obra para confirmar que son 17.
- Machones trasdosados con placa de yeso nueva: la sección de hormigón no es verificable a la vista.