

PROYECTO

Reforma integral de local de hostelería

EMPLAZAMIENTO

Local en planta baja y altílo Málaga

PLANO

PLANTA BAJA

Estado actual · estructura

LEYENDA

- Muro de carga / medianera
- Pilar o machón de hormigón
- Pared en L nueva (apoyo del vidrio)
- Carpintería acristalada
- Espacio de doble altura
- Forjado sobre el corte
- Reserva de espacio del cliente
- Punto de luz s/ proyecto

SUPERFICIES Y ALTURAS

Planta baja, dentro de muros	75,63 m²
Zona de doble altura	37,80 m²
Suelo a suelo, medido en obra	2,56 m
Altura libre bajo forjado	2,56 – canto
Panel de vidrio de la pared en L	1,35 m
Acristalamiento de fachada	≈ 4,70 m

PILARES Y MACHONES (secciones en m)

P1 Machón del muro Oeste	0,30 × 0,60
P1b Machón sobre P1, al forjado	1,83 × 0,25
P2 Pilastra del muro Sur	0,58 × 0,45
P3 Pilar central	0,65 × 1,07
P4 Machón de la medianera Este	0,20 × 0,60
P5 Pilar de fachada	0,60 × 1,00



NOTAS

Cotas en metros. Las de los pilares, la pared en L, el ventanal y la puerta están medidas en obra (revisión del 14 set. 2026); el resto procede del levantamiento previo.

Cota de referencia ±0,00 en el pavimento de planta baja. Sección horizontal a 1,20 m.

Las reservas de espacio en trazos no son estructura: sólo marcan dónde van la barra, el paso de personal y el sillón corrido.

Los puntos de luz proceden del proyecto de reforma, no están replanteados en obra.

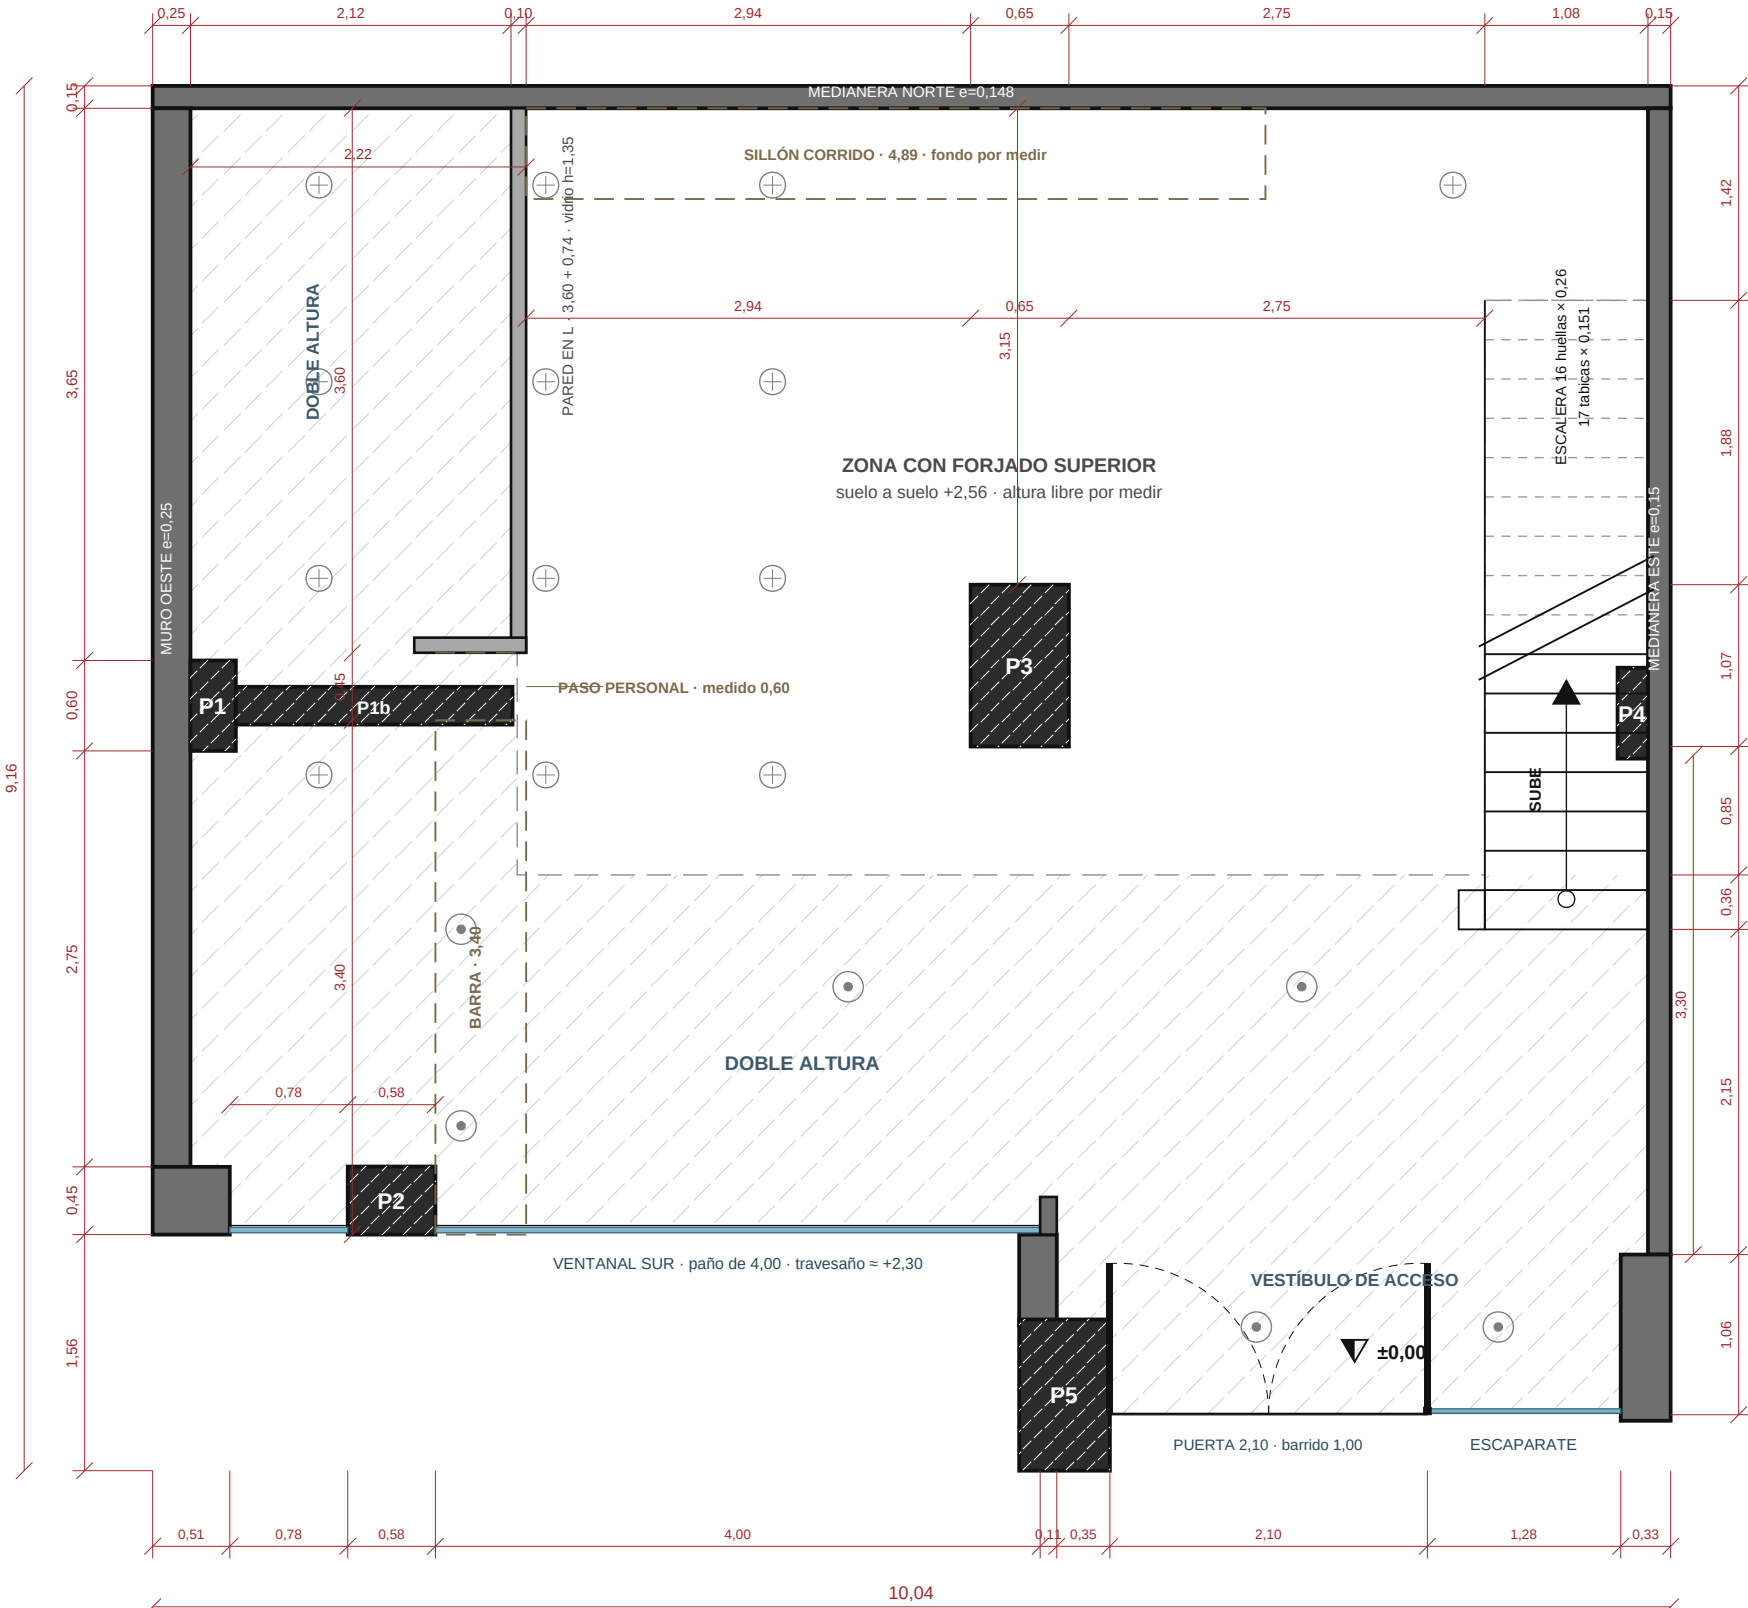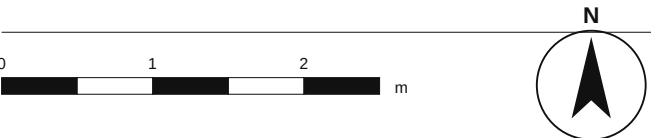

COMPROBAR EN OBRA Puntos en los que los vídeos del local no cuadran con el levantamiento, o que el levantamiento no recoge. Se dibuja el levantamiento por ser la única fuente acotada.

- La cota de 2,70 anotada contra la medianera norte no cuadra: mide la misma distancia que el 2,22 aplicado (muro Oeste a pared en L). Aclarar qué mide ese 2,70.
- Canto del forjado del altílo. Con 2,56 m de suelo a suelo, la altura libre de planta baja es 2,56 menos ese canto, no los 2,70 supuestos.
- Espesor de la pared en L y del panel de vidrio de 1,35 m que sostiene.
- Posición de P3: el 3,15 de la planta baja y el 1,90 de la planta alta se llevan 0,15; el 2,94 y el 3,20 se llevan 0,26. Se dibuja con la cadena de planta baja.
- Del P3 a la escalera se midió 2,35 y en el plano salen 2,75. Los 0,40 de diferencia no cierran contra la medianera Este.
- P5: se dibuja 0,60 x 1,00 con la cara Oeste a plomo con el muro del cuello. El resalto de 0,20 al Este anotado da 0,35 en esa posición.
- Escaparate: bajo él aparece un 2,70 sin aclarar. Se dibuja el hueco completo con la puerta de 2,10 pegada a P5.
- Tabica de la escalera: 2,56/17 = 0,151 m. Contar los peldaños en obra para confirmar que son 17.
- Machones trasdosados con placa de yeso nueva: la sección de hormigón no es verificable a la vista.

GRUPO SUMA

Reformas y proyectos · Málaga

PROYECTO

Reforma integral de local de hostelería

EMPLAZAMIENTO

Local en planta baja y altillo
Málaga

PLANO

PLANTA ALTA

Altillo +2,56 · estructura

LEYENDA

- Muro de carga / medianera
- Pilar o machón de hormigón
- Tabiquería
- Barandilla de vidrio
- Vacio sobre planta baja

SUPERFICIES Y ALTURAS


Forjado de planta alta	33,74 m²
Altillo diáfano	26,17 m²
Aseo (lavabo + inodoro)	3,92 m²
Almacén	2,59 m²
Nivel del forjado, medido	+2,56 m
Altura libre de planta alta	2,50 m (por medir)

PILARES Y MACHONES (secciones en m)

P1 Machón del muro Oeste	0,30 × 0,60
P1b Machón sobre P1, al forjado	1,83 × 0,25
P2 Pilastra del muro Sur	0,58 × 0,45
P3 Pilar central	0,65 × 1,07
P4 Machón de la medianera Este	0,20 × 0,60
P5 Pilar de fachada	0,60 × 1,00

NOTAS

Cotas en metros, tomadas sobre el levantamiento.
Plano de estructura: no se representa mobiliario ni equipamiento.
El forjado del altillo no cubre todo el local: la franja sur y oeste es un vacío a doble altura.
Nivel del forjado +2,56, medido en obra.
Sección horizontal a 1,20 m sobre el forjado.

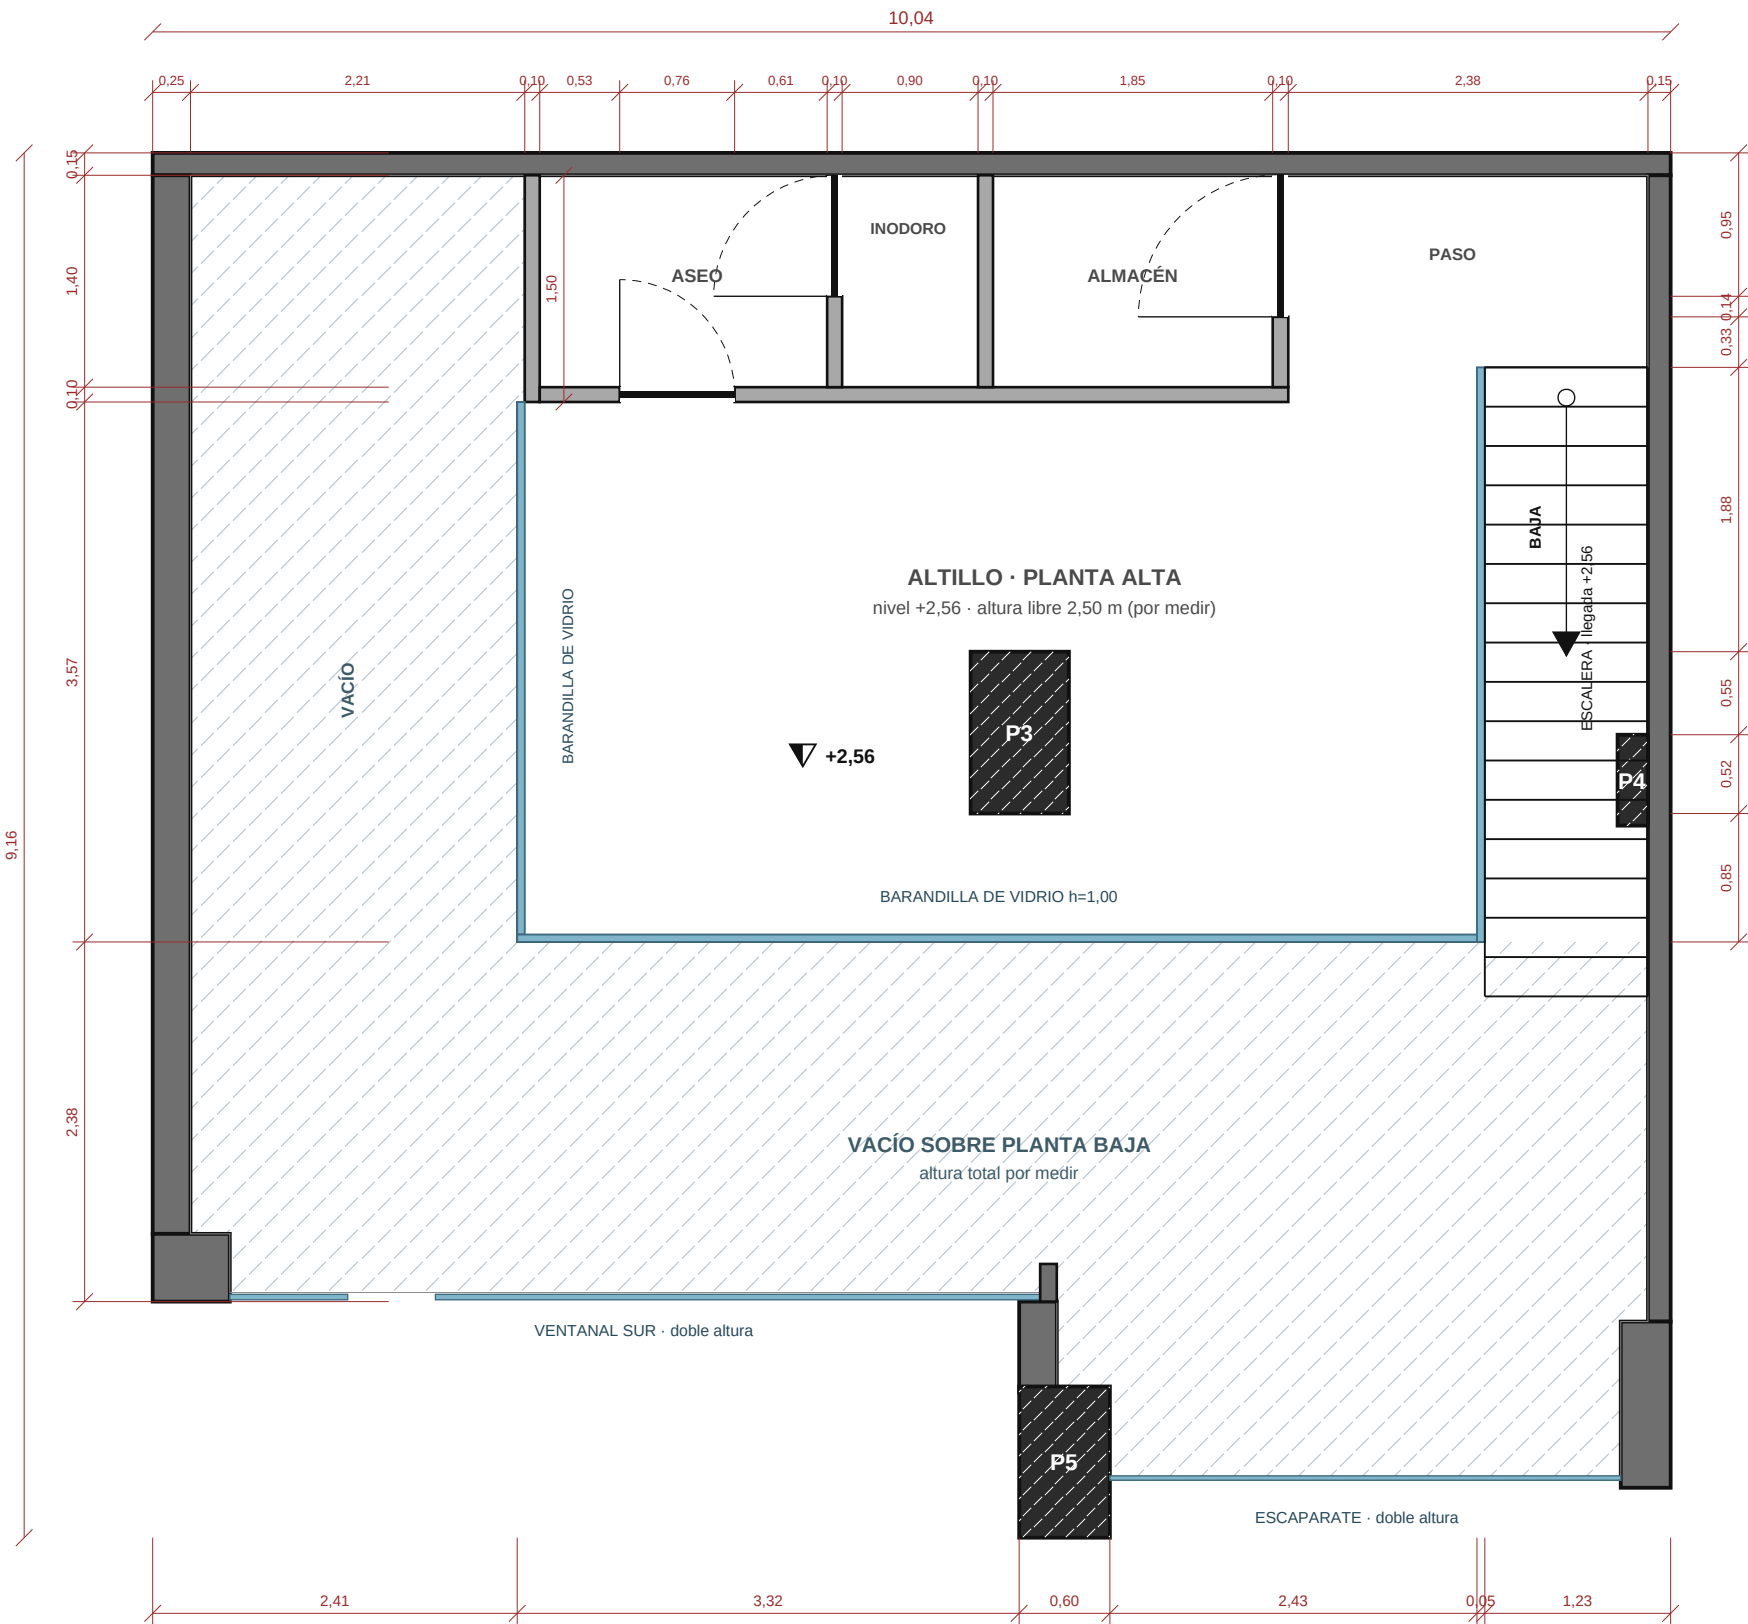

COMPROBAR EN OBRA Puntos en los que los vídeos del local no cuadran con el levantamiento, o que el levantamiento no recoge. Se dibuja el levantamiento por ser la única fuente acotada.

- La cota de 2,70 anotada contra la medianera norte no cuadra: mide la misma distancia que el 2,22 aplicado (muro Oeste a pared en L). Aclarar qué mide ese 2,70.
- Canto del forjado del altillo. Con 2,56 m de suelo a suelo, la altura libre de planta baja es 2,56 menos ese canto, no los 2,70 supuestos.
- Espesor de la pared en L y del panel de vidrio de 1,35 m que sostiene.
- Posición de P3: el 3,15 de la planta baja y el 1,90 de la planta alta se llevan 0,15; el 2,94 y el 3,20 se llevan 0,26. Se dibuja con la cadena de planta baja.
- Del P3 a la escalera se midió 2,35 y en el plano salen 2,75. Los 0,40 de diferencia no cierran contra la medianera Este.
- P5: se dibuja 0,60 x 1,00 con la cara Oeste a plomo con el muro del cuello. El resalto de 0,20 al Este anotado da 0,35 en esa posición.
- Escaparate: bajo él aparece un 2,70 sin aclarar. Se dibuja el hueco completo con la puerta de 2,10 pegada a P5.
- Tabica de la escalera: $2,56/17 = 0,151$ m. Contar los peldaños en obra para confirmar que son 17.
- Machones trasdosados con placa de yeso nueva: la sección de hormigón no es verificable a la vista.

ESCALA

1:50 (A3)

FECHA

14 set. 2026

PLANO

02 / 03

GRUPO SUMA

Reformas y proyectos · Málaga

PROYECTO
Reforma integral de local de hostelería

EMPLAZAMIENTO
Local en planta baja y altillo
Málaga

PLANO
EQUIPAMIENTO

Barra y cocina · distribución

LEYENDA



- Mueble bajo encimera
- Equipo refrigerado
- Encimera corrida
- Aparato sobre encimera
- Muro de carga / medianera
- Pilar o machón

HOLGURAS Y ALTURAS

Pasillo de trabajo en cocina	0,92 m
Paso de servicio en barra	1,02 m
Fondo de todos los muebles	0,60 m
Altura de encimera	0,90 m
Borde inferior de la campana	2,00 m

NOTAS

Anchos de serie de hostelería, no medidos sobre aparato. Sustituir por los del equipo que se elija.
La línea de cocción va en serie 600 y no en 700: con 2,12 m libres, un fondo de 700 dejaría el pasillo en 0,82 m, bajo el mínimo recomendado.
La trasbarra es un solo mueble con una sola encimera corrida; el módulo técnico T1 queda bajo la cafetera.
No hace falta cerrar la zona del ventanal: todo entra en los 2,75 m de trasbarra.

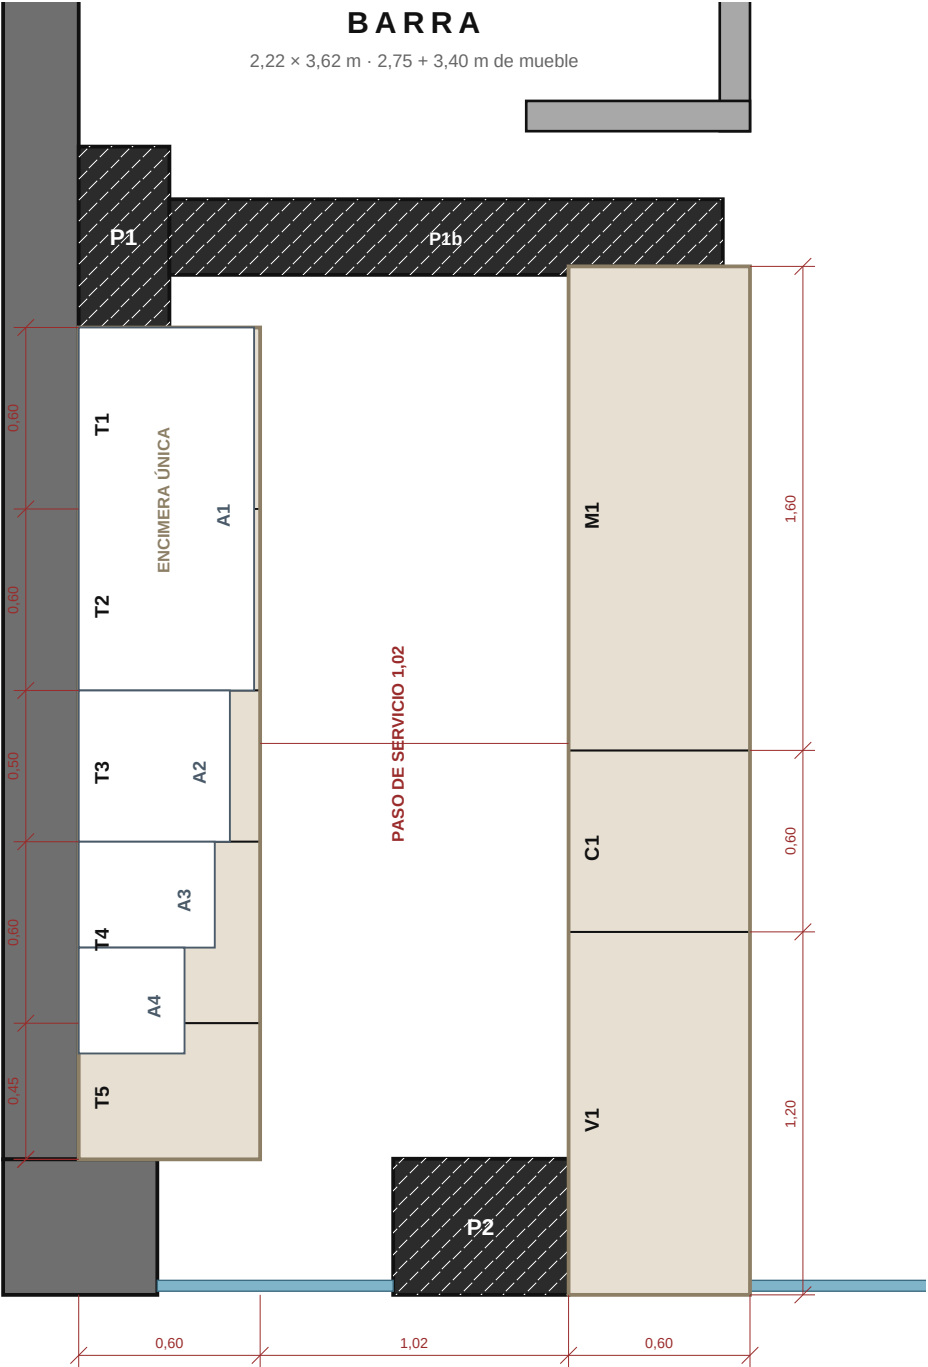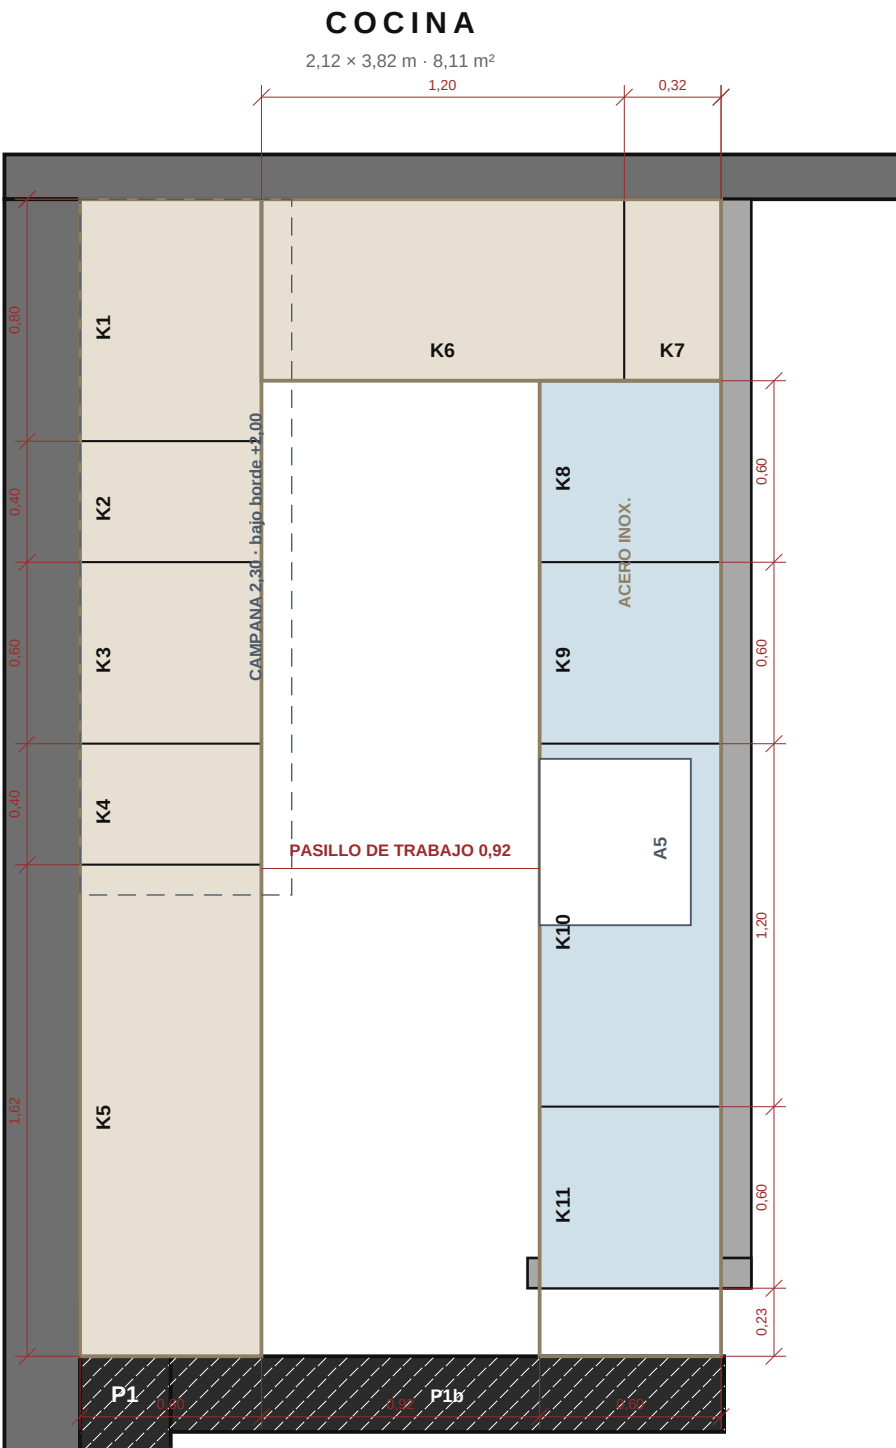

EQUIPAMIENTO

Ancho en metros. Serie de hostelería, pendiente de sustituir por el del equipo que se elija.

K1	Cocina de 4 fuegos	0,80	K9	Horno bajo encimera	0,60	V1	Vitrina expositora refrigerada	1,20
K2	Cocedor de pasta	0,40	K10	Mesa refrigerada de 2 puertas	1,20	C1	Caja y TPV	0,60
K3	Plancha	0,60	K11	Módulo de apoyo con estante	0,60	M1	Mostrador de servicio	1,60
K4	Freidora	0,40	T1	Módulo técnico: descalcificador, conexiones y cajón	0,60	A1	Cafetera de 2 grupos	1,20
K5	Mesa de trabajo	1,62	T2	Lavavajillas de barra, cesta 400 x 400	0,60	A2	Fregadero pequeño	0,50
K6	Fregadero de cocina, 2 cubetas con escurridor	1,20	T3	Mueble del fregadero	0,50	A3	Exprimidor de naranjas	0,35
K7	Módulo de apoyo	0,32	T4	Frigorífico bajo mostrador	0,60	A4	Tirador de cerveza	0,35
K8	Lavavajillas de cocina	0,60	T5	Cajonera	0,45	A5	Cortadora de fiambre	0,55

ESCALA

1:25 (A3)

FECHA

14 set. 2026

PLANO

03 / 03