

GRUPO SUMA

Reformas y proyectos · Málaga

PROYECTO

Reforma integral de local de hostelería

EMPLAZAMIENTO

Local en planta baja y altillo
Málaga

PLANO

PLANTA ALTA

Altillo +2,56 · estructura

LEYENDA

- Muro de carga / medianera
- Pilar o machón de hormigón
- Tabiquería
- Barandilla de vidrio
- Mesas y sillas (medidas promedio)
- Punto de luz
- Vacío sobre planta baja

SUPERFICIES Y ALTURAS

Forjado de planta alta	33,74 m²
Altillo diáfano	26,17 m²
Aseo (lavabo + inodoro)	3,92 m²
Almacén	2,59 m²
Nivel del forjado, medido	+2,56 m
Puestos de cowork	14

PILARES Y MACHONES (secciones en m)

P1 Machón del muro Oeste	0,30 × 0,60
P2 Pilastra del muro Sur	0,58 × 0,45
P3 Pilar central	0,65 × 1,07
P4 Machón de la medianera Este	0,20 × 0,60
P5 Pilar de fachada	0,60 × 1,00

NOTAS


Cotas en metros, tomadas sobre el levantamiento.

Nivel del forjado +2,56, medido en obra.

El forjado del altillo no cubre todo el local: la franja sur y oeste es un vacío a doble altura.

Mesa de cowork 2,40 × 1,00 para 8 puestos y dos redondas de Ø 0,80 con 3 sillas. Medidas promedio.


Un colgante por mesa y empotrados en el resto.

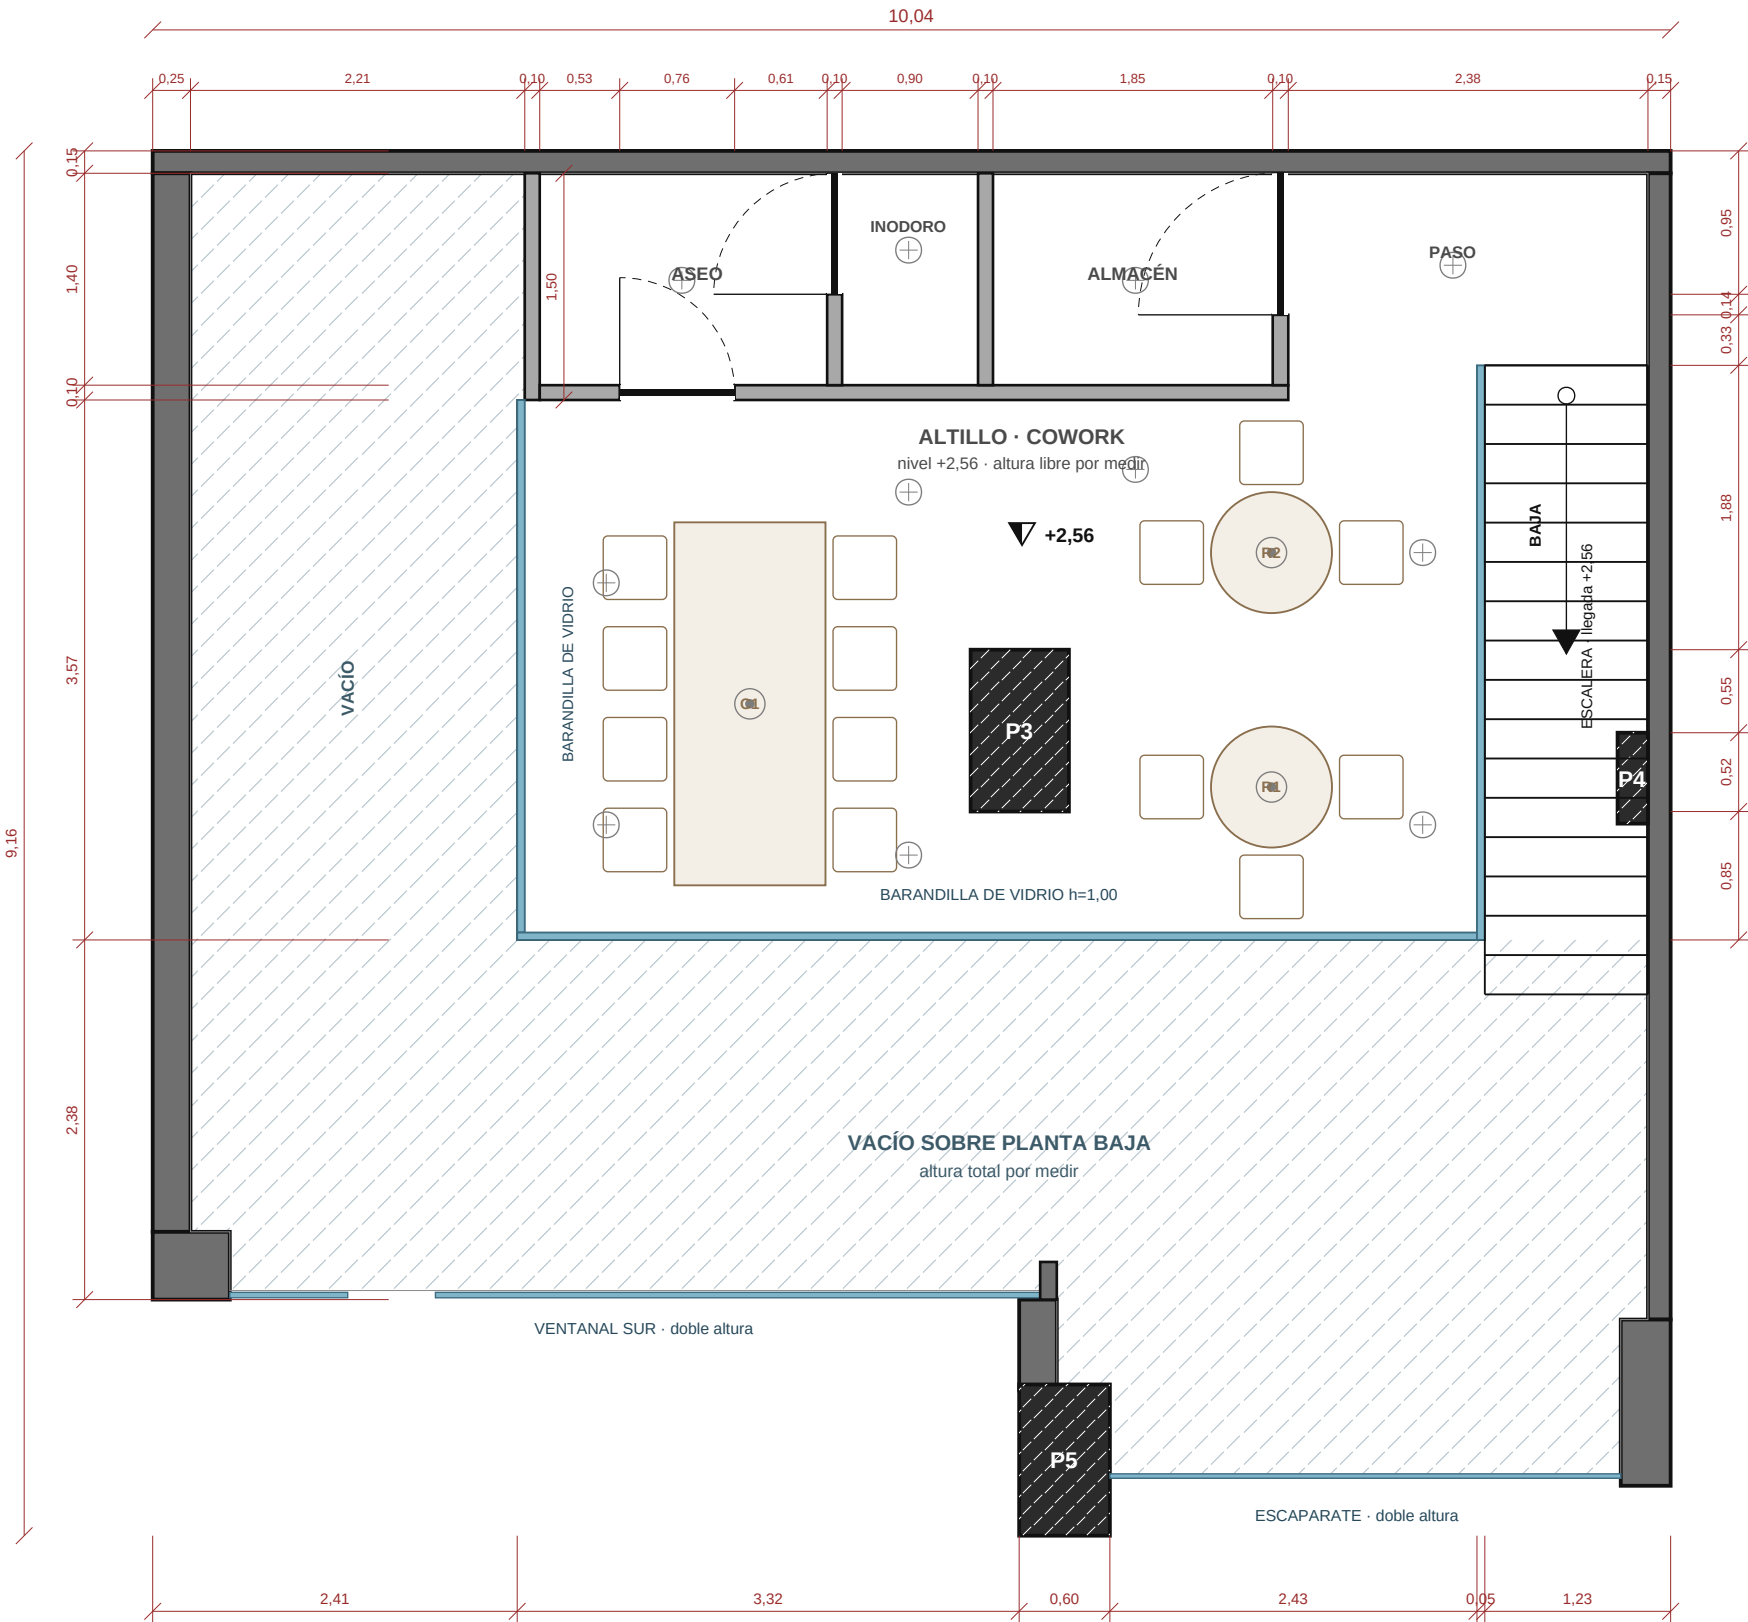

COMPROBAR EN OBRA

Puntos en los que los vídeos del local no cuadran con el levantamiento, o que el levantamiento no recoge. Se dibuja el levantamiento por ser la única fuente acotada.

- Pared en L: en el segundo croquis termina en y=5,35 (3,66 m) y la barra sube hasta 4,75 con el paso de 0,60 entre ambas. Antes se midió 4,22.
- Canto del forjado del altillo. Con 2,56 m de suelo a suelo, la altura libre de planta baja es 2,56 menos ese canto, no los 2,70 supuestos.
- P1b se dibuja como viga (1,83 × 0,25) y no como pilar: si fuera macizo hasta el suelo, la cocina no tendría entrada. Medir su intradós.
- Baño nuevo: tabiques de 0,10 y puerta de 0,70 tomados del croquis, sin medir. Comprobar que la puerta abre hacia dentro sin chocar.
- Posición de P3: el 3,15 de planta baja y el 1,90 de planta alta se llevan 0,15; el 2,94 y el 3,20 se llevan 0,26. Se usa la cadena de PB.
- Del P3 a la escalera se midió 2,35 y en el plano salen 2,75. Los 0,40 no cierran contra la medianera Este.
- Pasillo de cocina: 0,78 m frente a los frigoríficos (0,74 de fondo) y hasta 0,92 en el resto. Por debajo de 0,90 con permiso del cliente.
- Tabica de la escalera: 2,56/17 = 0,151 m. Contar los peldaños en obra.
- Máquinas: medidas de las fichas de makro.es según su buscador (la web bloquea el acceso directo). Sin dato: alto de la columna B4, 0,55 estimado.

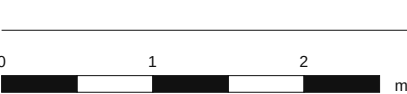

ESCALA

1:50 (A3)

FECHA

15 set. 2026

PLANO

02 / 03