

PROYECTO

Reforma integral de local de hostelería

EMPLAZAMIENTO

Local en planta baja y altílo
Málaga

PLANO

PLANTA BAJA

Estado actual · estructura

LEYENDA

- Muro de carga / medianera
- Pilar o machón de hormigón
- Pared en L y trasdosado del muro Norte
- Carpintería acristalada
- Espacio de doble altura
- Forjado sobre el corte
- Reserva de espacio del cliente
- Mesas dobles de 0,70 × 0,70 y sillas
- Nevera A7 · 0,54 × 0,58 (cara Sur de P3)
- Recorrido de sala · 0,70 por el Norte
- Punto de luz s/ proyecto original
- Aire acondicionado (cassette de techo)

SUPERFICIES Y ALTURAS

Planta baja, dentro de muros	75,25 m²
Zona de doble altura	37,79 m²
Suelo a suelo, medido en obra	2,56 m
Altura libre bajo forjado	2,56 – canto
Pared en L, altura	1,22 m
Mesas dobles / plazas sentadas	8 / 20
Acristalamiento de fachada	≈ 4,70 m


PILARES Y MACHONES (secciones en m)

P1 Machón del muro Oeste	0,30 × 0,60
P2 Pilastra del muro Sur	0,58 × 0,45
P3 Pilar central	0,65 × 1,07
P4 Machón de la medianera Este	0,20 × 0,60
P5 Pilar de fachada	0,60 × 1,00

NOTAS

Cotas en metros. Hundimiento, pared en L, P3, barra, zócalo y puerta con las medidas del 19 set.; el resto, del levantamiento. Sección a 1,20 m sobre el pavimento. Muro Norte: la barra (2,79) + 0,60 de paso llevan la base de la pared en L a la cara Norte de P1; la L mide 3,60 y llega al muro. El muro es macizo hasta el solar: 0,20 de espesor, 0,15 en la cocina por el hundimiento de 0,05. Mesas dobles de 0,70 × 0,70 que el personal junta. El sillón, 0,60 de fondo sin medir. Luces del proyecto. La nevera A7 sale 0,58 de la cara Sur de P3 y deja 0,45 hasta las sillas de M2: el paso a la barra da la vuelta por el Norte, con 0,70. Baño no accesible: 0,70.

0 1 2 m

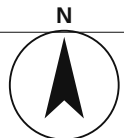

ESCALA


1:50 (A3)

FECHA

19 set. 2026

PLANO

01 / 04

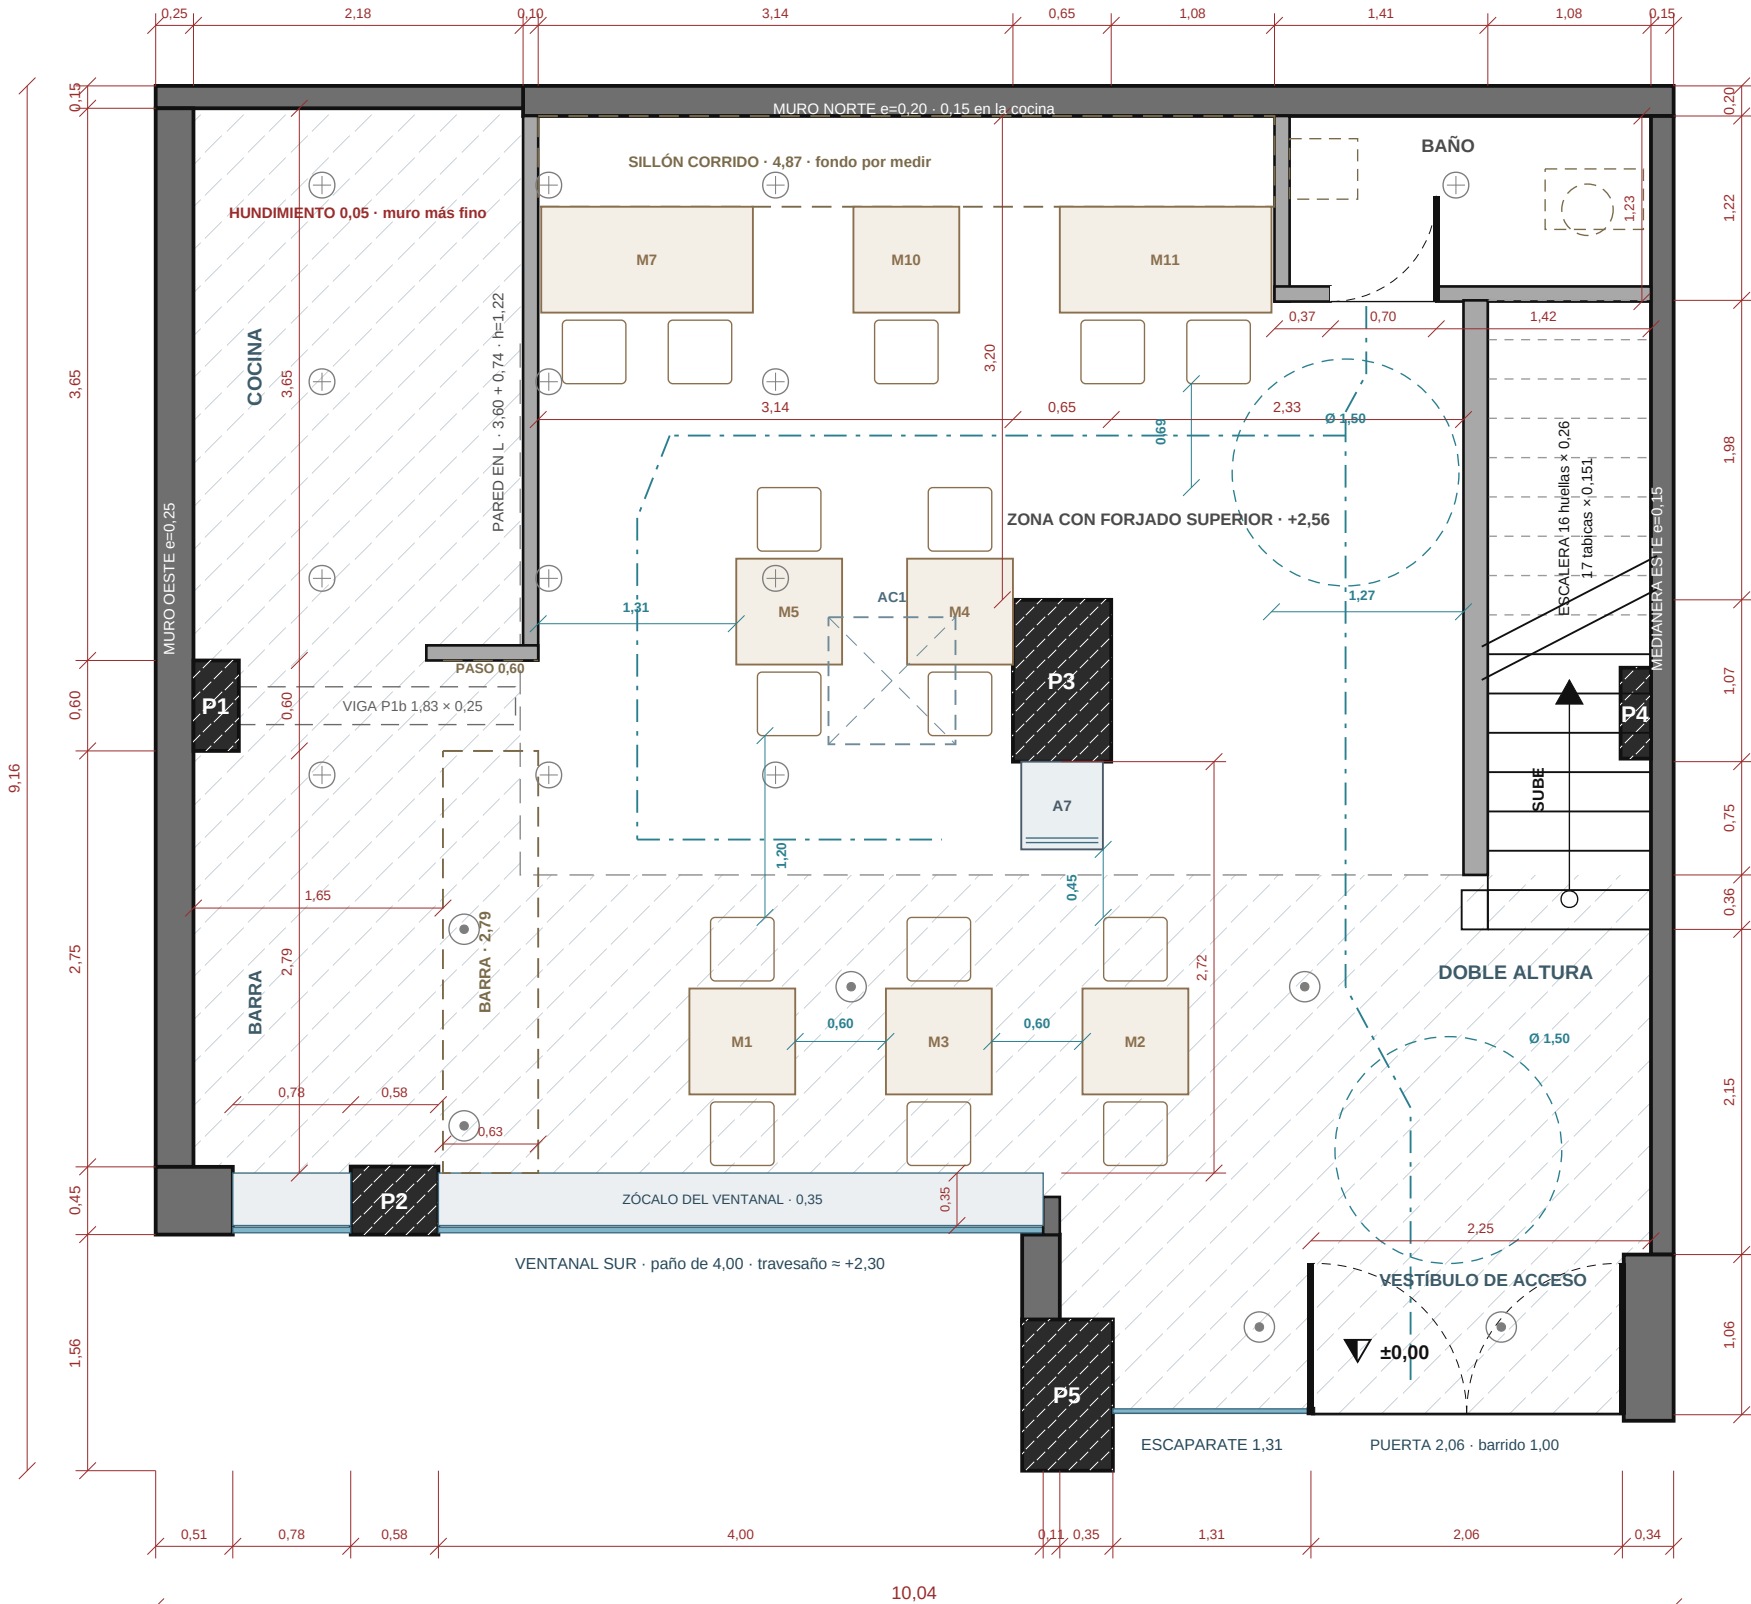

COMPROBAR EN OBRA Puntos en los que los vídeos del local no cuadran con el levantamiento, o que el levantamiento no recoge. Se dibuja el levantamiento por ser la única fuente acotada.

- Muro Norte: macizo hasta el solar, 0,148 en la cocina (el del levantamiento) y 0,199 en el resto. Medir ese espesor y el hundimiento de 0,05 entre los dos.
- Canto del forjado del altílo. Con 2,56 m de suelo a suelo, la altura libre de planta baja es 2,56 menos ese canto, no los 2,70 supuestos.
- P1b se dibuja como viga (1,83 × 0,25) y no como pilar: si fuera macizo hasta el suelo, la cocina no tendría entrada. Medir su intradós.
- Zócalo del ventanal: 0,347 desde el vidrio, deducido de los 2,72 de P3 a su cara interior; sobresale 0,16 del muro del ventanal (0,25). Medirlo directamente.
- Muro Oeste de la cocina: los cuatro aparatos suman 3,04 y entre P1 y la bancada hay 3,05. Entran con 1 cm de holgura: confirmar los anchos reales antes de comprar.
- La pared en L queda 0,10 al Este del borde del forjado del levantamiento: el vidrio de 1,35 sobre ella (2,57 en total) no pasa bajo el altílo. Medir ese borde.
- Vestíbulo: los 1,31 y 2,23 del cliente suman 3,54 y de P5 al muro Este hay 3,559. Se dibuja el 1,31 medido y el resto queda en 2,25, 2 cm más que su medida.
- P3 no se mueve: los 3,23 a la medianera dan 3,25 medidos al muro desnudo (2,98 al trasdosado) y los 3,65 a P5 se dibujan 3,69. Confirmar a qué cara se midió.
- Aire acondicionado: un solo cassette de 4 vías, empotrado en el forjado al Oeste de P3. Posición y panel (0,84) sacados de las fotos: medírlos en obra.